

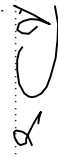
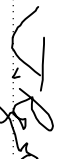


QR CODE	Scan to Check Document Version	REV	DATE	AMENDMENT / REVISION DESCRIPTION	APPROVAL	DRAWING FILE LOCATION / NAME	H:\SIGNS\TTT\DRAWINGS\SP\OTREG\LATR2-2.DWG
		01	23-08-18	AS Fonts & material classification raised	P. Oliver		
ALL DIMENSIONS ARE IN MILLIMETRES UNLESS OTHERWISE SPECIFIED							SIGN TO BE MANUFACTURED IN ACCORDANCE WITH RMS QA SPECIFICATION 3400
DESIGNED							VERIFIED
SIGNED: 							SIGNED: 
NAME: M. Davies							NAME: P. Oliver
DATE: 31-07-19							TITLE: Manager, Guidance & Delineation
REVIEWED							
SIGNED: 							DATE: 31-07-19
NAME: J. Rozdos							
DATE: 31-07-19							
PREPARED BY							GUIDANCE AND DELINEATION UNIT
NSW GOVERNMENT							TRAFFIC ENGINEERING SERVICES
Transport Roads & Maritime Services							TECHNICAL AND PROJECT SERVICES
REGULATORY SIGN							A
R2-2(L)							
ONE WAY (LEFT ARROW SYMBOLIC)							
SCALE: 1:10							EDMS No. XXXXXXXXXX
							SHEET No. 1
							ISS 0
							SHEET 1 OF 1


ACCEPTED FOR CONSTRUCTION

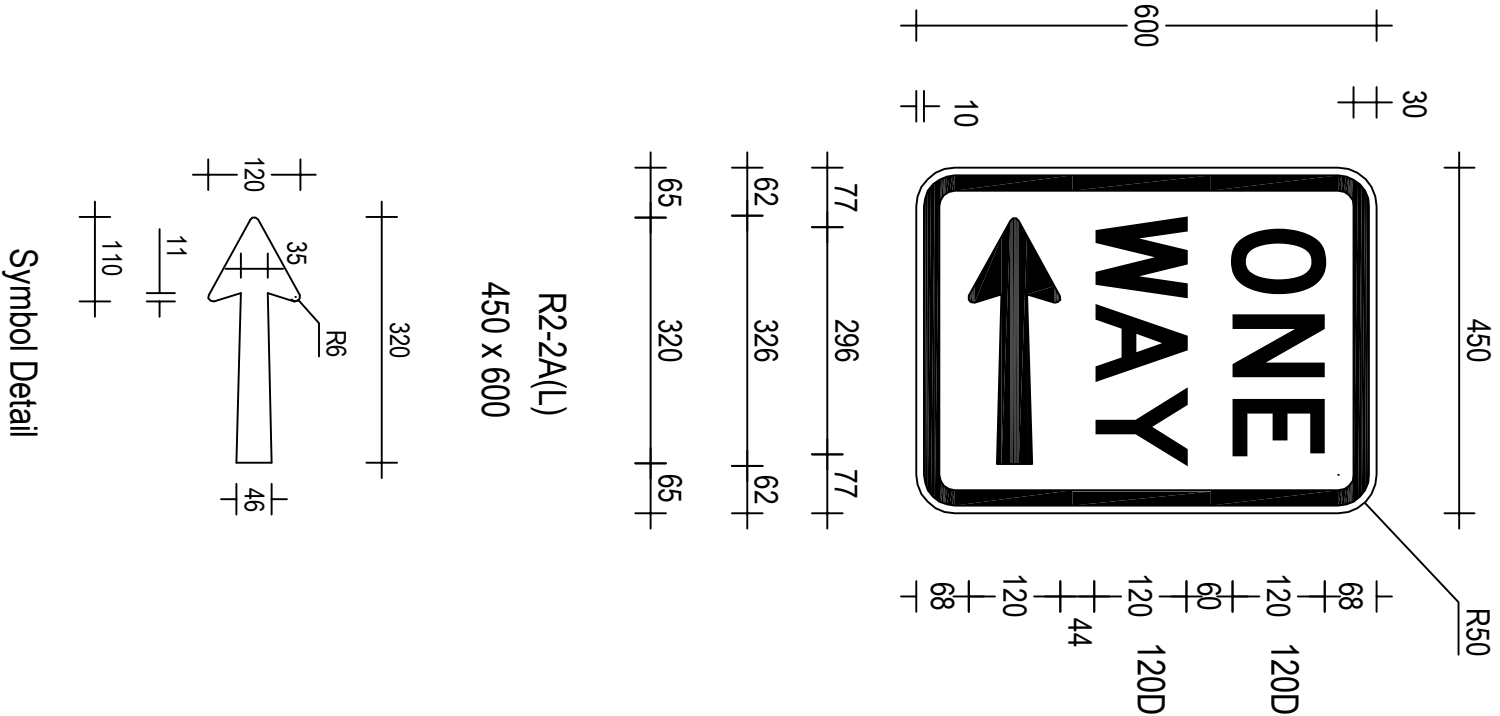


R2-2A(L)
450 x 600

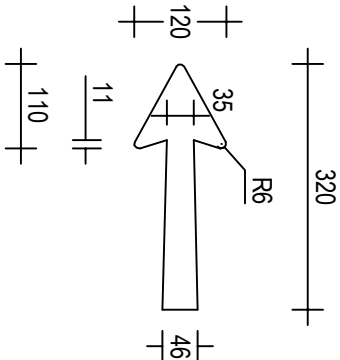

Symbol Detail

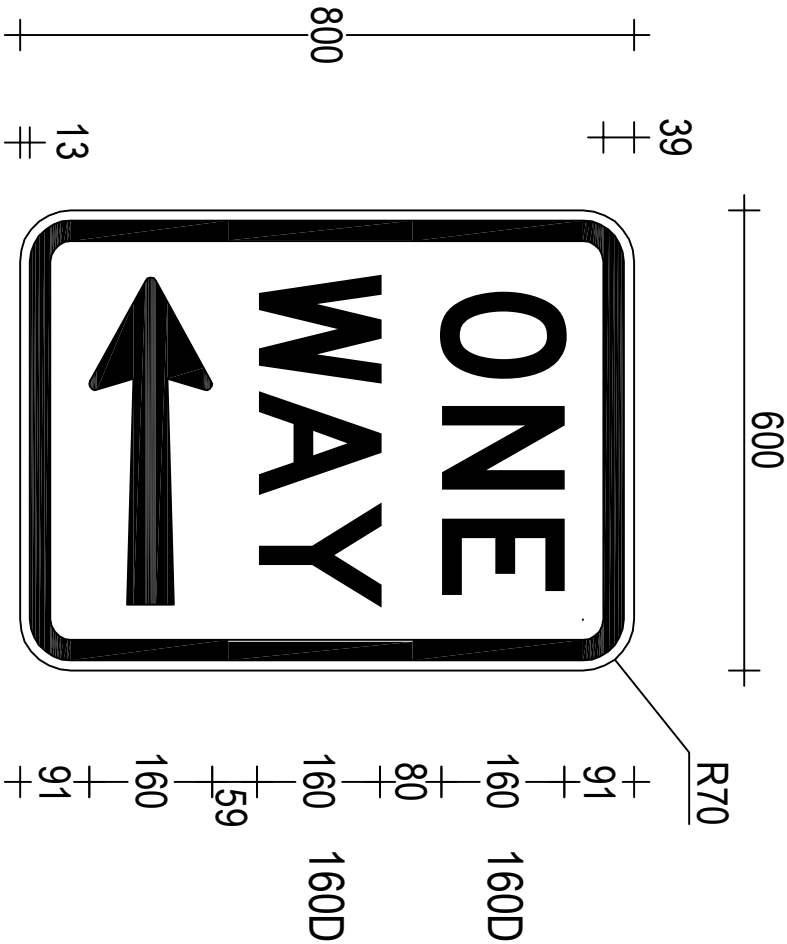

R2-2B(L)
600 x 800

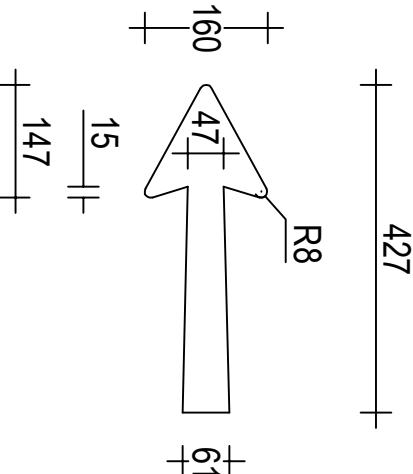

Symbol Detail