
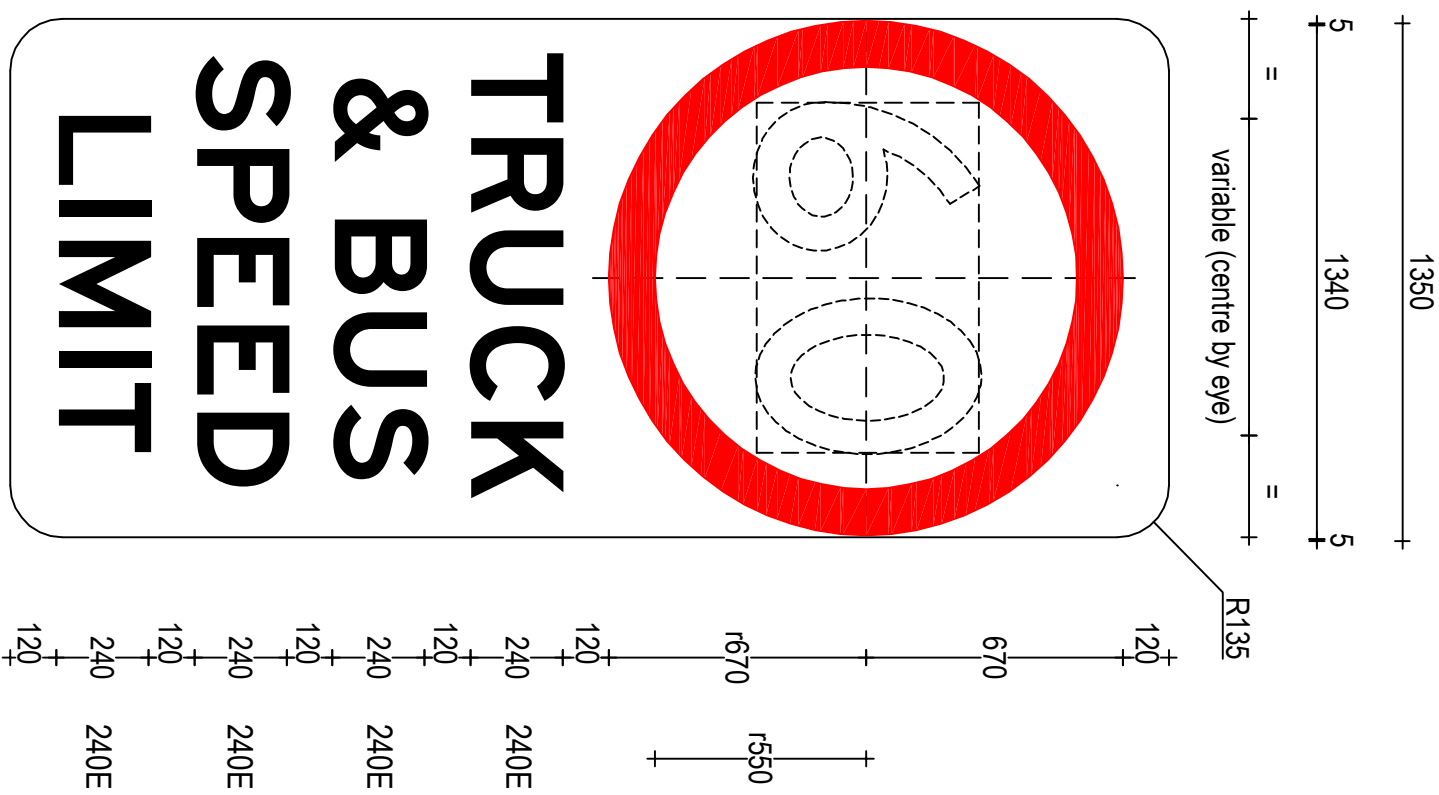
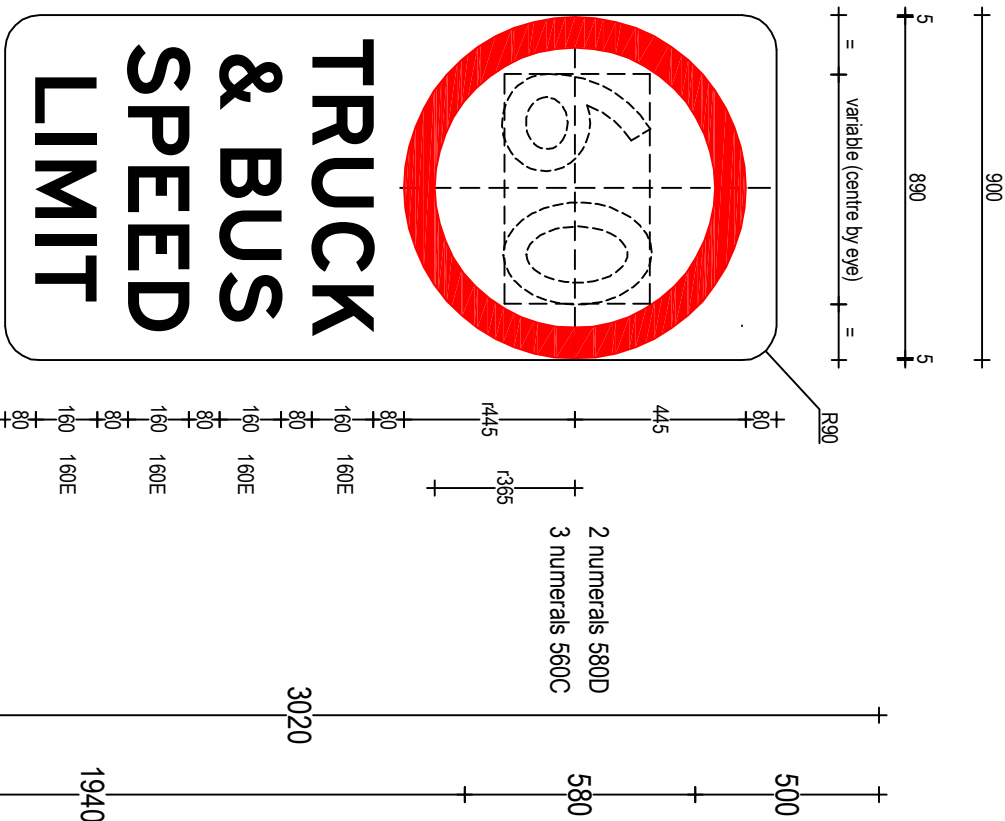


25	08 CODE	Scan to Check Document Version	REV /	DATE	AMENDMENT / REVISION DESCRIPTION	APPROVAL	DRAWING FILE LOCATION / NAME	H:\SIGNS\TIDDAIRAINNS\PLOT\REGULAT-R229.DWG	DESIGNED	SIGNED	VERIFIED	 Transport Roads & Maritime Services PREPARED BY GUIDANCE AND DELINEATION UNIT TRAFFIC ENGINEERING SERVICES TECHNICAL AND PROJECT SERVICES REGULATORY SIGN R4-229N TRUCK & BUS SPEED LIMIT SHEET 1 OF 1 SCALE: 1:20 EDMS No. XXXXXXXXXX SHEET No. 1 ISS 0 A			
20			01	23-08-18	AS Form & material classification revised	P.Oliver			NAME	M. Davies	SIGNED		P. Oliver		
15									DATE	31-07-19	TITLE		Manager Guidance & Delineation		
10									SIGNED		DATE		31-07-19		
5									NAME	J. Rozdos					
0									DATE	31-07-19					
ALL DIMENSIONS ARE IN MILLIMETRES UNLESS OTHERWISE SPECIFIED													SIGN TO BE MANUFACTURED IN ACCORDANCE WITH RMS QA SPECIFICATION 3400		
MATERIALS: ALUMINIUM SIGN BLACK LEGEND ON AS1906.1 CL.400 WHITE REFLECTORISED GROUND WITH AS1906.1 CL.400 RED REFLECTORISED ANNULUS															

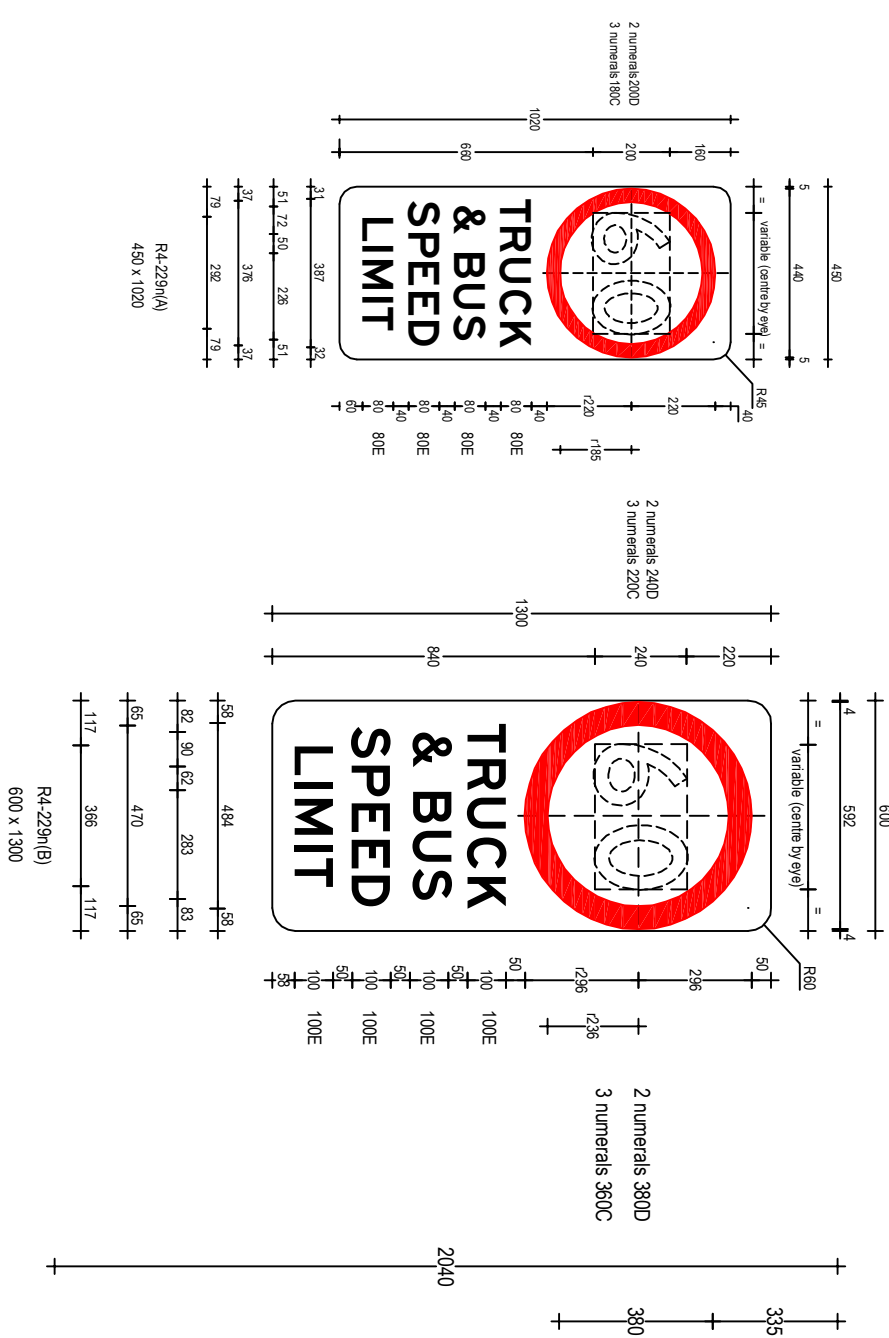

R4-229n(D)
1350 x 3020

ACCEPTED FOR CONSTRUCTION