
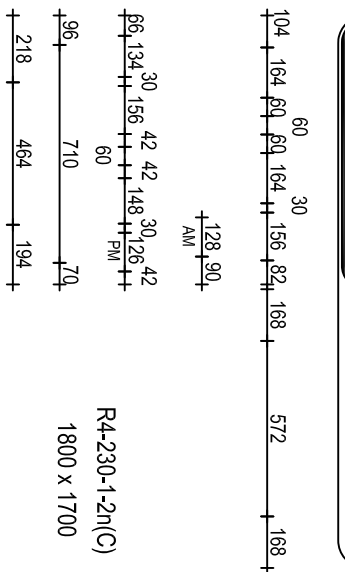
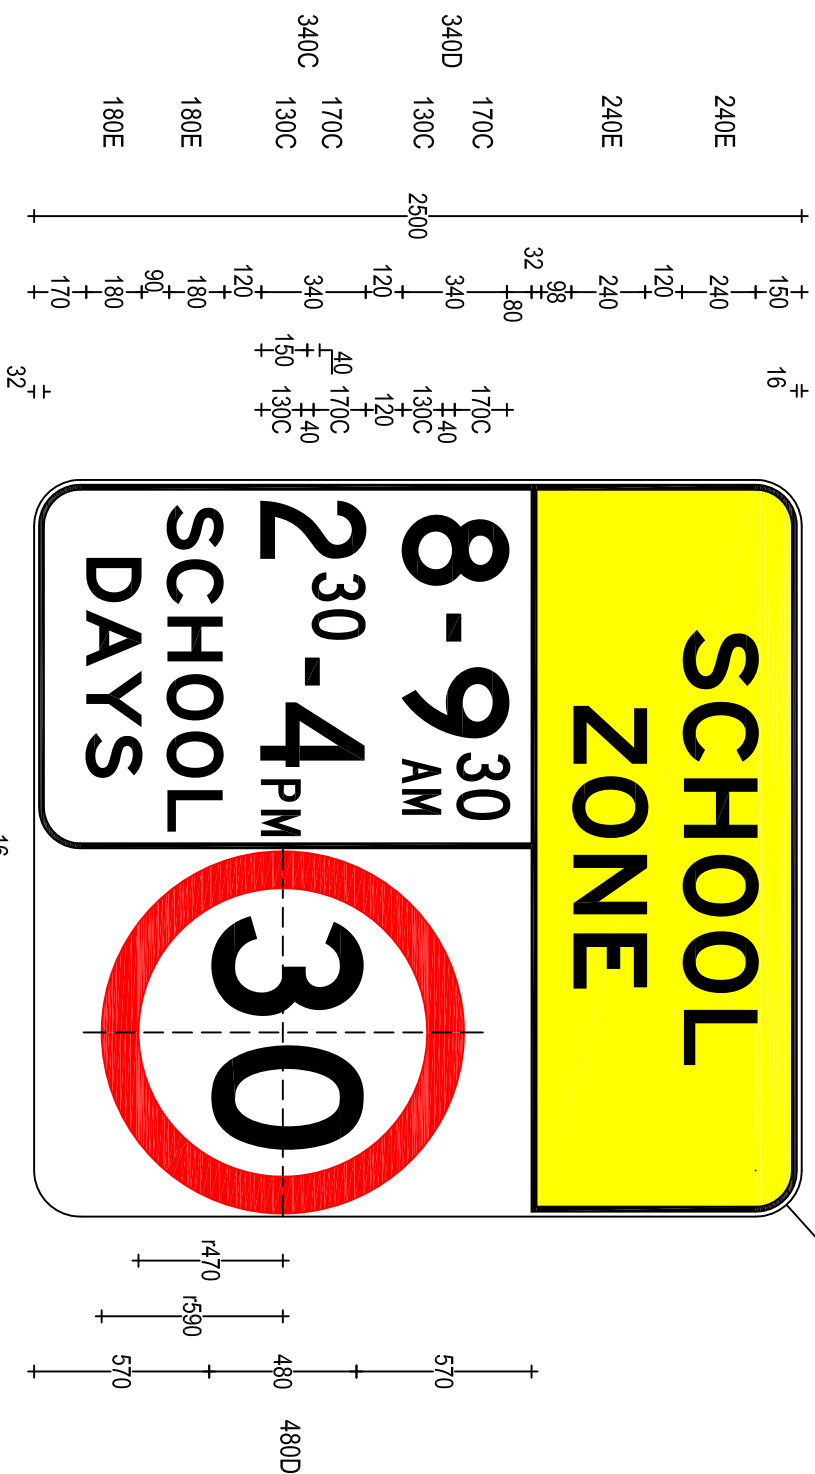


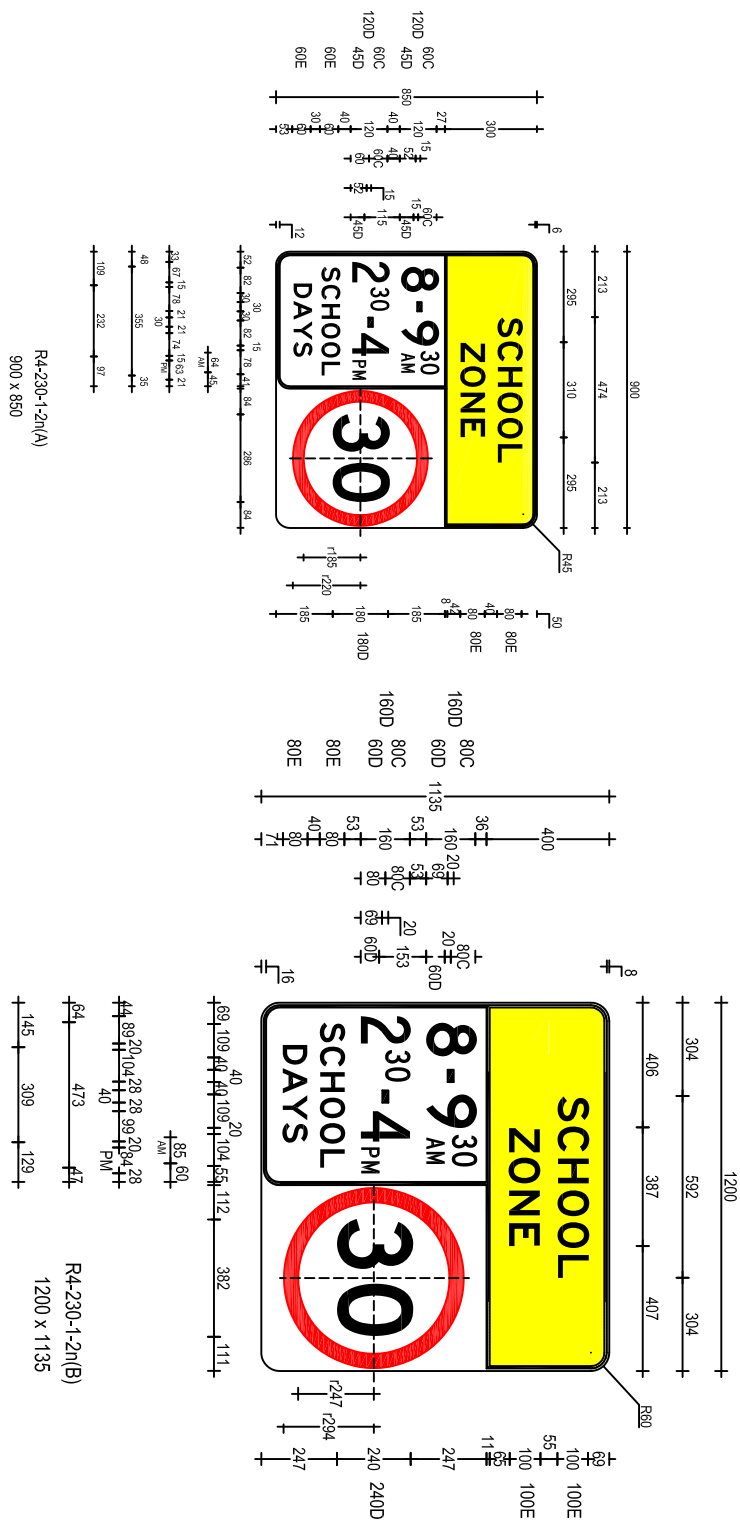

Note:- For Non Standard Times use R4-235m

ALL DIMENSIONS ARE IN MILLIMETRES UNLESS OTHERWISE SPECIFIED					SIGN TO BE MANUFACTURED IN ACCORDANCE WITH RMS QA SPECIFICATION 3400	
OR CODE	Sign to Check Document Version	REV	DATE	AMENDMENT / REVISION DESCRIPTION	APPROVAL	DRAWING FILE LOCATION / NAME: H:\SIGN\TIDORAWINGS\PILOT\REGULATORY\R4-230-1-2.DWG
		01	23-06-18	AS Forms & material classification revised	P Oliver	
MATERIALS: ALUMINIUM SIGN						
TOP PANEL:-BLACK LEGEND AND BORDER ON CL400						
FLUORESCENT YELLOW GREEN GROUND, LHS & RHS BLACK GROUND						
BOTTOM PANEL:- BLACK LGD & BDR ON CL400 WHITE REFL GROUND						
WITH CL400 RED REFLECTORISED ANNULUS						
DESIGNED		VERIFIED				
SIGNED		SIGNED				
NAME M.Davies		NAME P. Oliver				
DATE 31-07-19		DATE 31-07-19				
REVIEWED		TITLE Manager, Guidance & Delineation				
SIGNED		DATE 31-07-19				
NAME J. Rozos						
DATE 31-07-19						
 NSW GOVERNMENT Transport Roads & Maritime Services PREPARED BY GUIDANCE AND DELINEATION UNIT TRAFFIC ENGINEERING SERVICES TECHNICAL AND PROJECT SERVICES						
REGULATORY SIGN						A3
R4-230-1-2N						SHEET 1 OF 1
SCHOOL ZONE (8-930AM 230-4PM)						
SCHOOL DAYS (30)						
SCALE: 1:25		EDMS No.	SHEET No.	1	ISSUE	01