
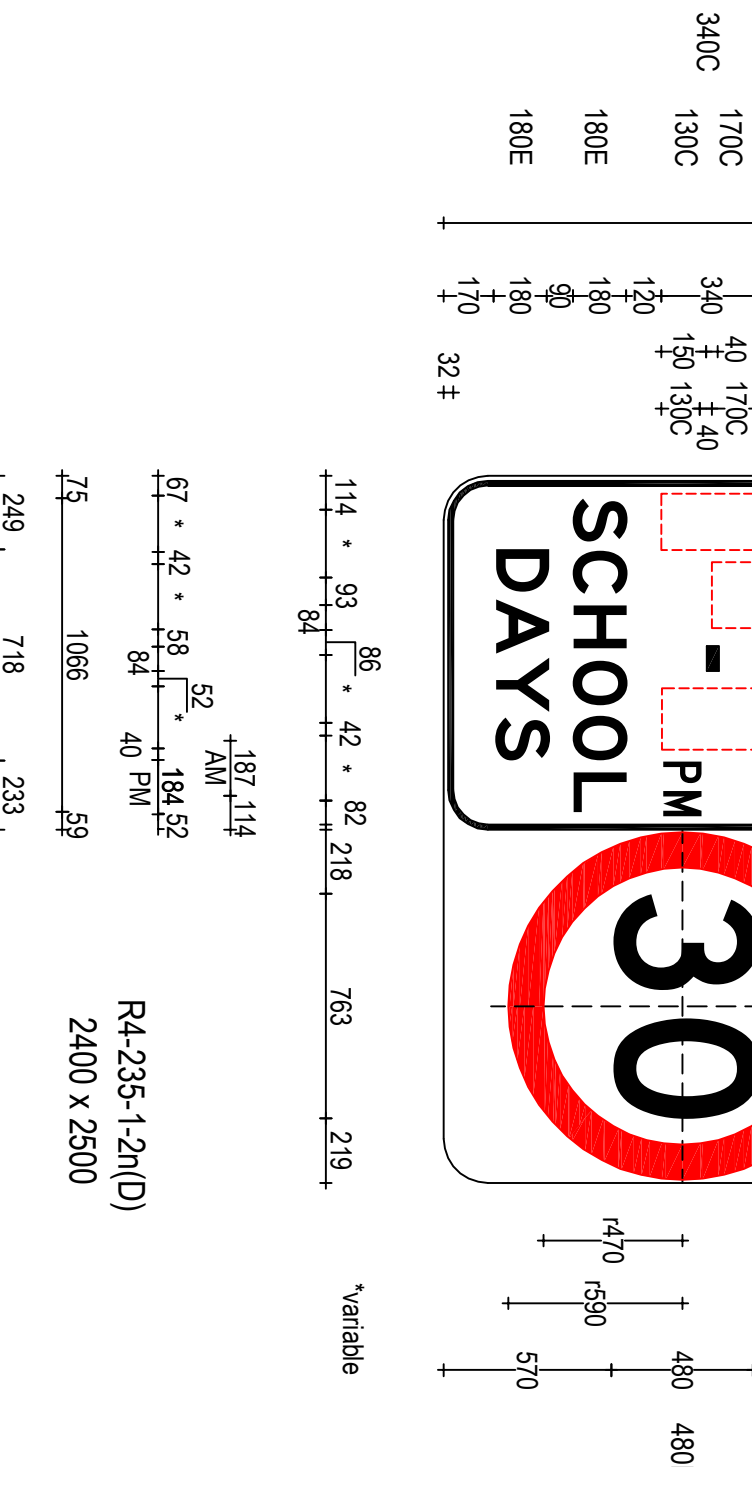
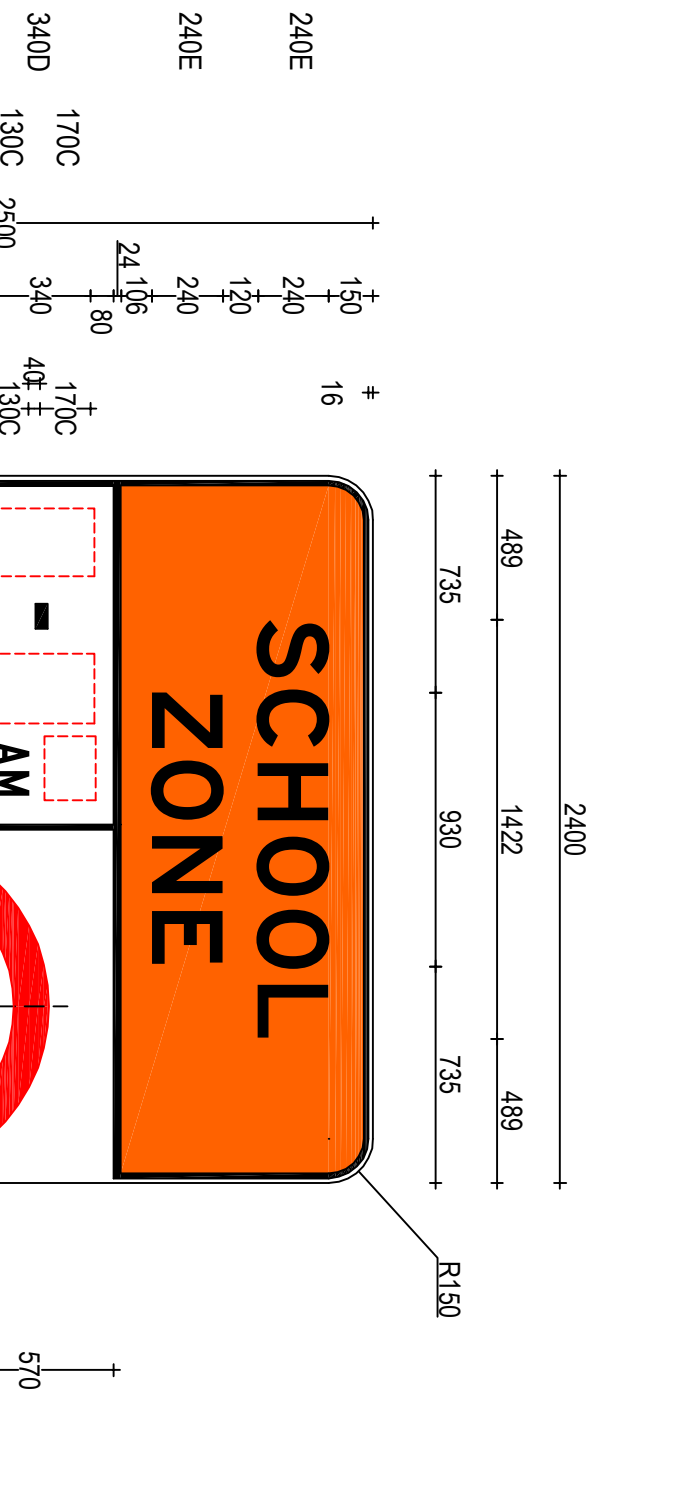


ACCEPTED FOR CONSTRUCTION

Note:- For standard times (8-9.30am & 2.30-4pm) use R4-230n

R4-235-1-2n(C)
1800 x 1700

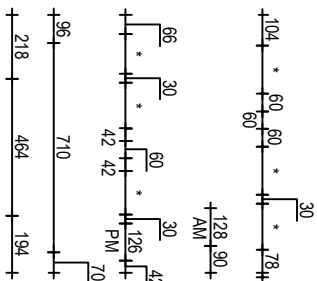

ACCEPTED FOR CONSTRUCTION

REGULATORY SIGN

R4-235-1-2N

SCHOOL ZONE (Times) SCHOOL DAYS

(30) SHEET 1 OF 1

SCALE: 1:20

CD 2

M. Davies

31-07-19

MED

...

31-07-19

VED

ED

SIGNED _____

NAME P.Oliver

TITLE..... **Manager Guidance & Delin**

DATE 31-07-19



Transport
Roads & Maritime
Services

PREPARED BY
GUIDANCE AND DELINEATION UNIT
TRAFFIC ENGINEERING SERVICES
TECHNICAL AND PROJECT SERVICES

*variable