


R5-39

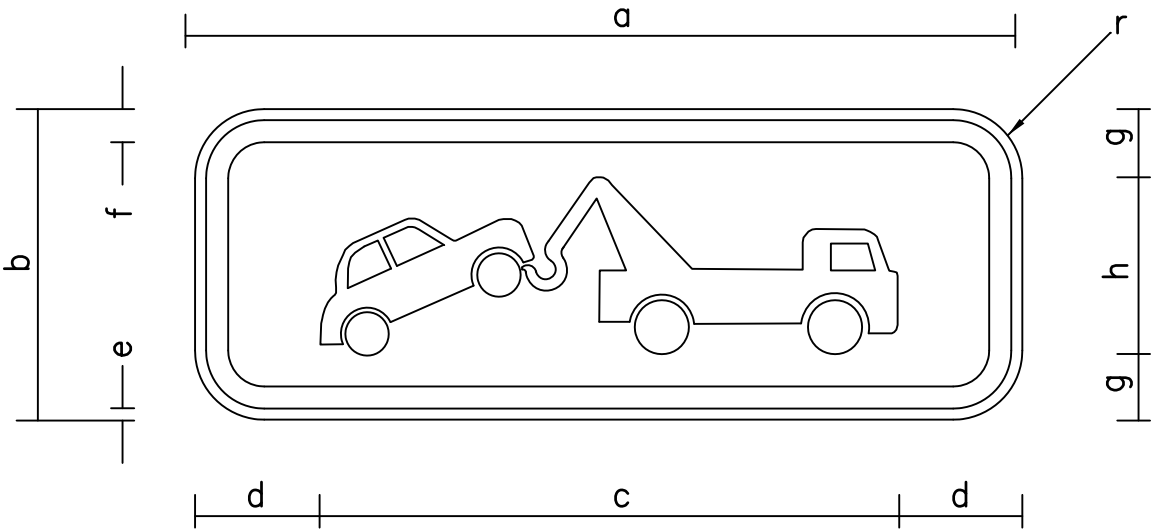

Black legend and border on Cl.1 white reflectorised ground

	a	b	c	d	e	f	g	h	r
R5-39A	600	225	414	93	8	24	48	129	50
R5-39B	900	337	621	139	12	36	72	193	75

SCALE 1:2500

TITLE

REGULATORY SIGN
R5-39

Drawn: MD 26-3-18
CHKED: MD 26-3-18



Transport
Roads & Maritime
Services

GUIDANCE AND DELINEATION UNIT
27-31 ARGYLE ST, PARRAMATTA 2150

H:\SIGNS\TIT\DRAWINGS\LOT\REGULAT\ r5-39.DWG

Revision: -