
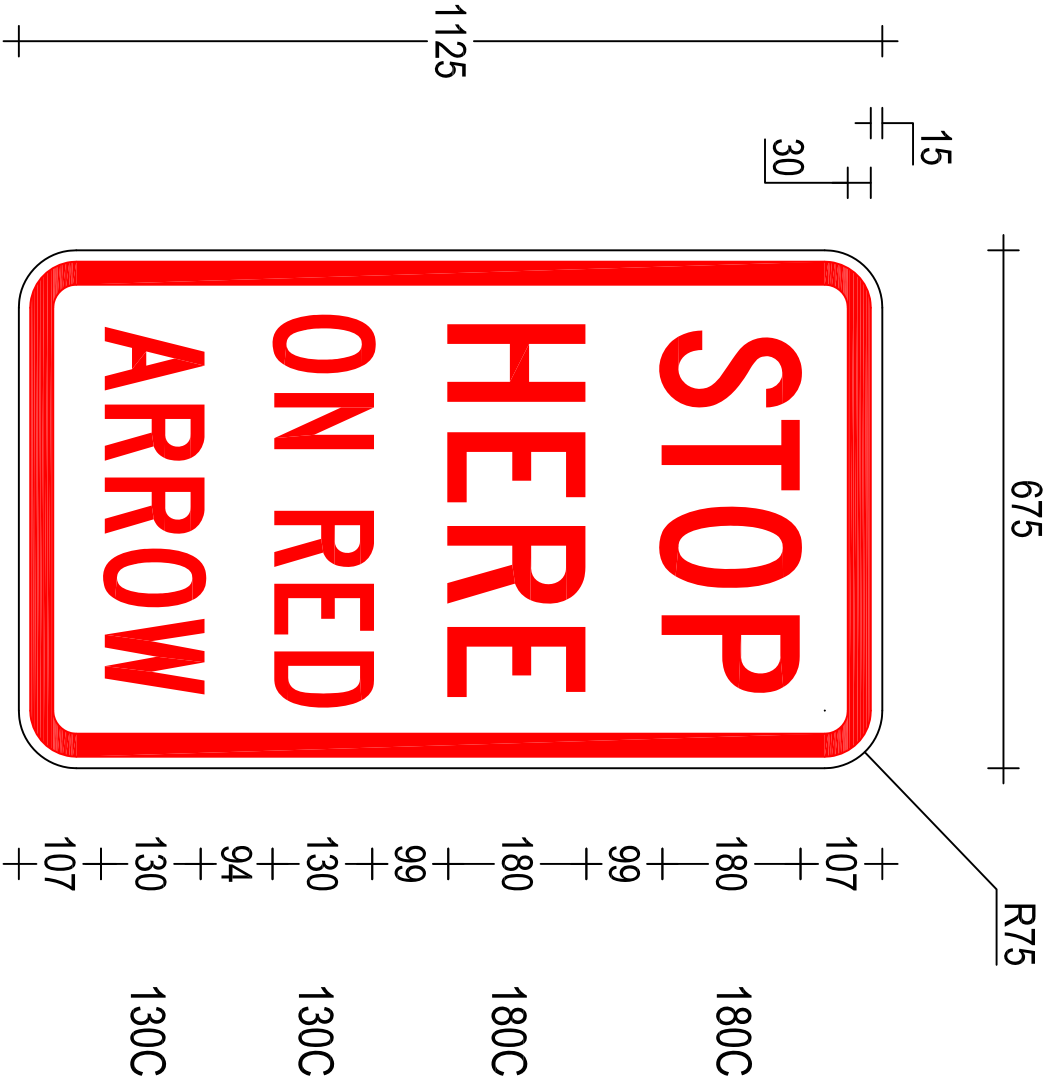


05101520253035404550mm ON A3 SIZE ORIGINAL

OR CODE		Scan to Check Document Version	REV	DATE	AMENDMENT / REVISION DESCRIPTION	APPROVAL	DRAWING FILE LOCATION / NAME: H:\SIGNS\TTT\DRAWINGS\PLOT\REGULATR-R6-14.DWG	DESIGNED	VERIFIED	REGULATORY SIGN				A3
			01	23-03-18	AS Forms & material classification revised	P. Oliver		MATERIALS: ALUMINIUM SIGN AS1906.1 CL.400 RED REFLECTORISED LEGEND AND BORDER ON AS1906.1 CL.400 WHITE REFLECTORISED GROUND SIGNED NAME M. Davies DATE 31-07-19 REVIEWED SIGNED NAME J. Rozos DATE 31-07-19	SIGNED NAME P. Oliver TITLE Manager, Guidance & Delineation DATE 31-07-19  Transport Roads & Maritime Services GOVERNMENT	STOP HERE ON RED ARROW				
ALL DIMENSIONS ARE IN MILLIMETRES UNLESS OTHERWISE SPECIFIED							SIGN TO BE MANUFACTURED IN ACCORDANCE WITH RMS QA SPECIFICATION 3400	SHEET 1 OF 1						
										PREPARED BY GUIDANCE AND DELINEATION UNIT TRAFFIC ENGINEERING SERVICES TECHNICAL AND PROJECT SERVICES	SCALE: 1:10	EDMS No. XXXXXXXXXX	SHEET No. 1	ISSUE 01

R6-14(A)
450 x 750

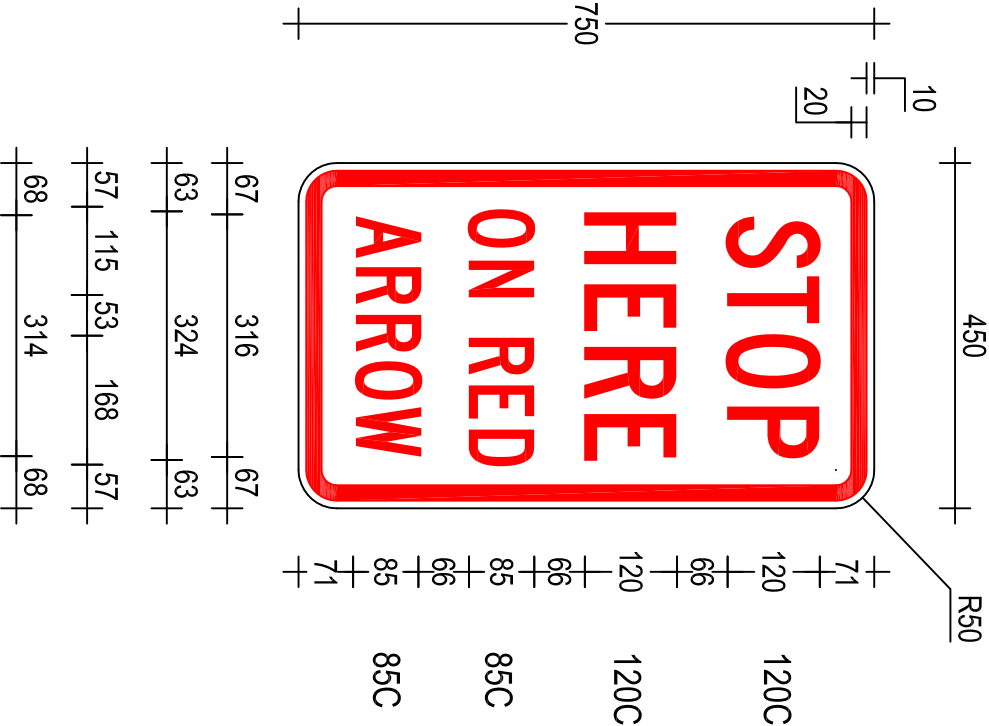

R6-14(B)
675 x 1125

ACCEPTED FOR CONSTRUCTION