


OR CODE	Scan to Check Document Version	REV	DATE	AMENDMENT / REVISION DESCRIPTION	APPROVAL	DRAWING FILE LOCATION / NAME: H:\SIGN\TTT\DRAWINGS\PLOT\REGULAT\TR6-26.DWG	
	01	23-03-18		AS Forms & material classification revised	P. Oliver		
ALL DIMENSIONS ARE IN MILLIMETRES UNLESS OTHERWISE SPECIFIED						SIGN TO BE MANUFACTURED IN ACCORDANCE WITH RMS QA SPECIFICATION 3400	
DESIGNED						VERIFIED	
SIGNED NAME M. Davies DATE 31-07-19						SIGNED NAME P. Oliver DATE 31-07-19	
REVIEWED SIGNED NAME J. Rozdos						TITLE Manager Guidance & Definition	
DATE 31-07-19						PREPARED BY GUIDANCE AND DELINEATION UNIT TRAFFIC ENGINEERING SERVICES TECHNICAL AND PROJECT SERVICES	
REGULATORY SIGN						A3	
R6-26 TRAMWAY CROSSING						SHEET 1 OF 1	
SCALE: 1:10						EDMS No. XXXXXXXXXX SHEET No. 1 ISSUE 01	

R6-26
1350 x 900
* non-standard spacing

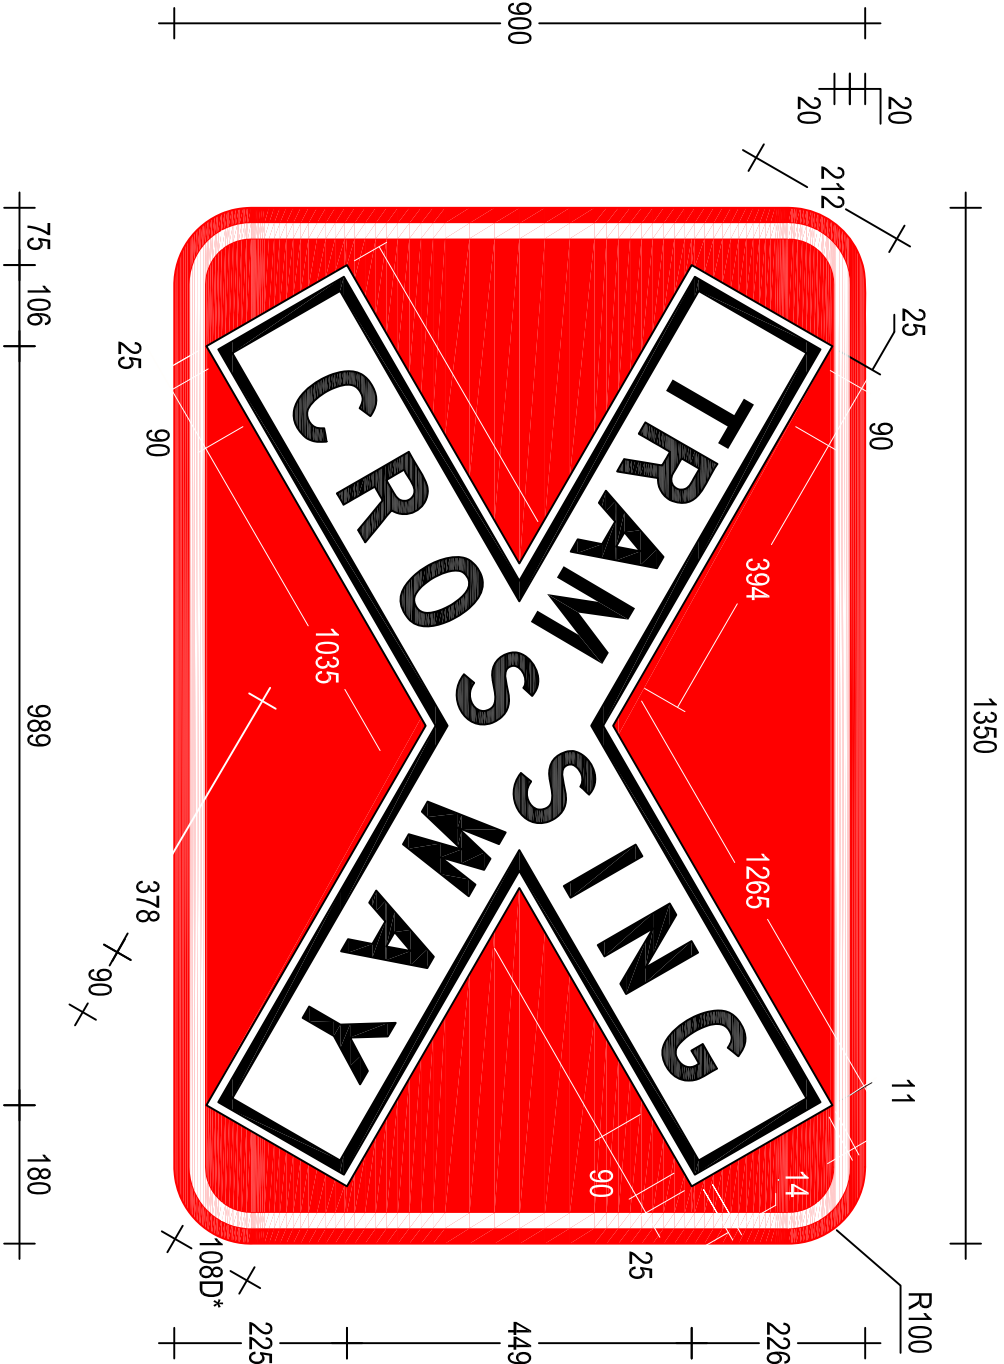

ACCEPTED FOR CONSTRUCTION