


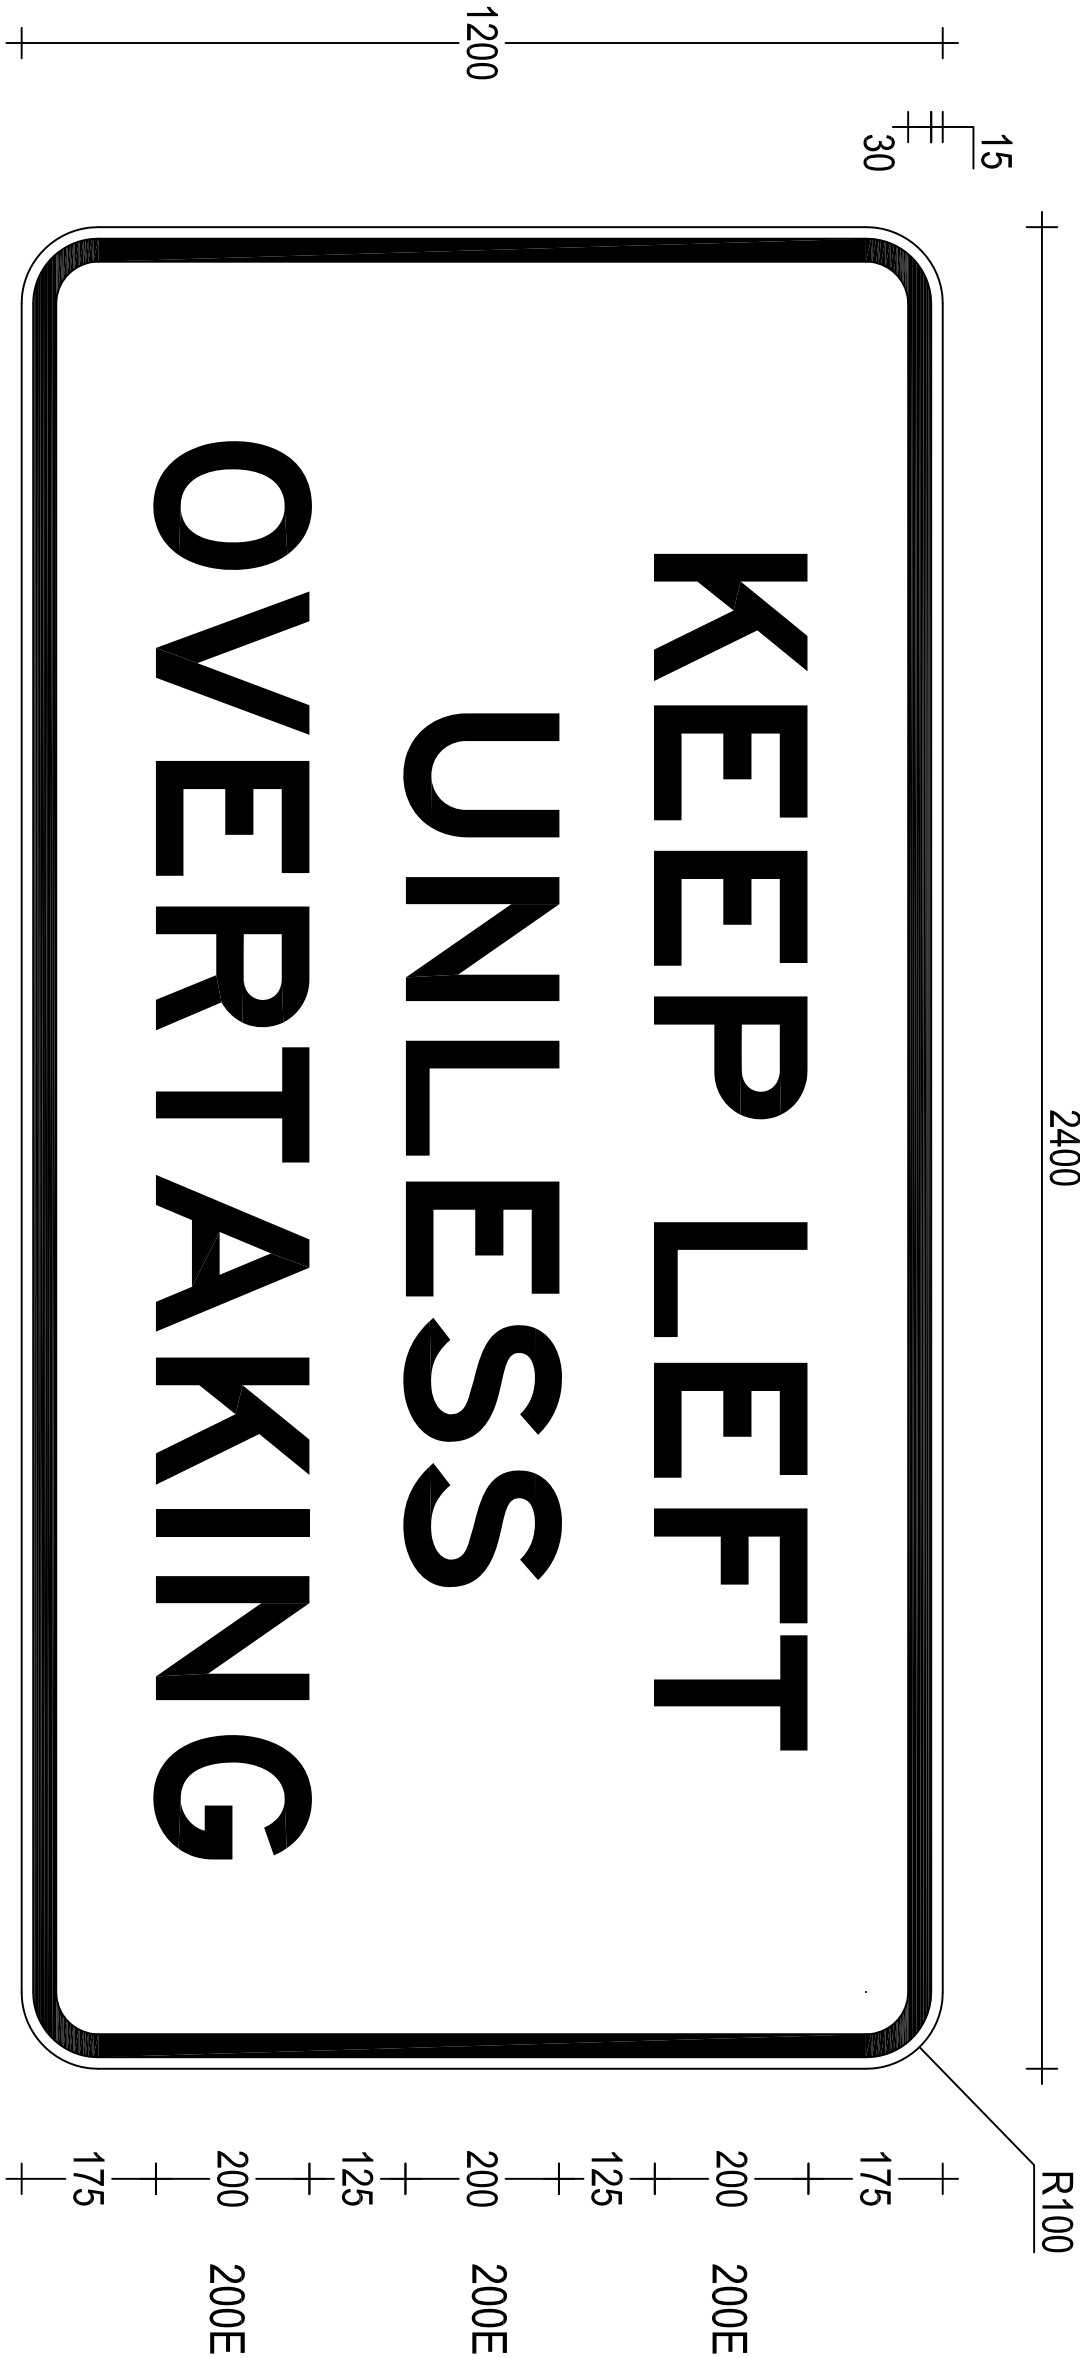

R6-29(C)
2400 x 1200

ACCEPTED FOR CONSTRUCTION

OR CODE		Scan to Check Document Version		REV	DATE	AMENDMENT / REVISION DESCRIPTION	APPROVAL	DRAWING FILE LOCATION / NAME: H:\SIGN\TTP\DRAWINGS\PLOT\REGULATR\R6-29.DWG	
				01	23-03-18	AS Forms & material classification revised	P.Oliver	MATERIALS: ALUMINIUM SIGN BLACK LEGEND AND BORDER ON AS1906.1 CL.400 WHITE REFLECTORISED GROUND	
ALL DIMENSIONS ARE IN MILLIMETRES UNLESS OTHERWISE SPECIFIED								SIGN TO BE MANUFACTURED IN ACCORDANCE WITH RMS QA SPECIFICATION 3400	
DESIGNED				VERIFIED				PREPARED BY	
SIGNED:  NAME: M. Davies DATE: 31-07-19				SIGNED:  NAME: P. Oliver TITLE: Manager Guidance & Delineation DATE: 31-07-19				NSW GOVERNMENT Transport Roads & Maritime Services PREPARED BY GUIDANCE AND DELINEATION UNIT TRAFFIC ENGINEERING SERVICES TECHNICAL AND PROJECT SERVICES	
SIGNED:  NAME: J. Rozdos DATE: 31-07-19								REGULATORY SIGN R6-29 KEEP LEFT UNLESS OVERTAKING	
SCALE: 1:10				EDMS No. XXXXXXXXXX		SHEET No. 1		ISSUE 01	