
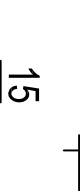
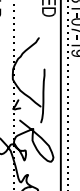
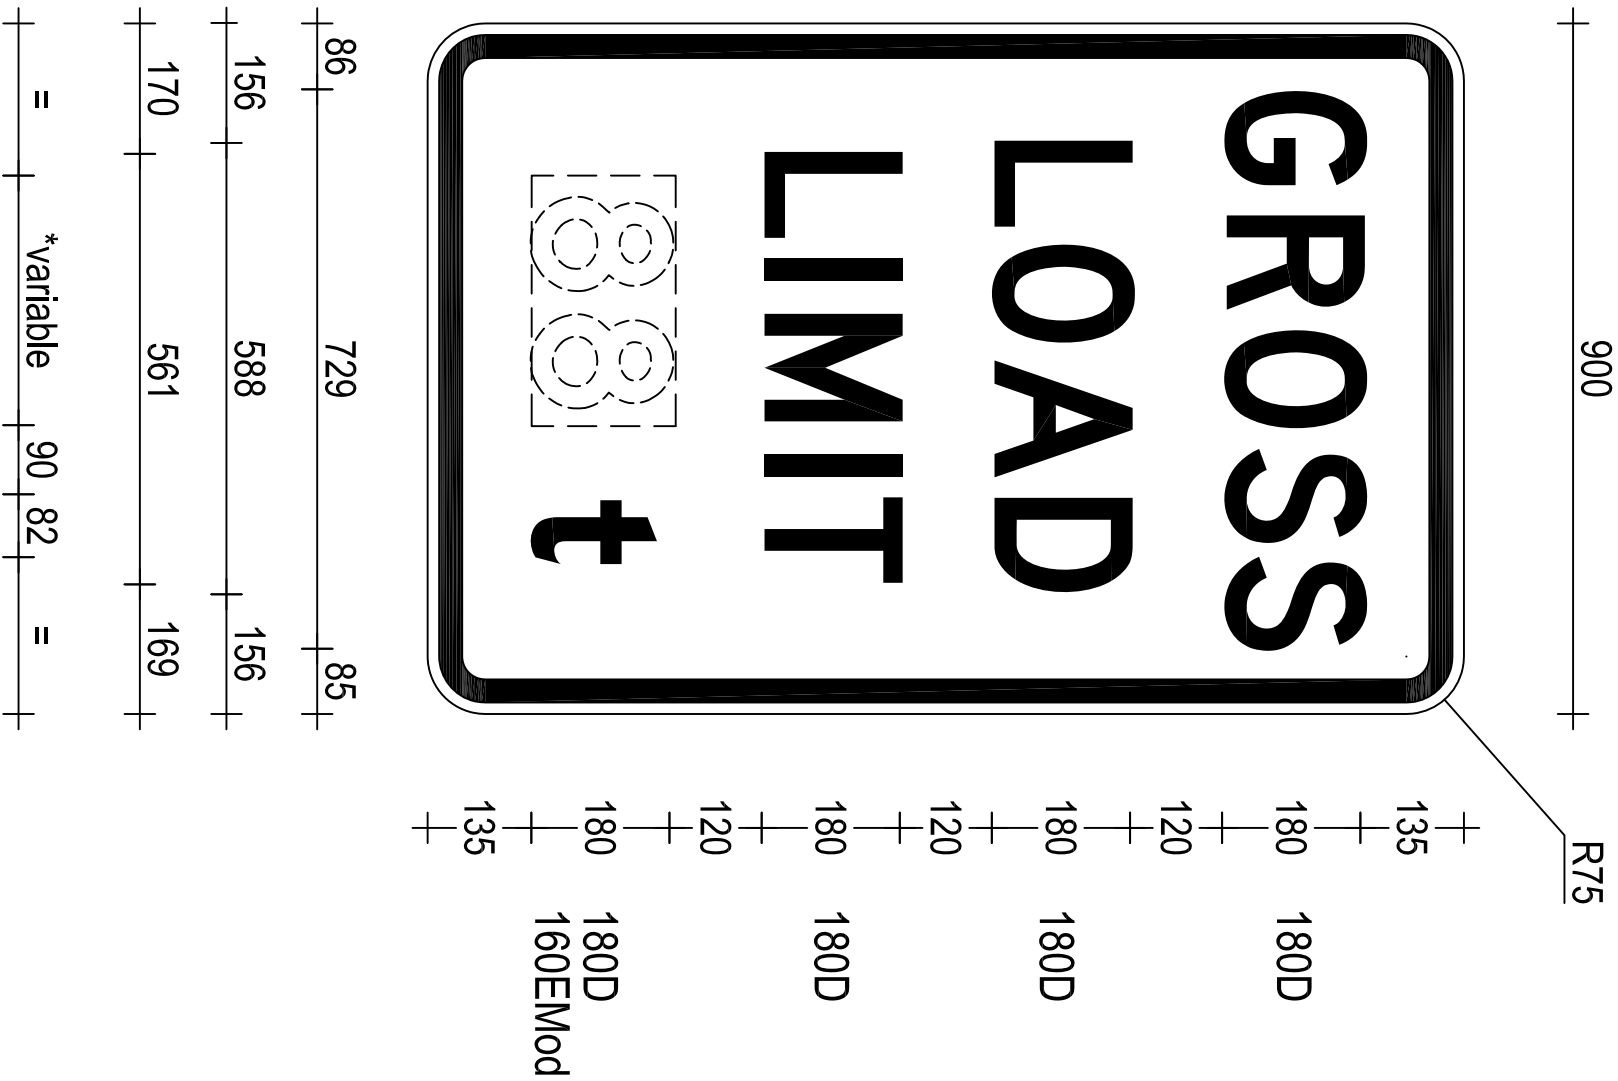


OR CODE	Scan to Check Document Version	REV	DATE	AMENDMENT / REVISION DESCRIPTION	APPROVAL	DRAWING FILE LOCATION / NAME: H:\SIGN\TTT\DRAWINGS\PLOT\REGULAT\TR6-4.DWG
		01	23-03-18	AS Forms & material classification revised	P. Oliver	
ALL DIMENSIONS ARE IN MILLIMETRES UNLESS OTHERWISE SPECIFIED						SIGN TO BE MANUFACTURED IN ACCORDANCE WITH RMS QA SPECIFICATION 3400
DESIGNED		VERIFIED		REGULATORY SIGN		
SIGNED: 		SIGNED: 		 Transport Roads & Maritime Services		
NAME: M. Davies		NAME: P. Oliver				
DATE: 31-07-19		DATE: 31-07-19				
REVIEWED		TITLE: Manager, Guidance & Delineation		PREPARED BY GUIDANCE AND DELINEATION UNIT TRAFFIC ENGINEERING SERVICES TECHNICAL AND PROJECT SERVICES		
SIGNED: 		DATE: 31-07-19				
NAME: J. Rozos		DATE: 31-07-19				
REGULATORY SIGN						A3
R6-4 GROSS LOAD LIMIT XX(t)						SHEET 1 OF 1
SCALE: 1:10						EDMS No. XXXXXXXXXX
						SHEET No. 1
						ISSUE 01

ACCEPTED FOR CONSTRUCTION

R6-4(A)
600 x 900

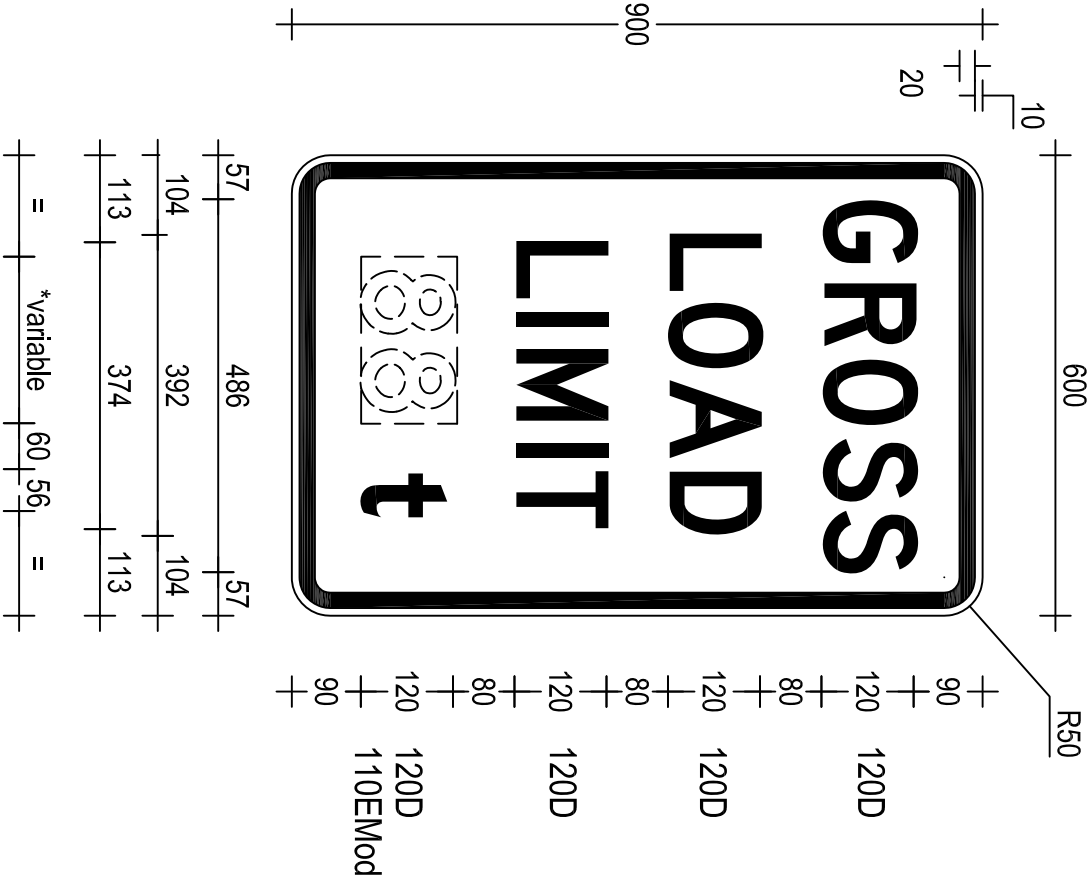

R6-4(B)
900 x 1350