


OR CODE	SCHEMATIC VERSION Document Version	REV	DATE	AMENDMENT / REVISION DESCRIPTION	APPROVAL	DRAWING FILE LOCATION / NAME: H:\SIGN\TTP\DRAWINGS\PL\OT\REG-R6-8.DWG	DESIGNED	VERIFIED	 Transport NSW GOVERNMENT Roads & Maritime Services	REGULATORY SIGN R6-8 STOP/SLOW BAT	A3		
		01	23-03-18	AS Forms & material classification revised	P. Oliver		SIGNED NAME: M. Davies DATE: 12-07-19 REVIEWED NAME: J. Rozos DATE: 12-07-19	SIGNED NAME: P. Oliver TITLE: Manager, Guidance & Delineation DATE: 12-07-19					
ALL DIMENSIONS ARE IN MILLIMETRES UNLESS OTHERWISE SPECIFIED							SIGN TO BE MANUFACTURED IN ACCORDANCE WITH RMS QA SPECIFICATION 3400	PREPARED BY GUIDANCE AND DELINEATION TRAFFIC ENGINEERING SERVICES TECHNICAL AND PROJECT SERVICES		SCALE: 1:10	EDMS N ^o . XXXXXXXXXX	SHEET N ^o . 1	ISSUE 01
								SHEET 1 OF 1		© Roads and Maritime Services			

ACCEPTED FOR CONSTRUCTION

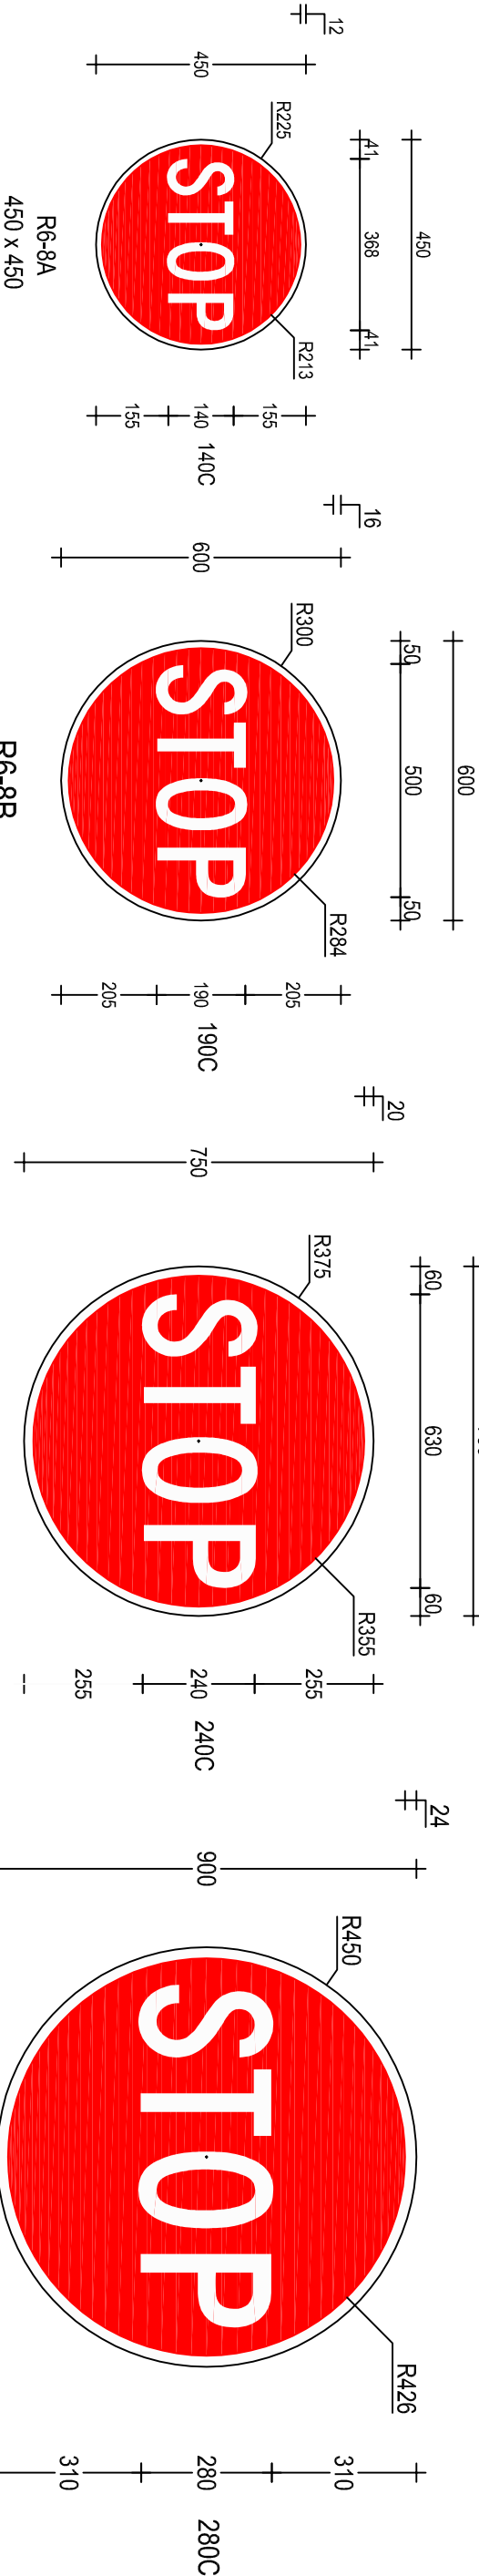

R6-8D
900 x 900