


50mm ON A3 SIZE ORIGINAL


OR CODE		Scan to Check Document Version	REV	DATE	AMENDMENT / REVISION DESCRIPTION	APPROVAL	DRAWING FILE LOCATION / NAME: H:\SIGN\TTP\DRAWINGS\PROJECT\REGULATORY\7-1-1.DWG	DESIGNED	VERIFIED	REGULATORY SIGN		A3
			01	23-03-18	AS Forms & material classification revised	P. Oliver		SIGNED NAME: M. Davies DATE: 31-07-19 REVIEWED SIGNED: J. Rozdos NAME: J. Rozdos DATE: 31-07-19	SIGNED NAME: P. Oliver DATE: 31-07-19 TITLE: Manager, Guidance & Delineation	R7-11-1 CROSS ARROW SUPPLEMENTARY PLATES (BOTH WAYS)		
ALL DIMENSIONS ARE IN MILLIMETRES UNLESS OTHERWISE SPECIFIED					SIGN TO BE MANUFACTURED IN ACCORDANCE WITH RMS QA SPECIFICATION 3400			SHEET 1 OF 1				
								SCALE: 1:10				
								EDMS No. XXXXXXXXXX				
								SHEET No. 1				
								ISSUE 01				
								SHEET 1 OF 1				
								A3				

© Roads and Maritime Services


ACCEPTED FOR CONSTRUCTION

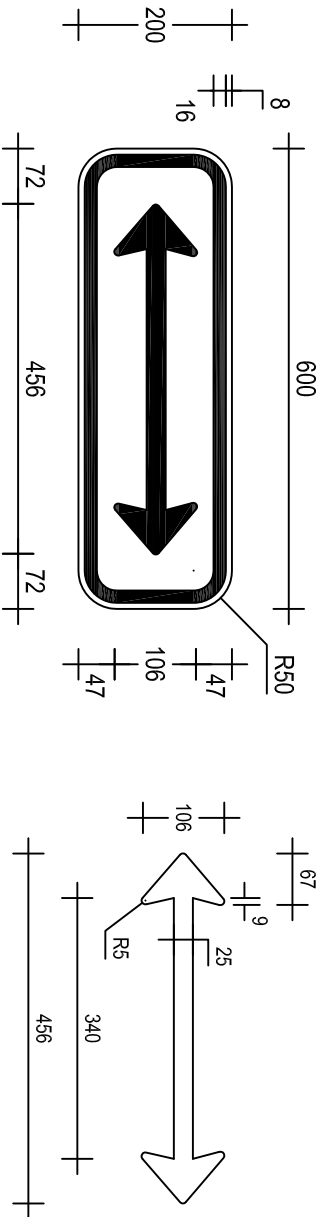

R7-11-1(C)
600 x 200

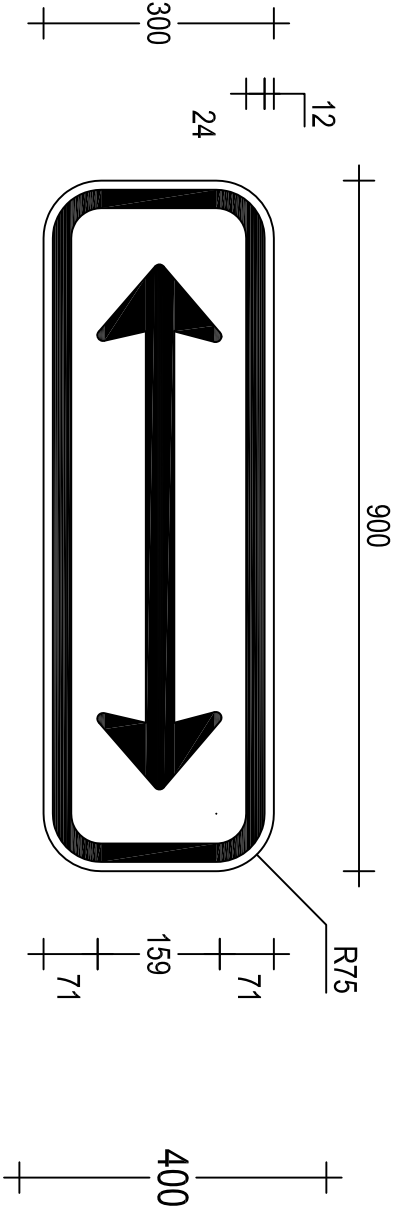

R7-11-1(D)
900 x 300

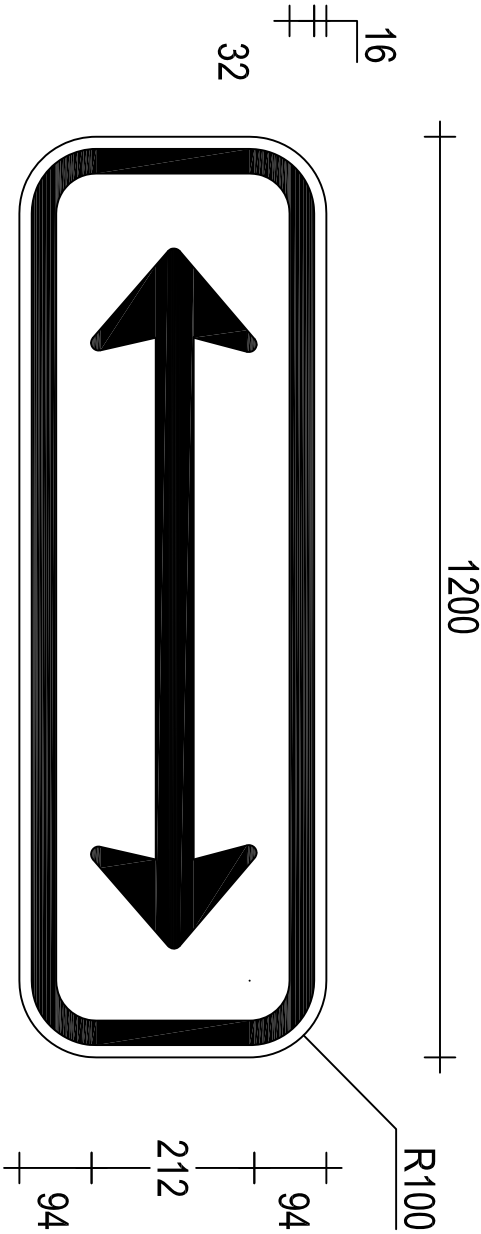

R7-11-1(E)
1200 x 400

