



051015253035404550mm ON A3 SIZE ORIGINAL

OR CODE	Scan to Check Document Version	REV	DATE	AMENDMENT / REVISION DESCRIPTION	APPROVAL	DRAWING FILE LOCATION / NAME: H:\SIGN\ITTDRAWINGS\PLOT\REGULATR2-12.DWG	DESIGNED	VERIFIED	PREPARED BY	REGULATORY SIGN	A3
		01	23-03-18	AS Forms & material classification revised	P.Oliver		SIGNED: M. Davies NAME: M. Davies DATE: 31-07-19	SIGNED: P.Oliver NAME: P.Oliver TITLE: Manager, Guidance & Delineation DATE: 31-07-19	NSW GOVERNMENT Transport Roads & Maritime Services	R7-12	
						MATERIALS: ALUMINIUM SIGN BLACK LEGEND AND BORDER ON AS1906.1 CL.400 WHITE REFLECTORISED GROUND	REVIEWED SIGNED: J. Rozdos NAME: J. Rozdos DATE: 31-07-19		GUIDANCE AND DELINEATION UNIT TRAFFIC ENGINEERING SERVICES TECHNICAL AND PROJECT SERVICES	R7-12 x (m) AHEAD	SHEET 1 OF 1 EDMS No. XXXXXXXXXX SHEET No. 1 ISSUE 01
ALL DIMENSIONS ARE IN MILLIMETRES UNLESS OTHERWISE SPECIFIED						SIGN TO BE MANUFACTURED IN ACCORDANCE WITH RMS QA SPECIFICATION 3400				SCALE: 1:10	


ACCEPTED FOR CONSTRUCTION

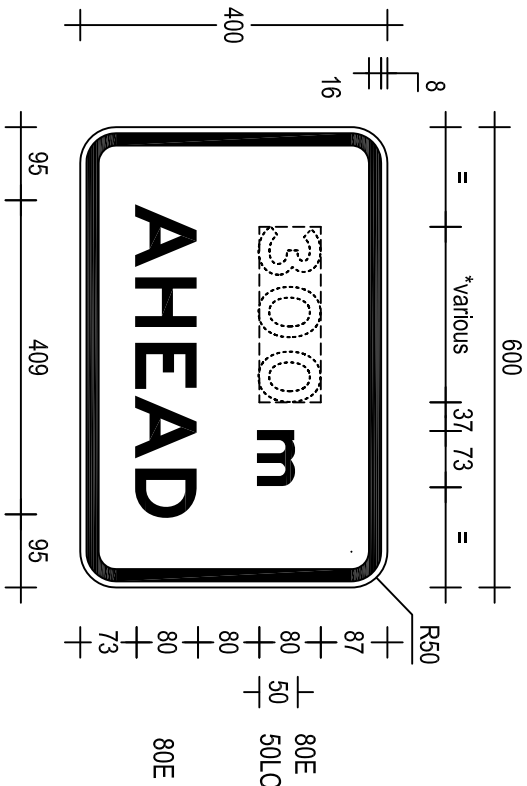

R7-12(C)
600 x 400

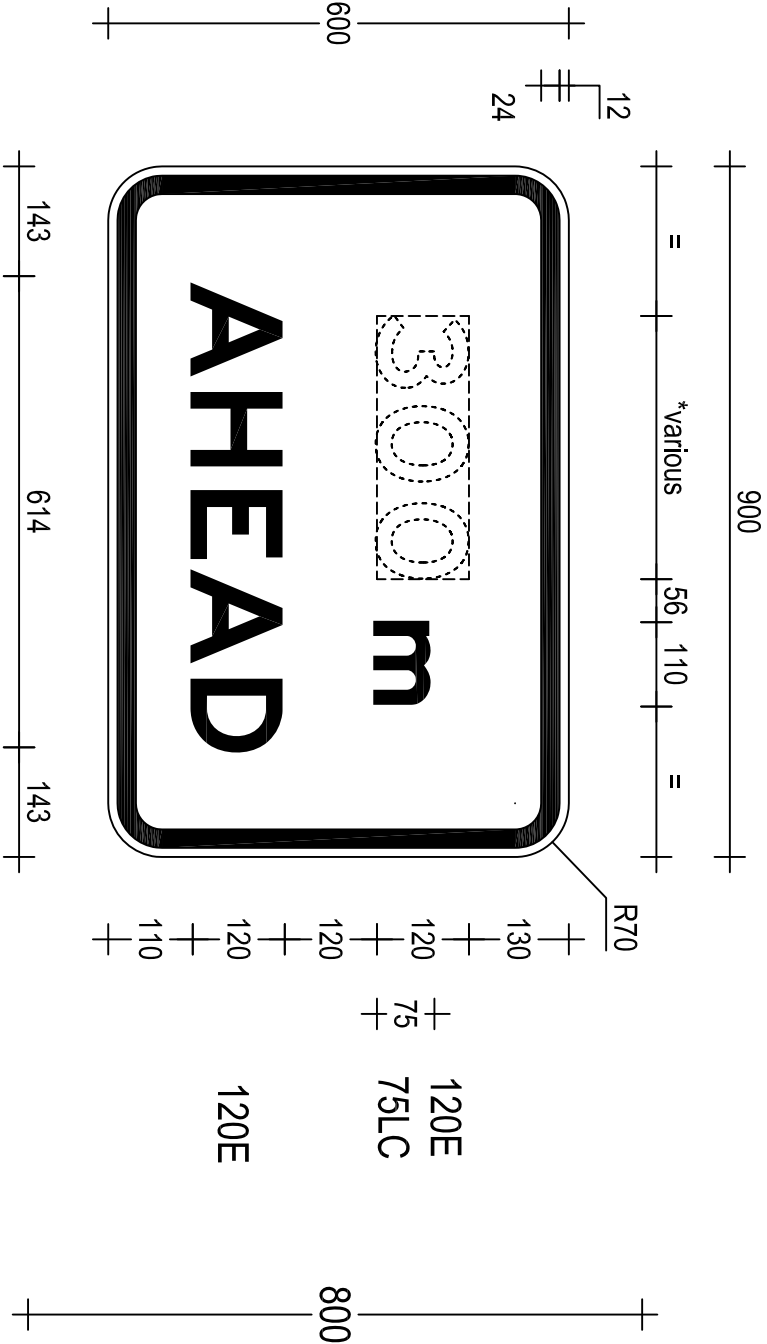

R7-12(D)
900 x 600

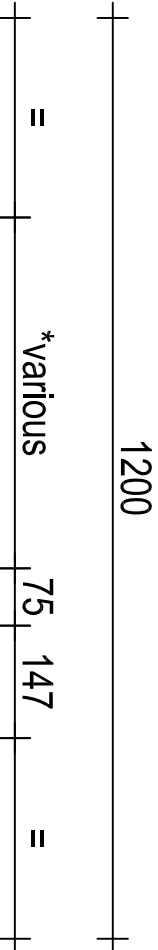

R7-12(E)
1200 x 800

