


1600

R25

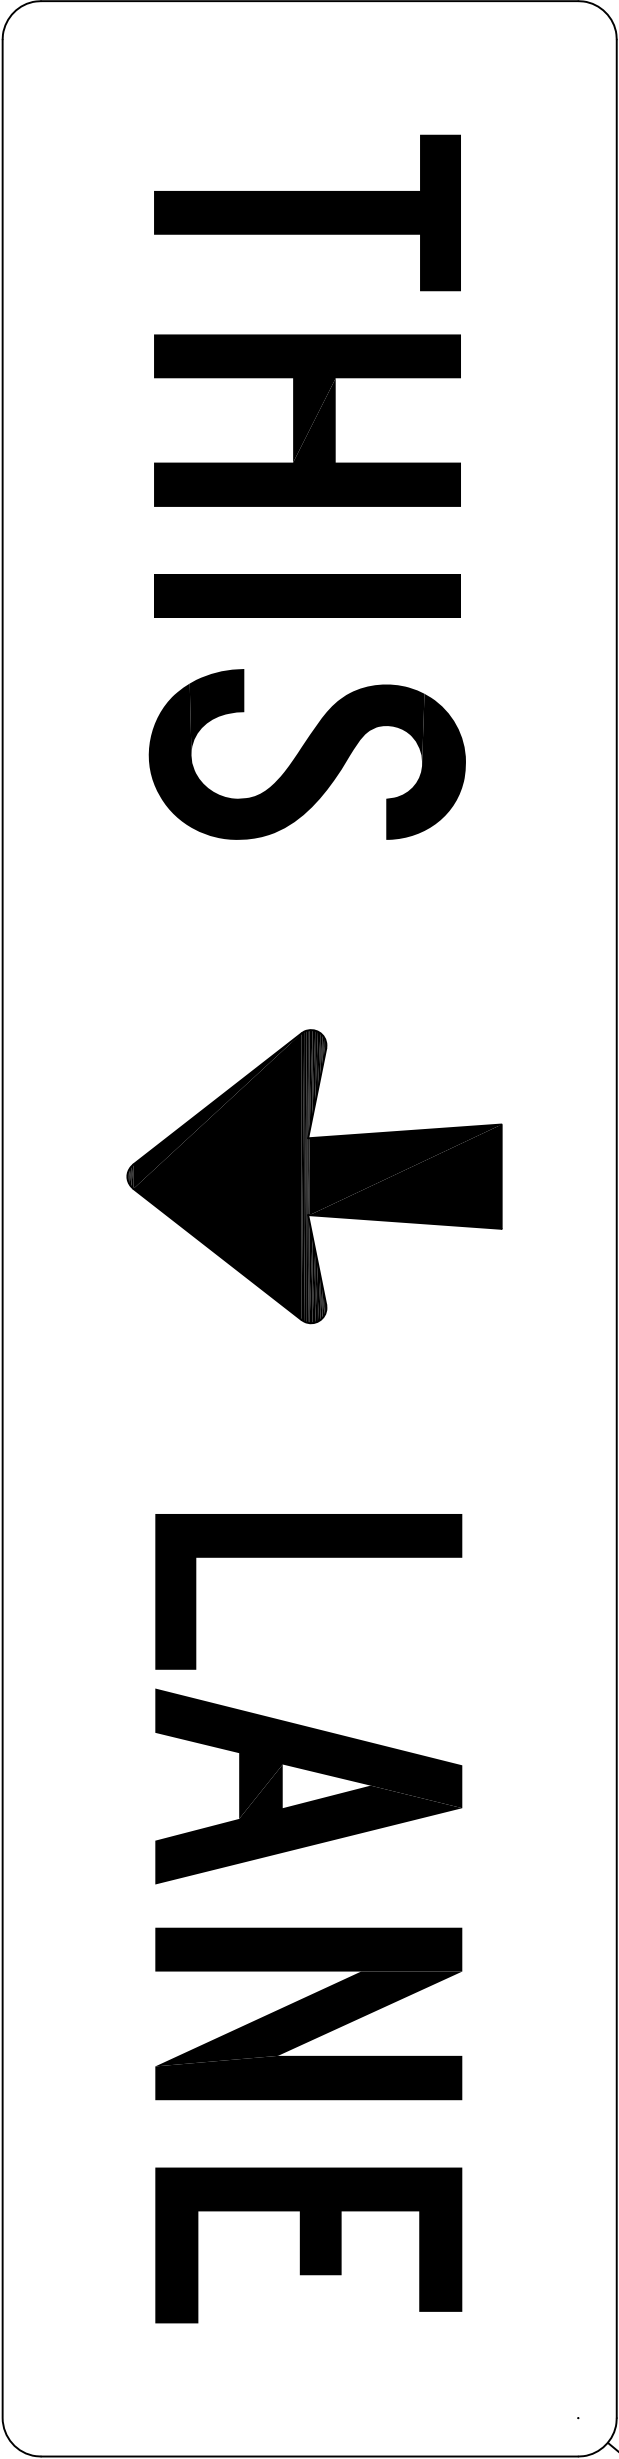


20

220

68


R7-6-4

1600 x 400

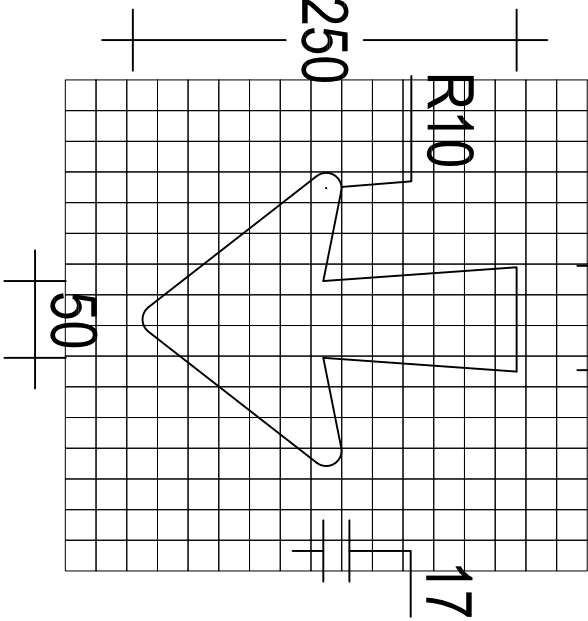

ACCEPTED FOR CONSTRUCTION

THIS DRAWING MAY BE PREPARED IN COLOUR AND MAY BE INCOMPLETE IF COPIED

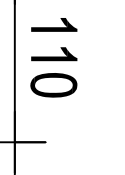0	5	10	15	20	25	30	35	40	45	50mm ON A3 SIZE ORIGINAL
OR CODE	Scan to Check Document Version	REV	DATE	AMENDMENT / REVISION DESCRIPTION	APPROVAL	DRAWING FILE LOCATION / NAME: H:\SIGN\TTT\DRAWINGS\PLOT\REGULAT\R7-6-4.DWG				
		01	23-03-18	AS Forms & material classification revised	P. Oliver	MATERIALS: ALUMINIUM SIGN BLACK LEGEND & SYMBOL ON AS1906.1 CL.400 WHITE REFLECTORISED GROUND				
ALL DIMENSIONS ARE IN MILLIMETRES UNLESS OTHERWISE SPECIFIED						SIGN TO BE MANUFACTURED IN ACCORDANCE WITH RMS QA SPECIFICATION 3400				
DESIGNED						VERIFIED				
SIGNED: 						SIGNED: 				
NAME: M. Davies						NAME: P. Oliver				
DATE: 31-07-19						DATE: 31-07-19				
REVIEWED						TITLE: Manager Guidance & Delineation				
SIGNED: 						DATE: 31-07-19				
NAME: J. Rozos										
						PREPARED BY				
						GUIDANCE AND DELINEATION UNIT				
						TRAFFIC ENGINEERING SERVICES				
						TECHNICAL AND PROJECT SERVICES				
						REGULATORY SIGN				
						R7-6-4				
						THIS LANE				
						SCALE: 1:5				
						SHEET 1 OF 1				
						EDMS No. XXXXXXXXXX				
						SHEET No. 1				
						ISSUE 01				