

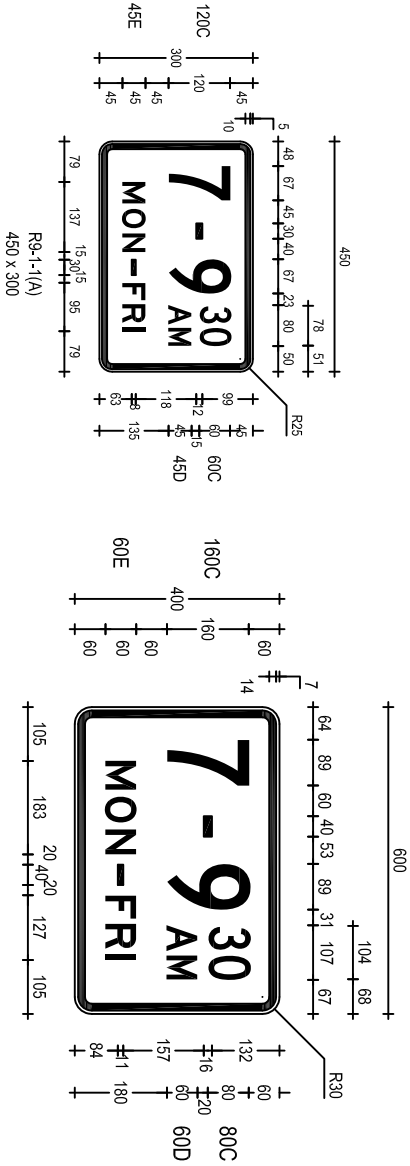


|    |                                                              |                                   |     |                                            |                                  |   |                                                                        |                                                                             |          |   |   |    |
|----|--------------------------------------------------------------|-----------------------------------|-----|--------------------------------------------|----------------------------------|---|------------------------------------------------------------------------|-----------------------------------------------------------------------------|----------|---|---|----|
| 25 | OR CODE                                                      | Scan to Check<br>Document Version | REV | DATE                                       | AMENDMENT / REVISION DESCRIPTION | APPROVAL                                                                                              | DRAWING FILE LOCATION / NAME: H:\SIGN\IT\DRAWINGS\PLOT\REGULATR2\0.DWG | DESIGNED                                                                    | VERIFIED | <div><div>Transport<br/>Roads &amp; Maritime<br/>Services</div></div> <div>PREPARED BY<br/>GUIDANCE AND DELINEATION UNIT<br/>TRAFFIC ENGINEERING SERVICES<br/>TECHNICAL AND PROJECT SERVICES</div> | <div>REGULATORY SIGN</div> <div>R9-1-1</div> <div>TIMES OF OPERATION (Single Period)</div> <div>(AM Illustrated)</div> <div>SHEET 1 OF 1</div> | A3 |
| 20 |                                                              |                                   |     | AS Forms & material classification revised | P. Oliver                        | MATERIALS: ALUMINIUM SIGN<br>BLACK LEGEND AND BORDER<br>ON AS1906.1 CL.400 WHITE REFLECTORISED GROUND | NAME: M. Davies<br>DATE: 24-03-21                                      | NAME: P. Oliver<br>TITLE: Manager, Guidance & Delineation<br>DATE: 24-03-21 |          |   |   |    |
| 15 |                                                              |                                   |     |                                            |                                  |   | REVIEWED                                                               |                                                                             |          |   |   |    |
| 10 |                                                              |                                   |     |                                            |                                  |   | NAME: J. Rozos<br>DATE: 24-03-21                                       |                                                                             |          |   |   |    |
| 5  |                                                              |                                   |     |                                            |                                  |   |                                                                        |                                                                             |          |   |   |    |
|    | ALL DIMENSIONS ARE IN MILLIMETRES UNLESS OTHERWISE SPECIFIED |                                   |     |                                            |                                  |   | SIGN TO BE MANUFACTURED IN ACCORDANCE WITH RMS QA SPECIFICATION 3400   |                                                                             |          |   |   |    |

ACCEPTED FOR CONSTRUCTION

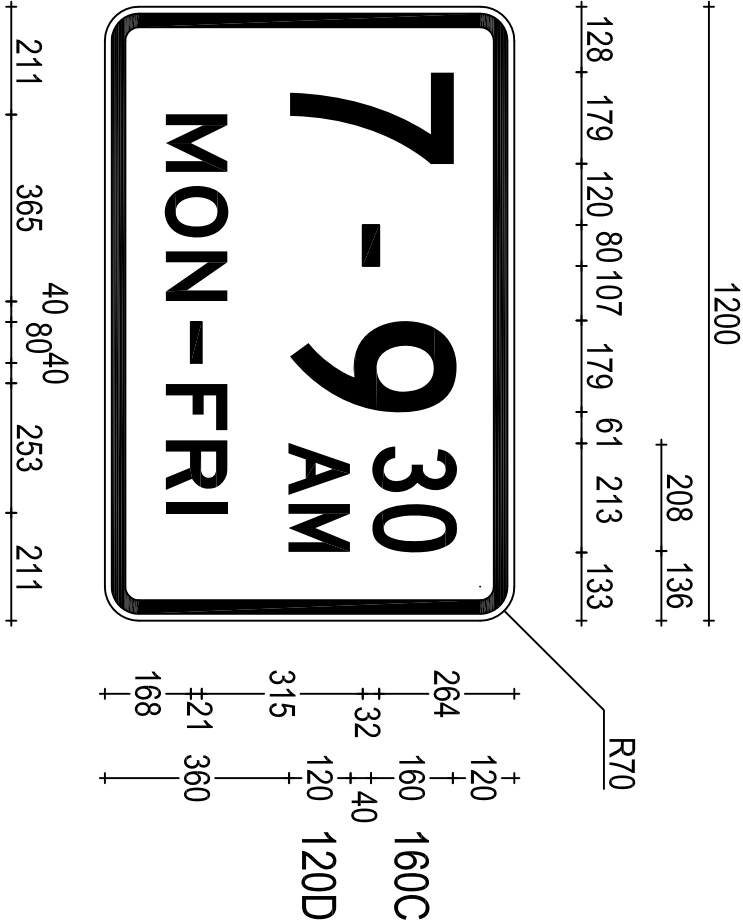

R9-1-1(B)  
600 x 400

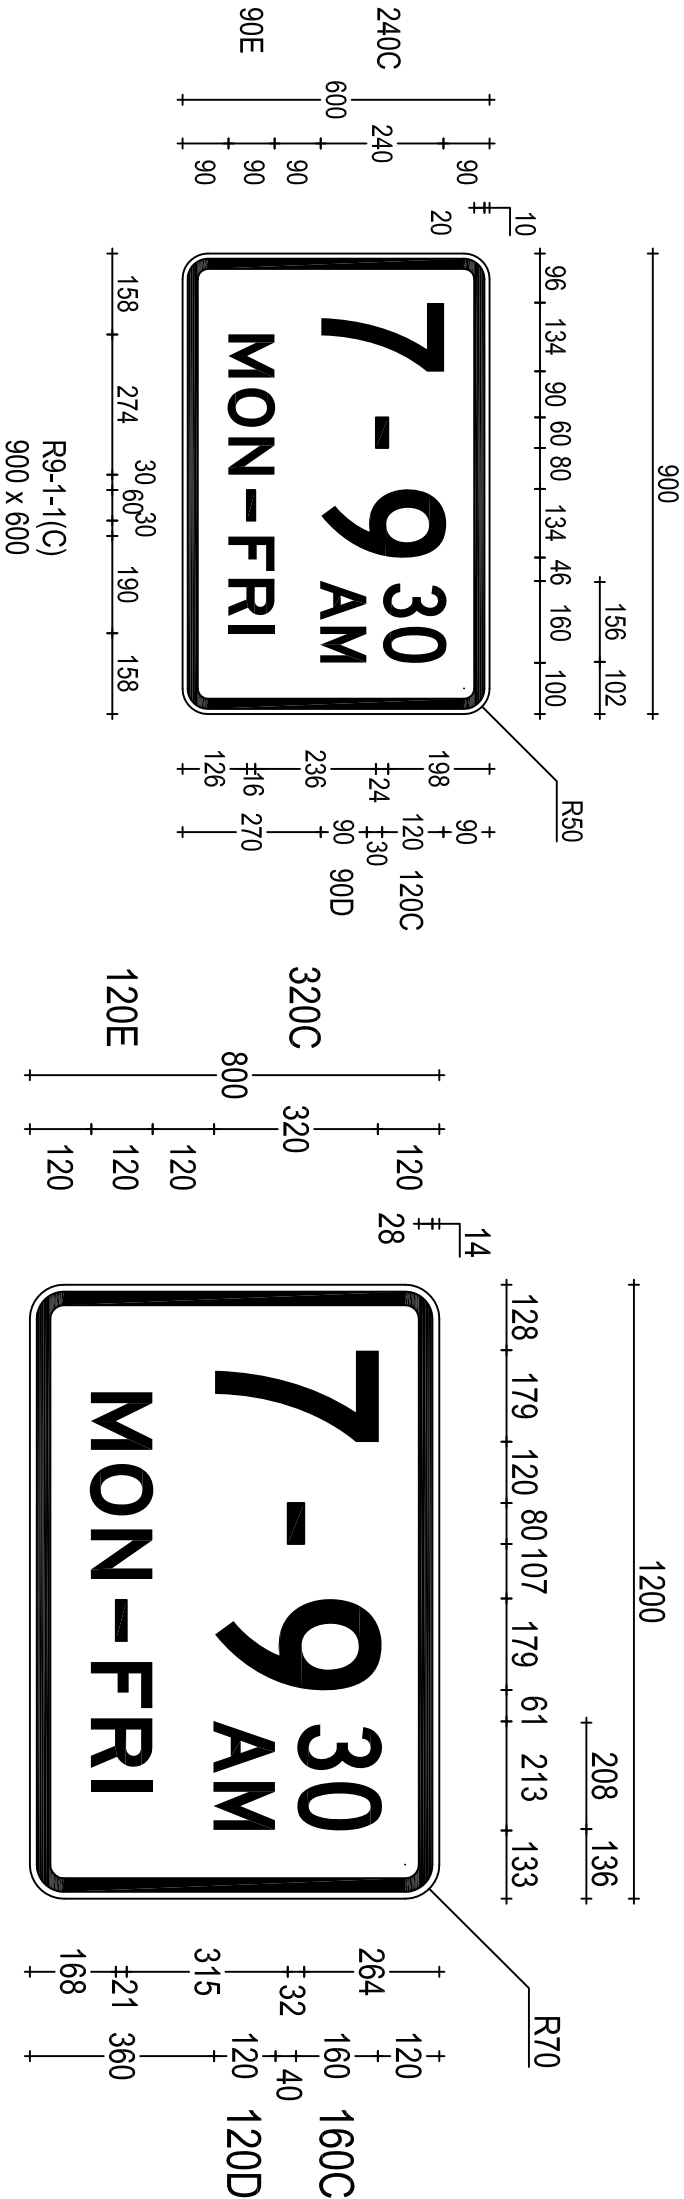

R9-1-1(D)  
1200 x 800