


06 CODE	Scan to Check Document Version	REV	DATE	AMENDMENT / REVISION DESCRIPTION	APPROVAL	DRAWING FILE LOCATION / NAME : H:\SIGN\1TDRRAWINGS\PLT\REGULATR9-203-3D.WG	DESIGNED	VERIFIED	 Transport Roads & Maritime Services GOVERNMENT			REGULATORY SIGN R9-203-3n GARAGE AND LOADING DOCK ACCESS EXCEPTED			SHEET 1 OF 1		A3	
25		01	23-03-18	AS Forms & material classification revised	P Oliver		NAME : M Davies DATE : 24-03-21	NAME : P Oliver TITLE : Manager, Guidance & Delineation DATE : 24-03-21	PREPARED BY GUIDANCE AND DELINEATION UNIT TRAFFIC ENGINEERING SERVICES TECHNICAL AND PROJECT SERVICES			EDMS No. XXXXXXXXXX		SHEET No. 1	ISSUE 01			
20	MATERIALS: ALUMINIUM SIGN BLACK LEGEND AND BORDER ON AS1906.1 CL.400 WHITE REFLECTORISED GROUND						REVIEWED NAME : J Rozos DATE : 24-03-21											
15																		
10																		
5	ALL DIMENSIONS ARE IN MILLIMETRES UNLESS OTHERWISE SPECIFIED						SIGN TO BE MANUFACTURED IN ACCORDANCE WITH RMS QA SPECIFICATION 3400											

ACCEPTED FOR CONSTRUCTION

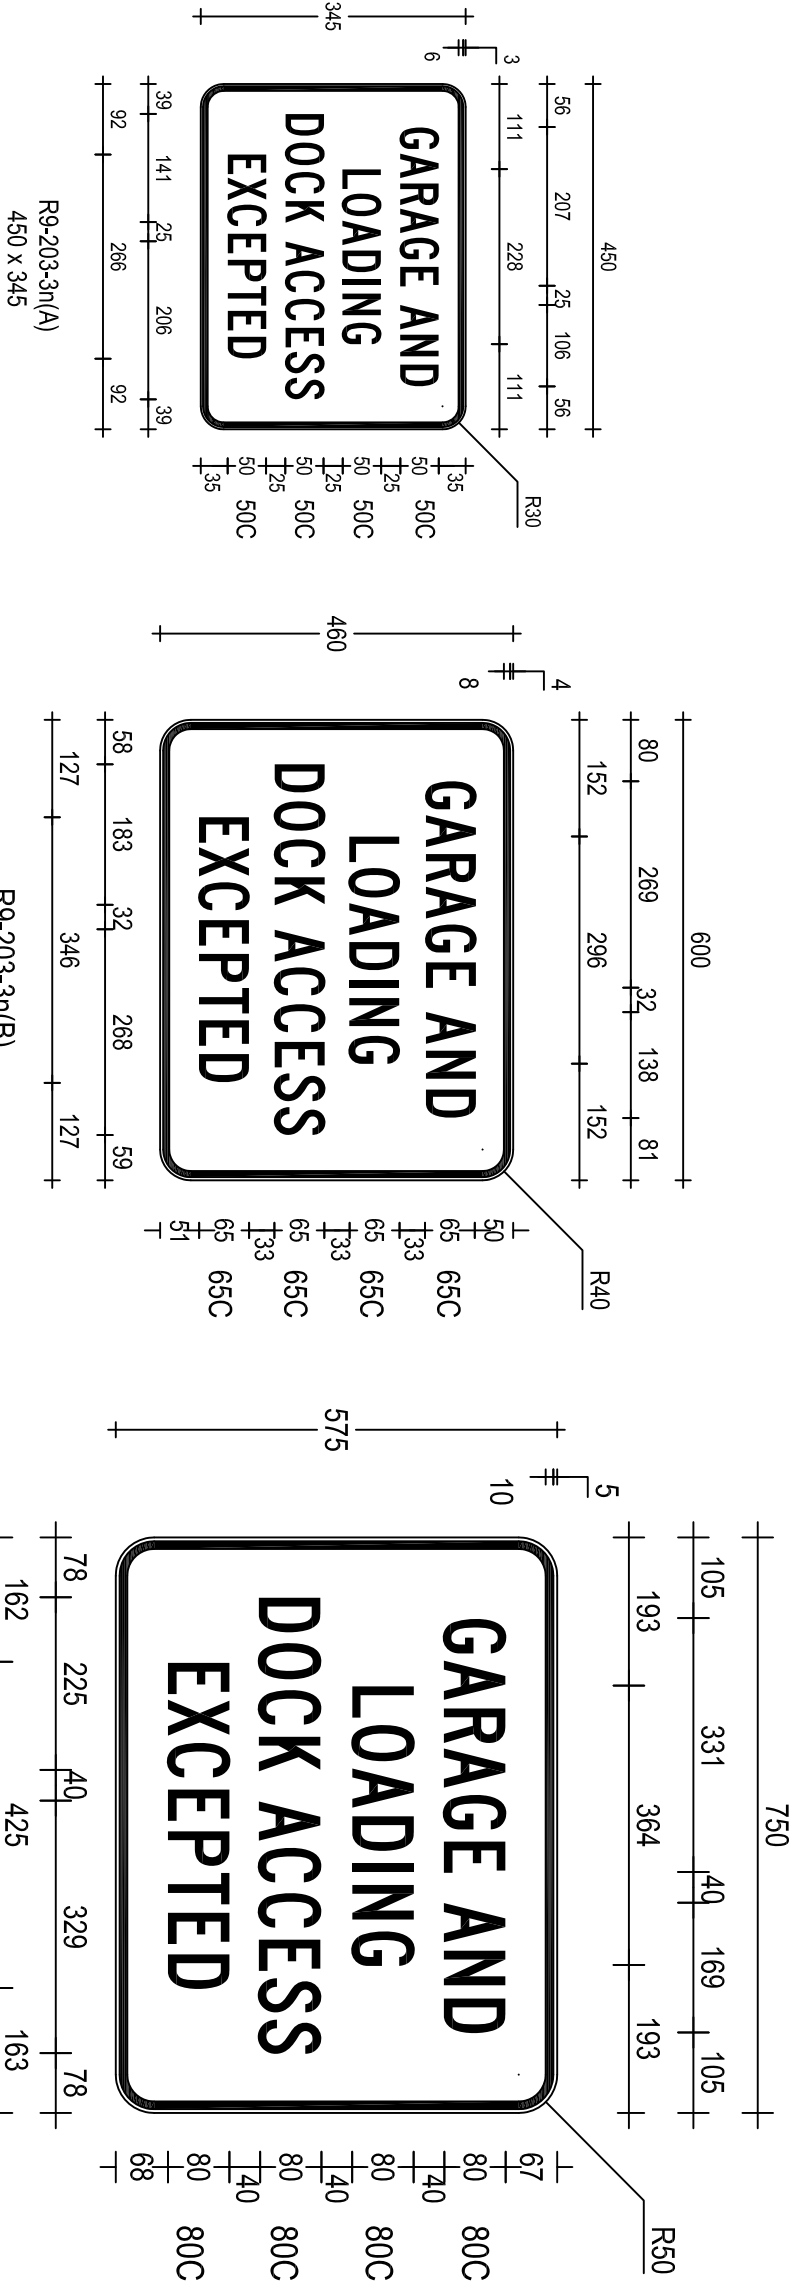

R9-203-3n(C)
750 x 575