
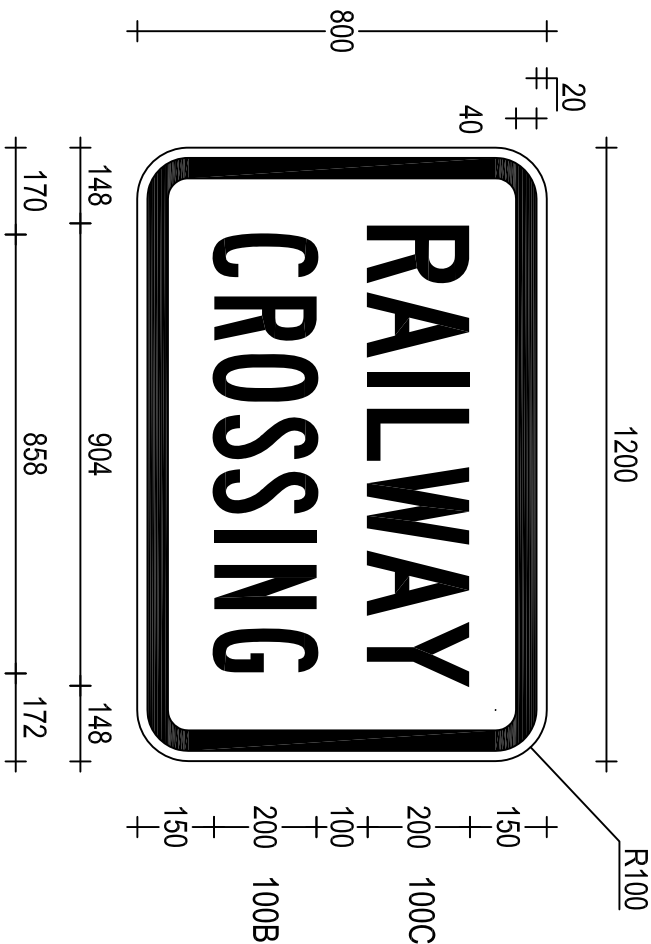
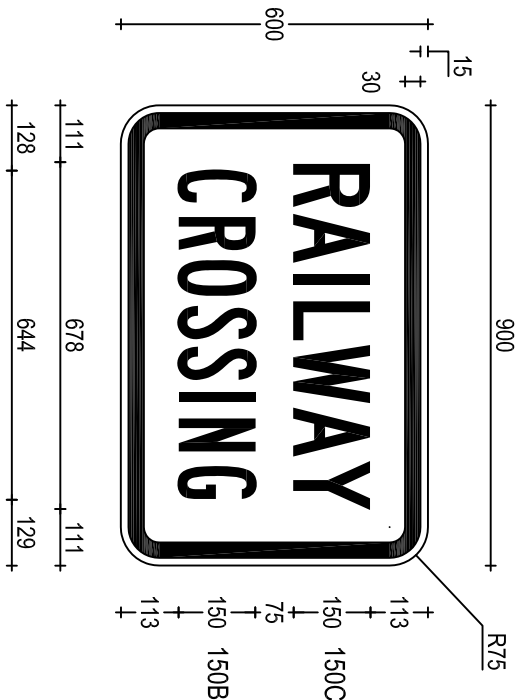
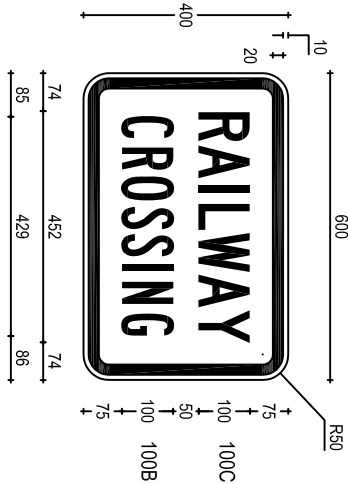


25	OR CODE Document Version	REV 01	DATE 23-06-18	AMENDMENT / REVISION DESCRIPTION AS Forms & material classification revised	APPROVAL P. Oliver	DRAWING FILE LOCATION / NAME : H:\SIGN\17\TRAFFIC\NSP\LOT\REGUL\RA9-236n.DWG	DESIGNED SIGNED  NAME M. Davies DATE 31-07-19 REVIEWED  SIGNED J. Rozz NAME J. Rozz DATE 31-07-19	VERIFIED  SIGNED P. Oliver NAME P. Oliver TITLE Manager, Guidance & Delineation DATE 31-07-19	 Transport Roads & Maritime Services GOVERNMENT	PREPARED BY GUIDANCE AND DELINEATION UNIT TRAFFIC ENGINEERING SERVICES TECHNICAL AND PROJECT SERVICES	REGULATORY SIGN R9-236n RAILWAY CROSSING	SHEET 1 OF 1	EDMS No. XXXXXXXXXX	SHEET No. 1	ISSUE 01	A3	
20													SCALE: 1:15				
15																	
10																	
5																	
0	ALL DIMENSIONS ARE IN MILLIMETRES UNLESS OTHERWISE SPECIFIED						SIGN TO BE MANUFACTURED IN ACCORDANCE WITH RMS QA SPECIFICATION 3400										

ACCEPTED FOR CONSTRUCTION

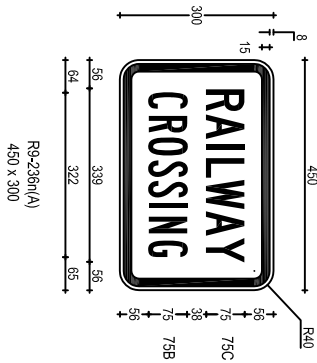

R9-236n(C)
900 x 600

R9-236n(D)
1200 x 800