


05101520253035404550mm ON A3 SIZE ORIGINAL


OR CODE	Scan to Check Document Version	REV	DATE	AMENDMENT / REVISION DESCRIPTION	APPROVAL	DRAWING FILE LOCATION / NAME: H:\SIGN\TTT\DRAWINGS\PLOT\REGULAT\R9-6-1.DWG	DESIGNED	VERIFIED	 Transport Roads & Maritime Services PREPARED BY GUIDANCE AND DELINEATION UNIT TRAFFIC ENGINEERING SERVICES TECHNICAL AND PROJECT SERVICES				REGULATORY SIGN R9-6-1 NEXT (x)m			A3
		01	22-03-18	AS Forms & material classification revised	P. Oliver	MATERIALS: ALUMINIUM SIGN BLACK LEGEND AND BORDER ON AS1906.1 CL.400 WHITE REFLECTORISED GROUND	NAME: M. Davies DATE: 24-03-21 REVIEWED NAME: J. Rozdos DATE: 24-03-21	NAME: P. Oliver TITLE: Manager, Guidance & Delineation DATE: 24-03-21	SHEET 1 OF 1							
ALL DIMENSIONS ARE IN MILLIMETRES UNLESS OTHERWISE SPECIFIED						SIGN TO BE MANUFACTURED IN ACCORDANCE WITH RMS QA SPECIFICATION 3400	SCALE: 1:10				EDMS No. XXXXXXXXXX	SHEET No. 1	ISSUE 01	© Roads and Maritime Services		

ACCEPTED FOR CONSTRUCTION

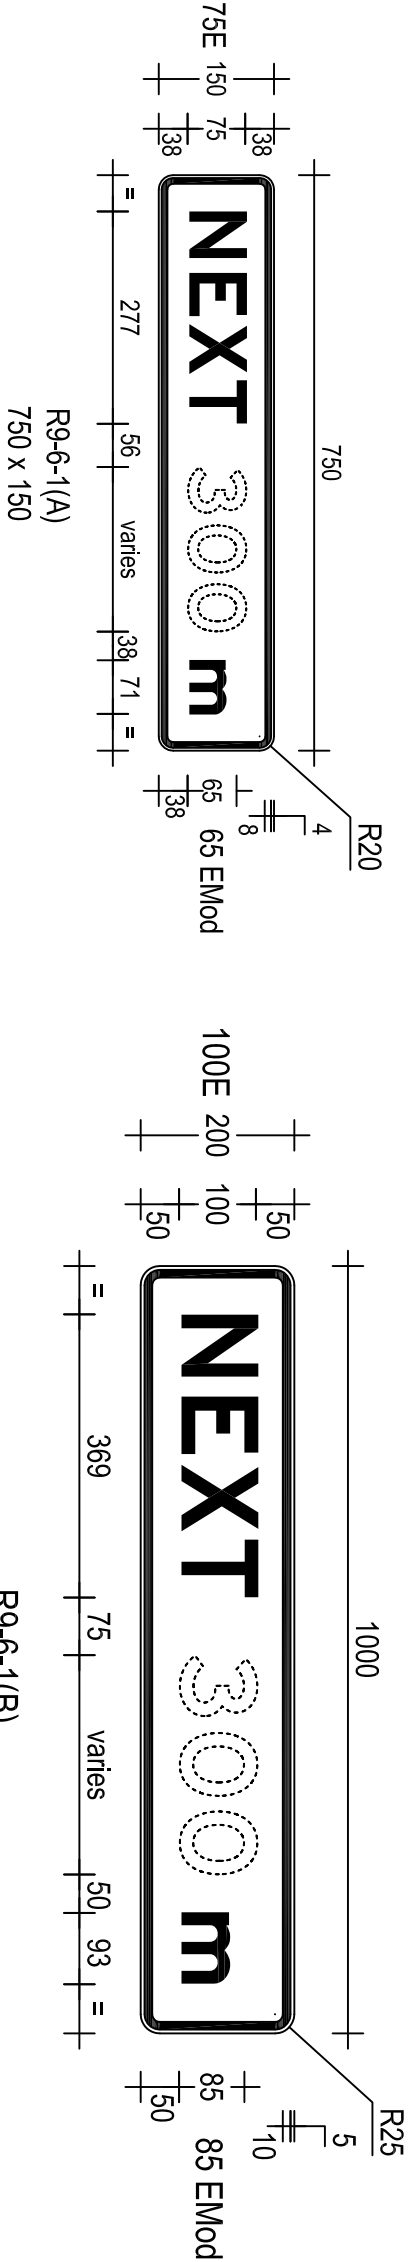

R9-6-1(A)
750 x 150

R9-6-1(B)
1000 x 200

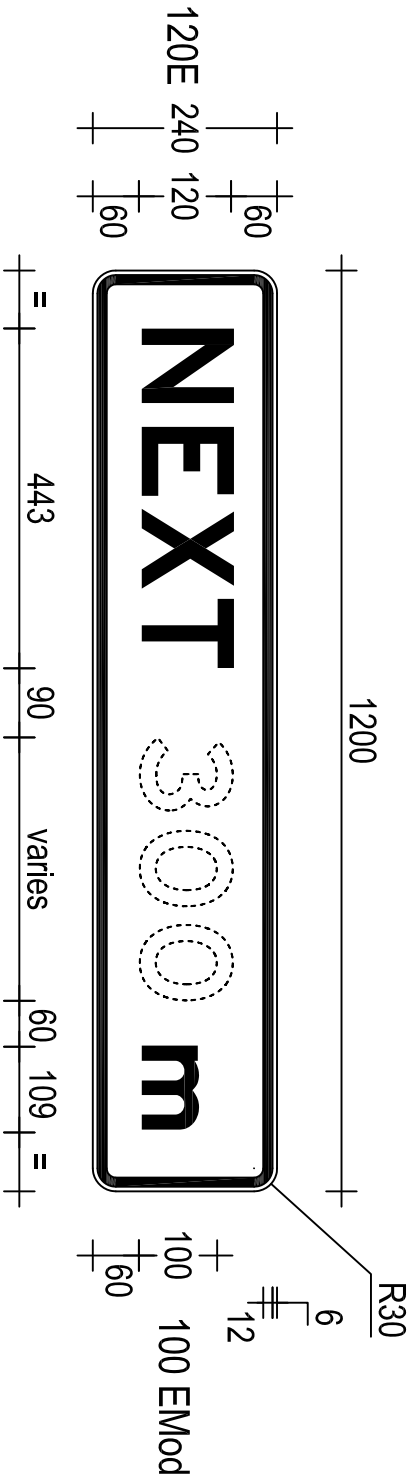

R9-6-1(C)
1200 x 240