





THIS DRAWING MAY BE PREPARED IN COLOUR AND MAY BE INCOMPLETE IF COPIED
0 15 30 1000
50mm ON A3 SIZE ORIGINAL

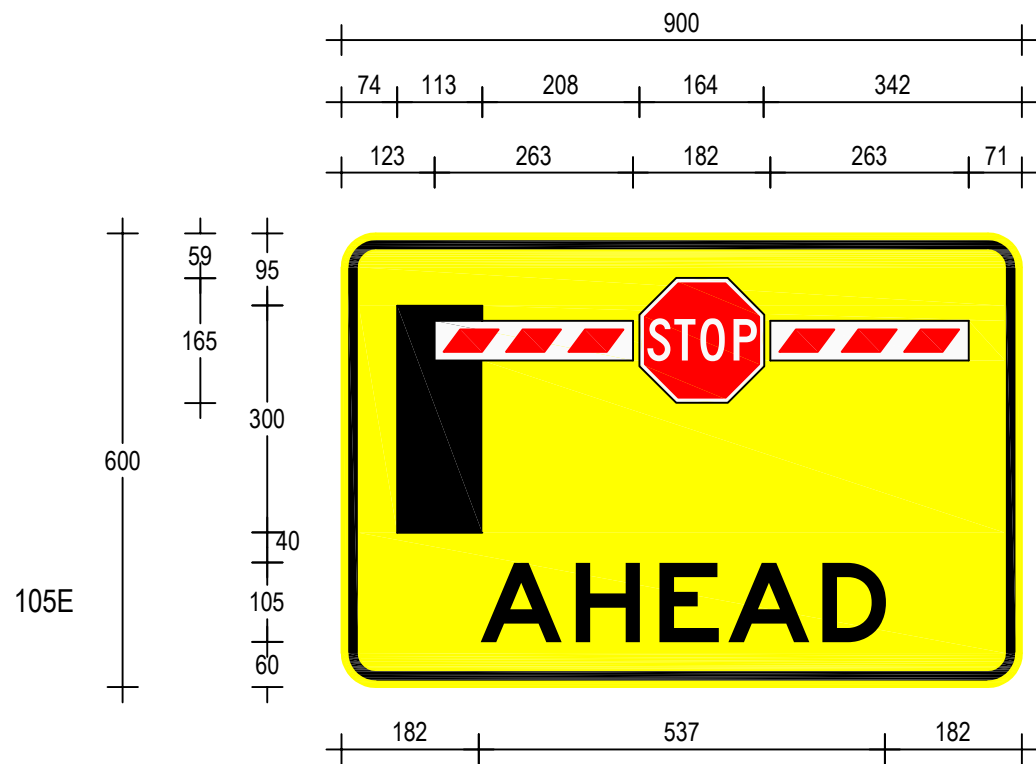

T1-272N(A)
900 X 600

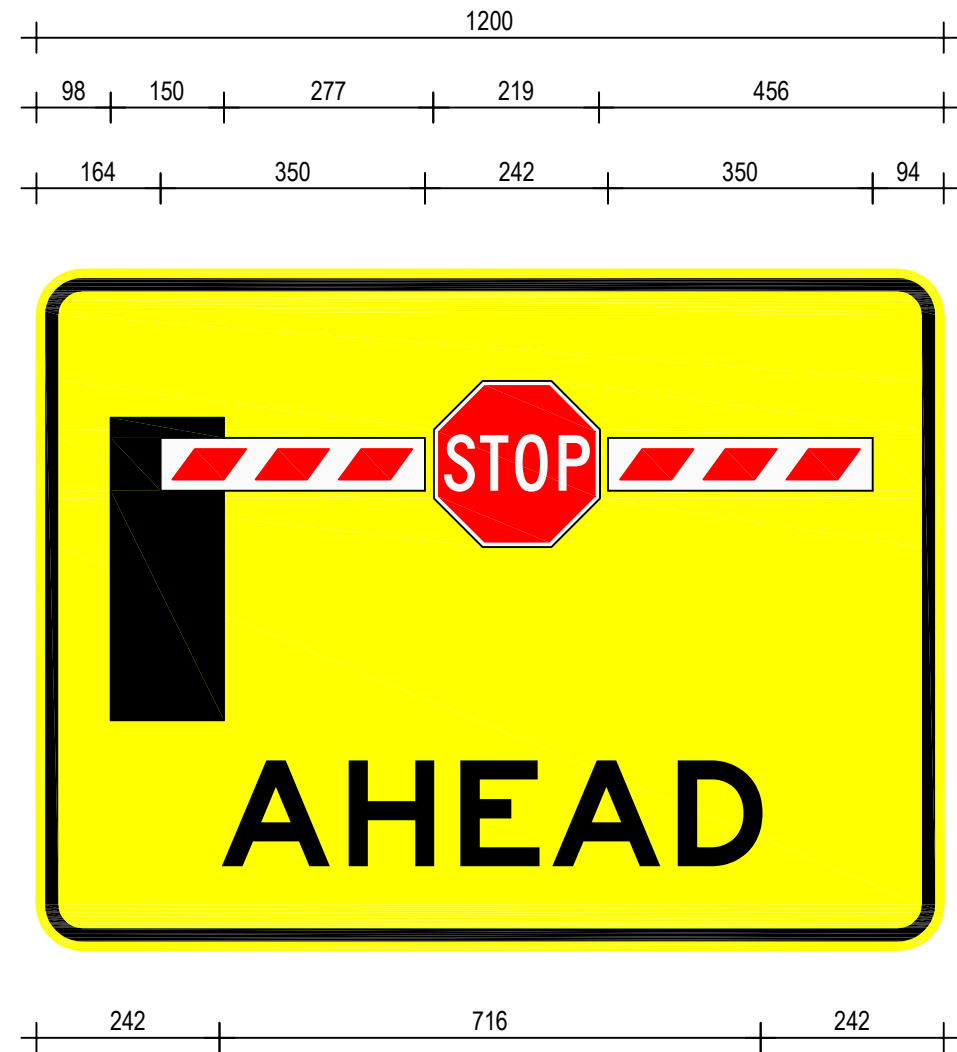

T1-272N(B)
1200 x 900

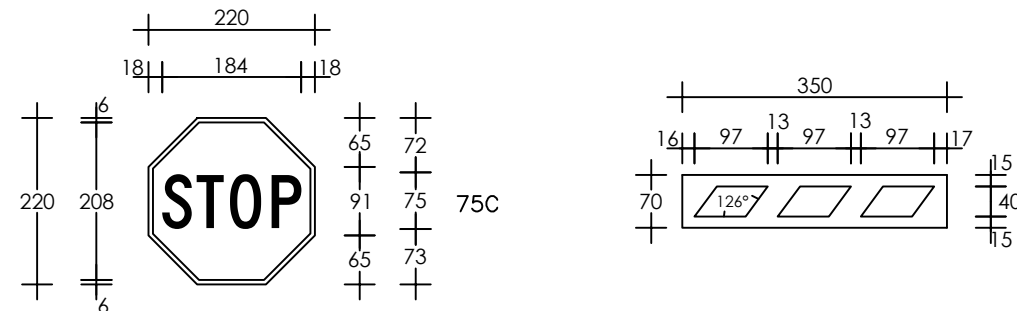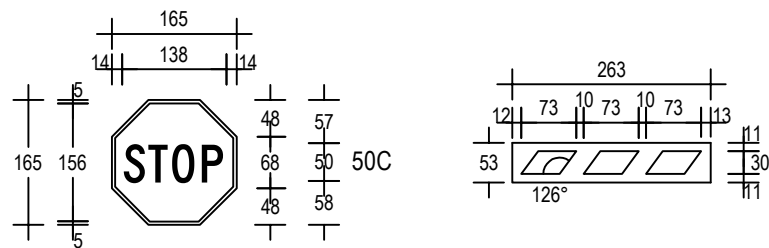

ACCEPTED FOR CONSTRUCTION

REV	DATE	AMENDMENT / REVISION DESCRIPTION	APPROVAL	DRAWING FILE LOCATION / NAME: H:\Signs\T1\Drawings\Plot\Temporary\T1-35N.dgn	DESIGNED	VERIFIED	Transport Roads & Maritime Services			TEMPORARY SIGN T1-272N BOOM BARRIER AHEAD SIGN			A3			
01				MATERIALS: Aluminium Sign Black letters and border on AS1906.1 Cl.400 Yellow refl grd Stop Sign:- AS1906.1 Cl.400 White refl lgd on AS1906.1 Cl.400 Red refl grd Boom Gate:- AS1906.1 Cl.400 Red refl chevron on AS1906.1 Cl.400 White refl grd with a black border	SIGNED NAME Martin Davies DATE 27-08-18	SIGNED NAME Phil Oliver TITLE Guidance & Delineation Manager DATE 27-08-18	 PREPARED BY GUIDANCE AND DELINEATION UNIT TRAFFIC ENGINEERING SERVICES TECHNICAL AND PROJECT SERVICES	SHEET 1 OF 1			SCALE: 1:10		EDMS No.	SHEET No.	1	ISSUE 01
ALL DIMENSIONS ARE IN MILLIMETRES UNLESS OTHERWISE SPECIFIED				SIGN TO BE MANUFACTURED IN ACCORDANCE WITH RMS QA SPECIFICATION 3400	SIGNED NAME John Rozos DATE 27-08-18											