


OR CODE		Scan to Check Document Version		REV	DATE	AMENDMENT / REVISION DESCRIPTION	APPROVAL	DRAWING FILE LOCATION / NAME: H:\SIGN\TTP\DRAWINGS\PL\OTTEMP\T1-4.DWG		DESIGNED		VERIFIED		PREPARED BY		TEMPORARY SIGN		A3	
				01	23-03-18	AS Forms & material classification revised	P. Oliver	MATERIALS: ALUMINIUM SIGN BLACK LEGEND AND BORDER ON AS1906.1 CL 400 YELLOW REFLECTORISED GROUND		SIGNED NAME M. Davies DATE 12-07-19		SIGNED NAME P. Oliver TITLE Manager, Guidance & Delineation DATE 12-07-19		NSW GOVERNMENT Transport Roads & Maritime Services		T1-4 GRADER AHEAD			
										REVIEWED SIGNED J. Rozos DATE 12-07-19				GUIDANCE AND DELINEATION TRAFFIC ENGINEERING SERVICES TECHNICAL AND PROJECT SERVICES		SCALE: 1:5		EDMS No. XXXXXXXXX	
																SHEET No. 1		ISSUE 01	
				ALL DIMENSIONS ARE IN MILLIMETRES UNLESS OTHERWISE SPECIFIED				SIGN TO BE MANUFACTURED IN ACCORDANCE WITH RMS QA SPECIFICATION 3400										© Roads and Maritime Services	

T1-4
900 x 600

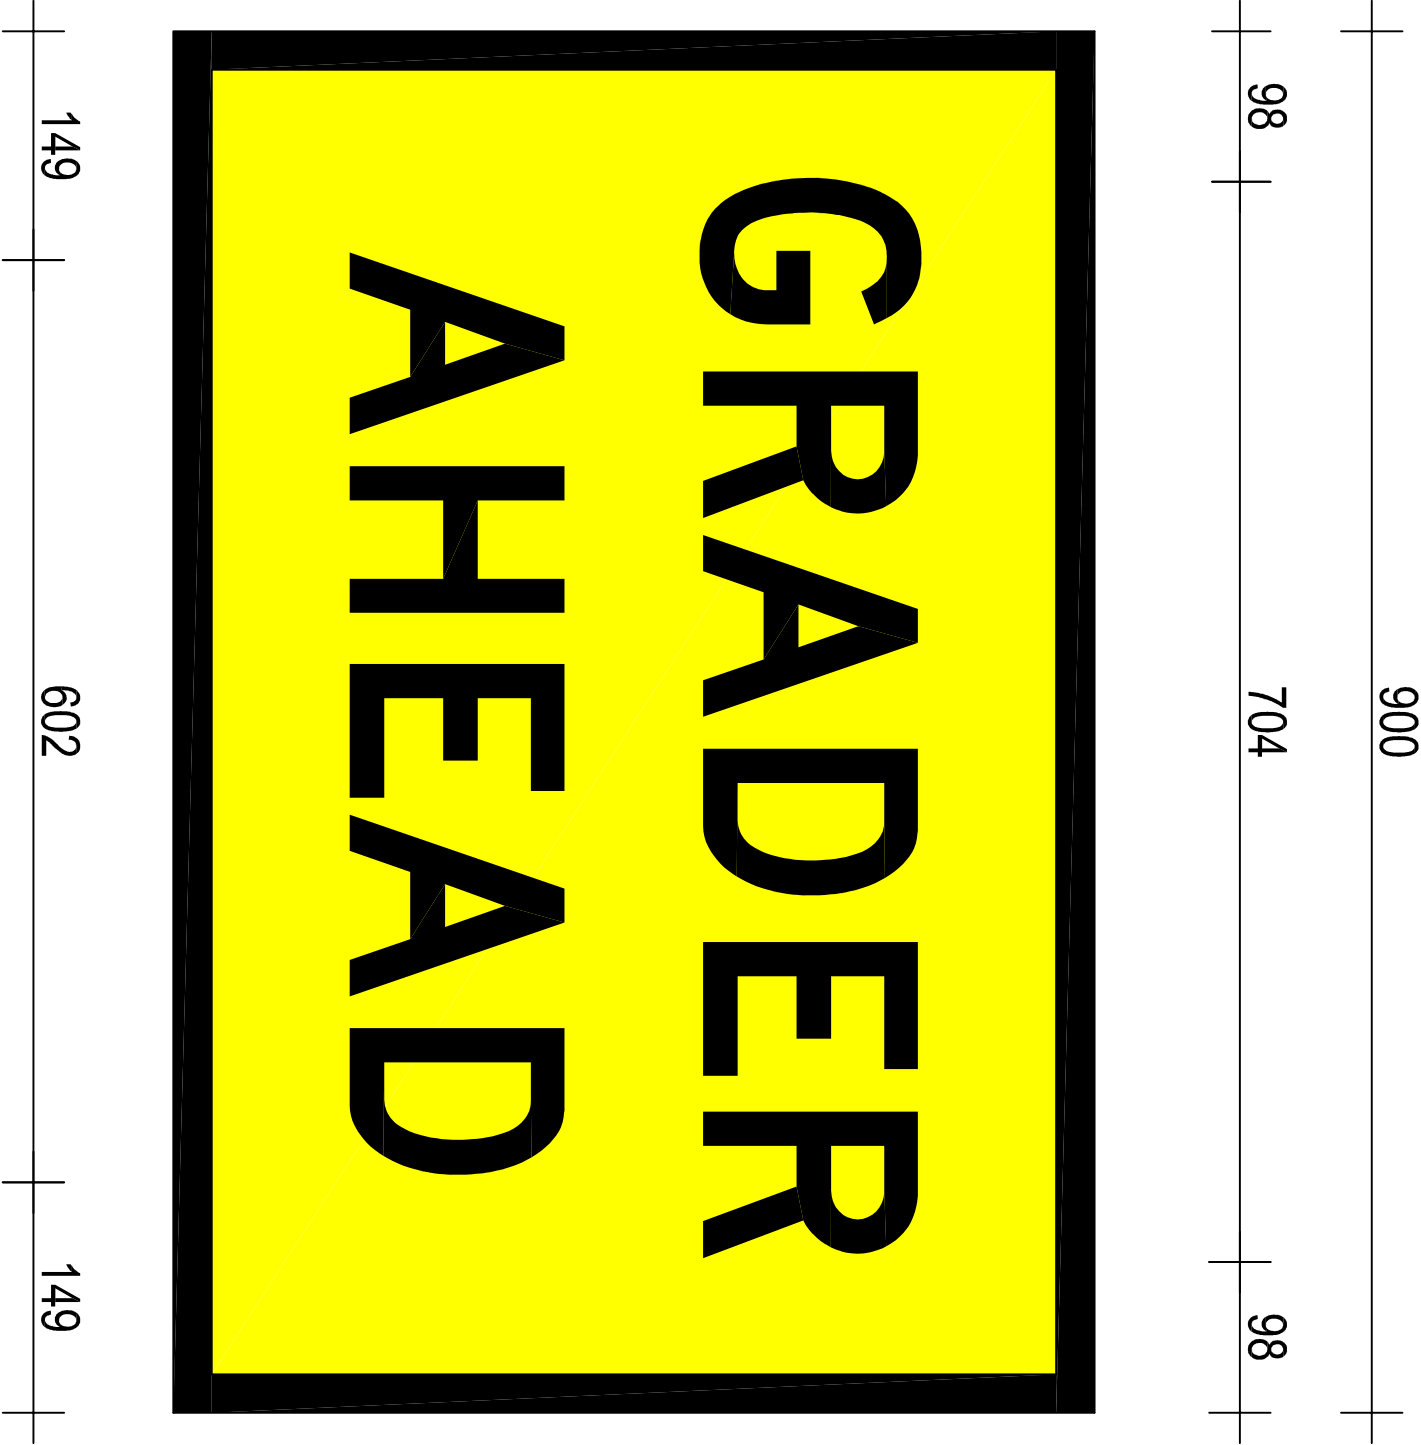

115
140
90
140
115
140D
140D

ACCEPTED FOR CONSTRUCTION