


0 5 10 15 20 25 30 35 40 45 50mm ON A3 SIZE ORIGINAL

OR CODE		Revision	REV	DATE	AMENDMENT / REVISION DESCRIPTION	APPROVAL	DRAWING FILE LOCATION / NAME: H:\SIGNS\TITDRAWMING\PLOTTING\T223.DWG	DESIGNED	VERIFIED	 Transport Roads & Maritime Services	TEMPORARY SIGN T2-23 END DETOUR	A3				
		01	22-06-18	AS Forms & material classification revised	P. Oliver	MATERIALS: ALUMINIUM SIGN BLACK LEGEND AND BORDER ON AS1906.1 CL 400 YELLOW REFLECTORISED GROUND	SIGNED: M. Davies NAME: M. Davies DATE: 12-07-19 REVIEWED: J. Rozos NAME: J. Rozos DATE: 12-07-19	SIGNED: P. Oliver NAME: P. Oliver DATE: 12-07-19 TITLE: Manager Guidance & Delineation								
ALL DIMENSIONS ARE IN MILLIMETRES UNLESS OTHERWISE SPECIFIED						SIGN TO BE MANUFACTURED IN ACCORDANCE WITH RMS QA SPECIFICATION 3400	PREPARED BY GUIDANCE AND DELINEATION TRAFFIC ENGINEERING SERVICES TECHNICAL AND PROJECT SERVICES									
										SCALE: 1:10		SHEET 1 OF 1		ENDS 1K XXXXXXXXXX	SHEET NO. 1	ISSUE 01
© Roads and Maritime Services																

ACCEPTED FOR CONSTRUCTION

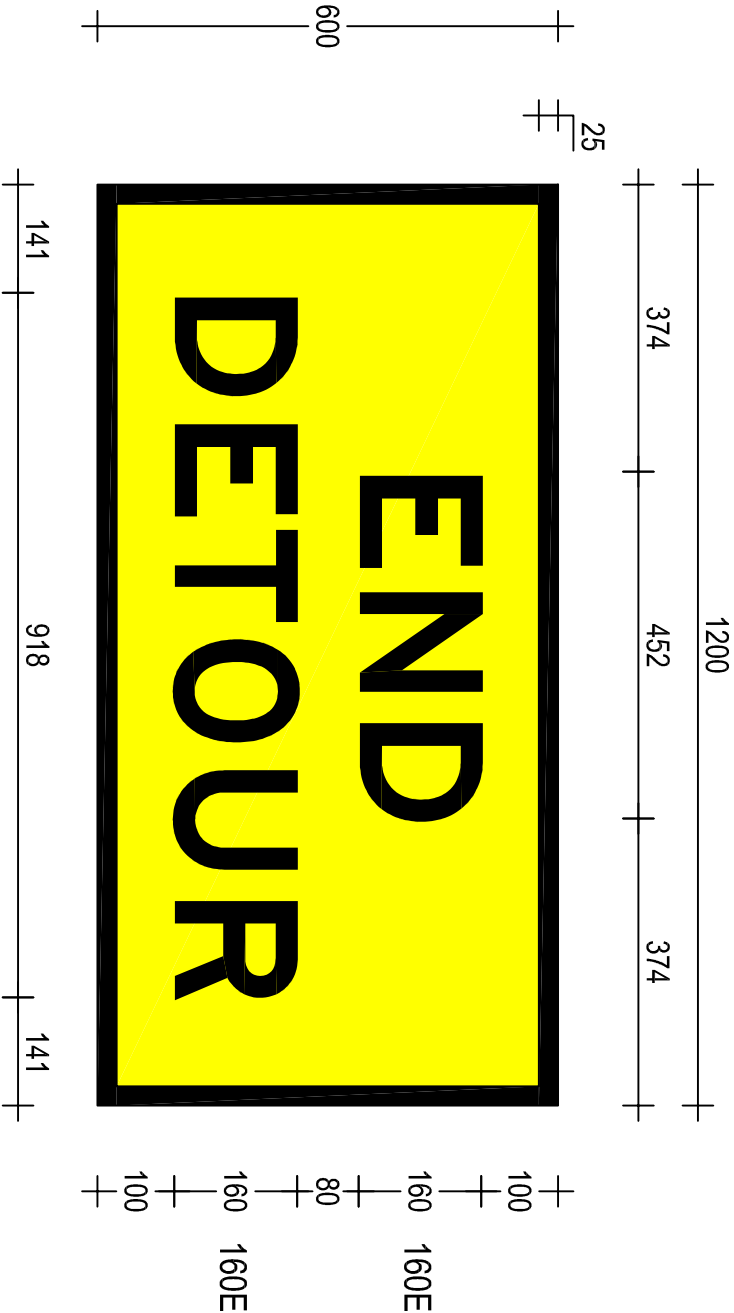

T2-23
1200 x 600