


OR CODE	Scan to Check Document Version	REV	01	DATE	23-06-18	AMENDMENT / REVISION DESCRIPTION	AS Forms & material classification revised	APPROVAL	P. Oliver	DRAWING FILE LOCATION NAME	H:\SIGN\T1TDRAWINGS\PL01TEMP235n(R).DWG	DESIGNED	SIGNED	VERIFIED	 Transport Roads & Maritime Services PREPARED BY GUIDANCE AND DELINEATION UNIT TRAFFIC ENGINEERING SERVICES TECHNICAL AND PROJECT SERVICES	TEMPORARY SIGN T2-235n(R) LANE CLOSED (Over hazard marker Right) SCALE: 1:10	EDMS No. XXXXXXXXXX	SHEET No. 1	ISSUE 01	A3	
MATERIALS: ALUMINIUM SIGN BLACK LEGEND SYMBOL AND BORDER ON AS1906.1 CL.400 YELLOW REFLECTORISED GROUND											SIGNED	M. Davies	SIGNED	P. Oliver							
												DATE	31-07-19	TITLE	Manager, Guidance & Delineation						
												REVIEWED	SIGNED	J. Rozzoni	DATE	31-07-19					
												NAME	J. Rozzoni	DATE	31-07-19						
ALL DIMENSIONS ARE IN MILLIMETRES UNLESS OTHERWISE SPECIFIED												SIGN TO BE MANUFACTURED IN ACCORDANCE WITH RIMS QA SPECIFICATION 3400									
0																					
5																					
10																					
15																					
20																					
25																					

ACCEPTED FOR CONSTRUCTION

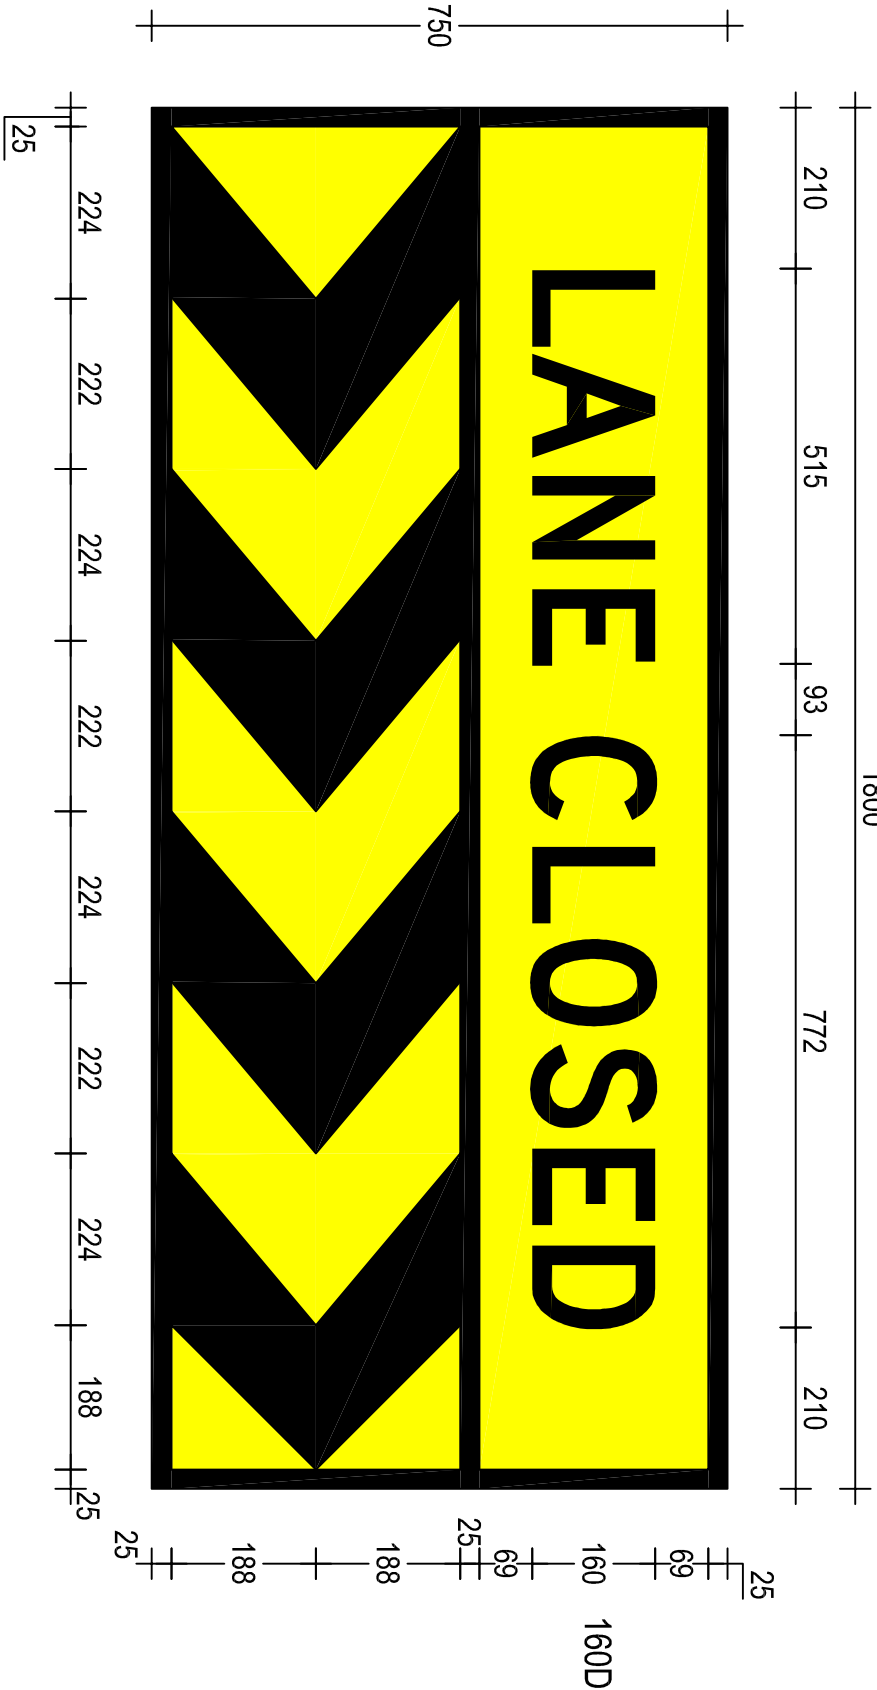

T2-235n(R)
1800 x 750

Symbol Detail

