



05101520253035404550mm ON A3 SIZE ORIGINAL

OR CODE	Scan to Check Document Version	REV	DATE	AMENDMENT / REVISION DESCRIPTION	APPROVAL	DRAWING FILE LOCATION / NAME: H:\SIGN\TTP\DRAWINGS\PL\OTTEMP\T3-3.DWG	
		01	23-03-18	AS Forms & material classification revised	P.Oliver	MATERIALS: ALUMINIUM SIGN BLACK LEGEND AND BORDER ON AS1906.1 CL.400 YELLOW REFLECTORISED GROUND	
ALL DIMENSIONS ARE IN MILLIMETRES UNLESS OTHERWISE SPECIFIED						SIGN TO BE MANUFACTURED IN ACCORDANCE WITH RMS QA SPECIFICATION 3400	
DESIGNED		VERIFIED		PREPARED BY			
SIGNED: 		SIGNED: 		NSW GOVERNMENT			
NAME: M. Davies		NAME: P. Oliver		Transport Roads & Maritime Services			
DATE: 31-07-19		DATE: 31-07-19		GUIDANCE AND DELINEATION UNIT			
REVIEWED		TITLE: Manager, Guidance & Delineation		TRAFFIC ENGINEERING SERVICES			
SIGNED: 		DATE: 31-07-19		TECHNICAL AND PROJECT SERVICES			
NAME: J. Rozos				TEMPORARY SIGN			
DATE: 31-07-19				T3-3			
				SLIPPERY (Symbolic)			
SCALE: 1:10		EDMS N ^o . XXXXXXXXXX		SHEET N ^o . 1		ISSUE 01	
						SHEET 1 OF 1	
						A3	


ACCEPTED FOR CONSTRUCTION

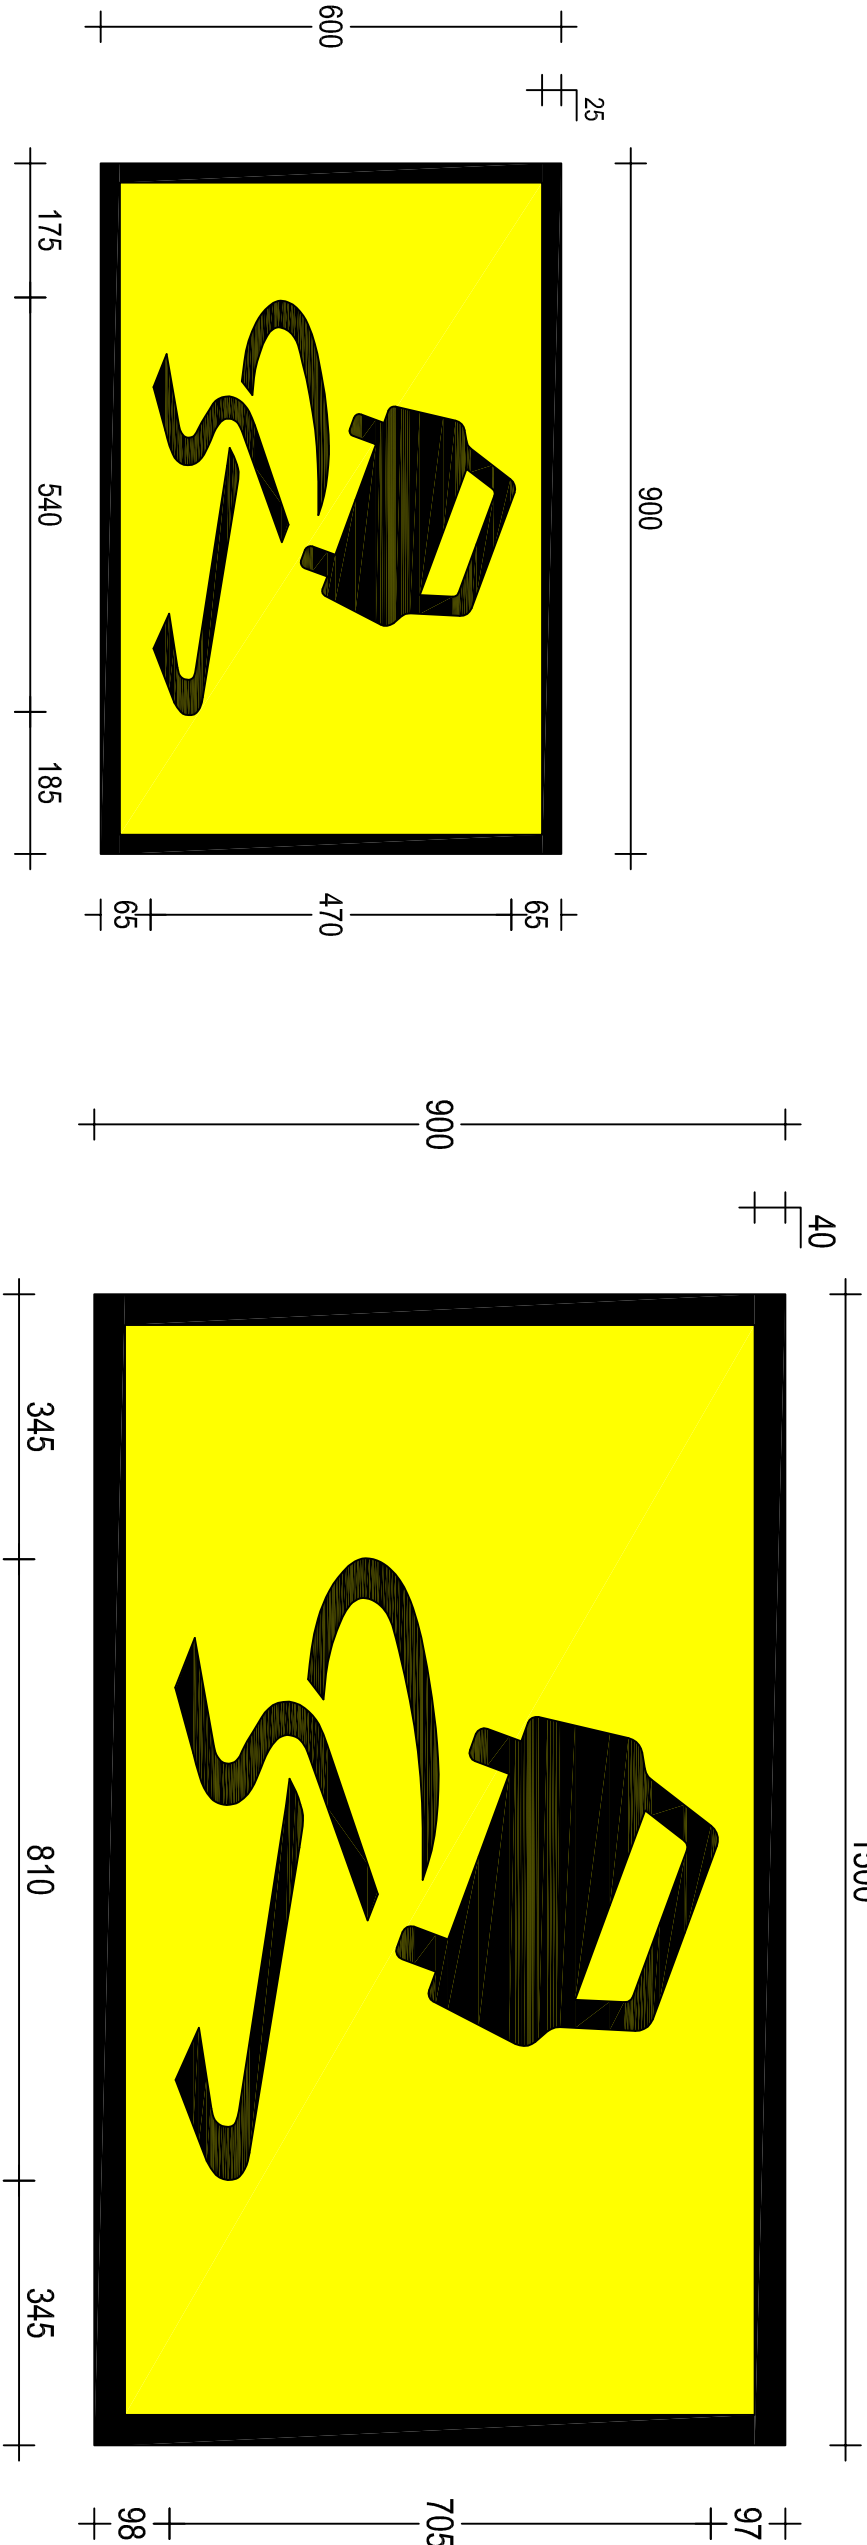


T3-3A
900 x 600

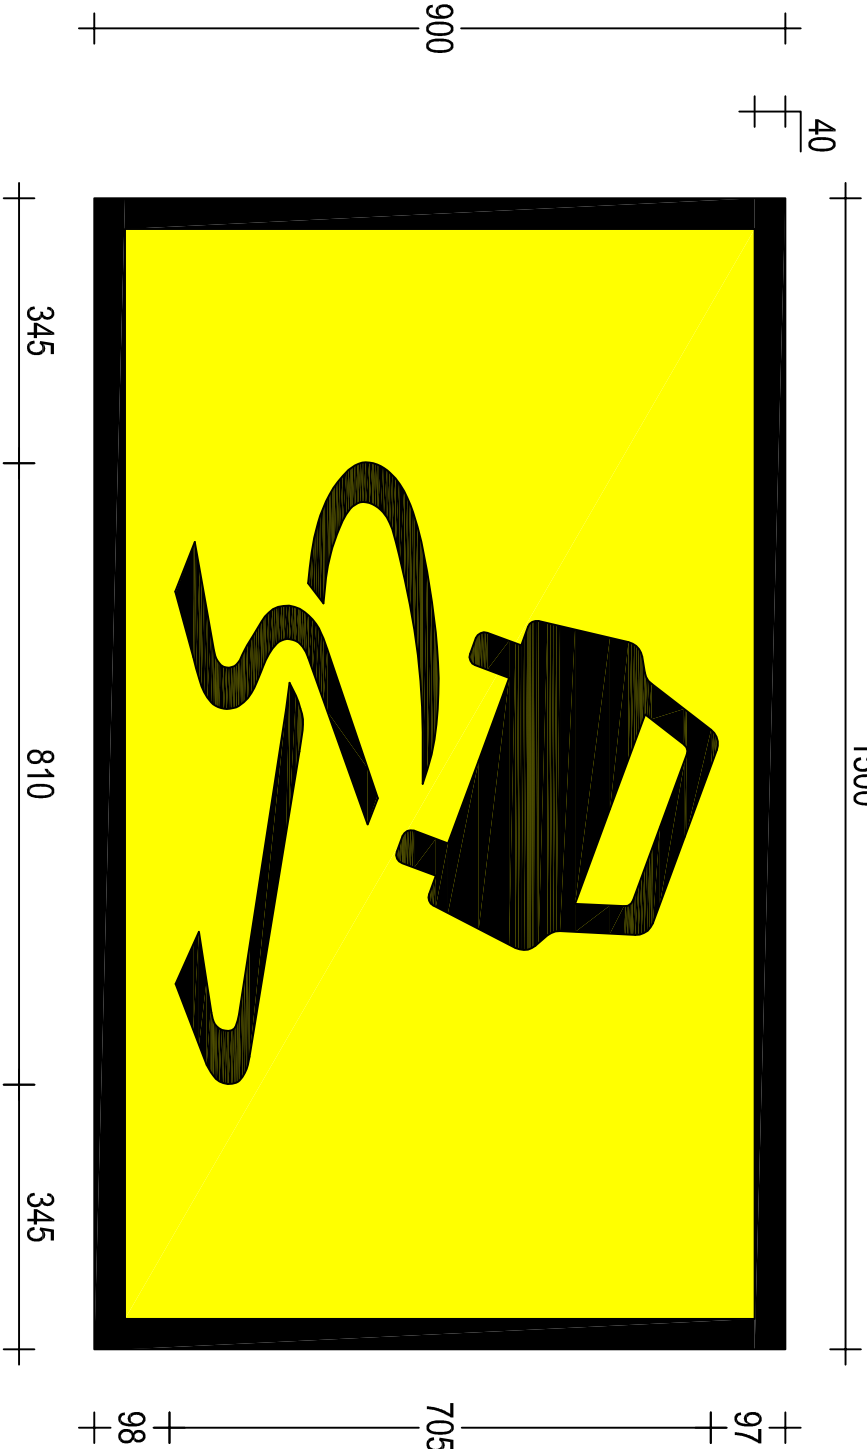

T3-3B
1500 x 900

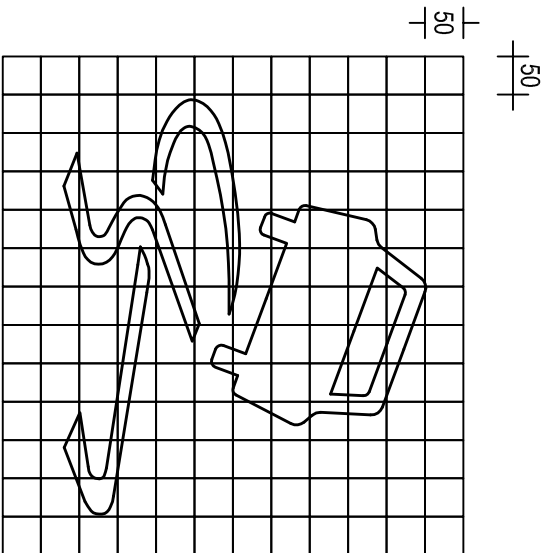

SYMBOL DETAIL

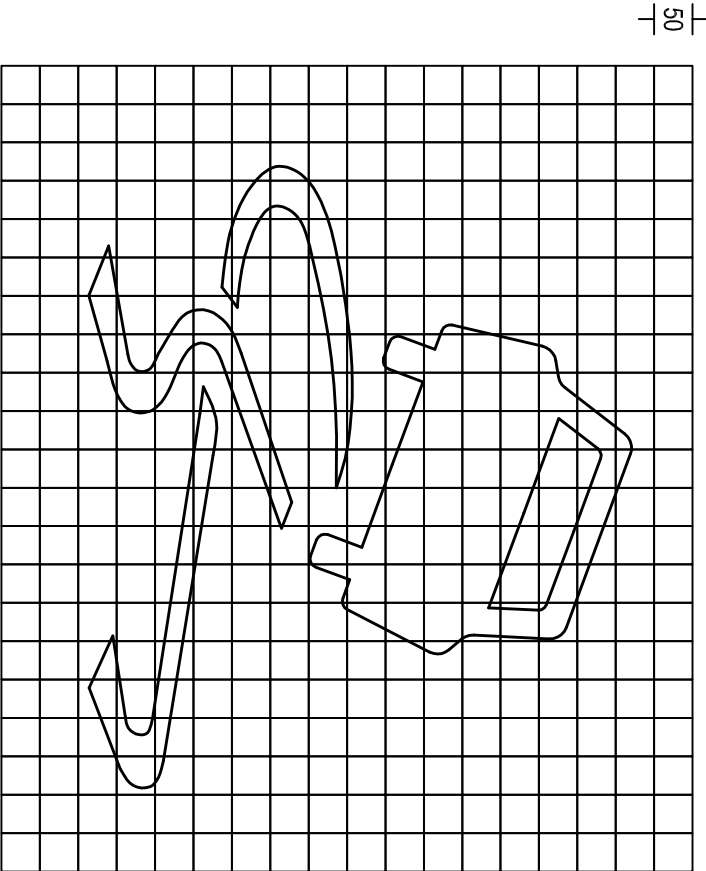

SYMBOL DETAIL