


0	5	10	15	20	25	30	35	40	45	50mm ON A3 SIZE ORIGINAL	
OR CODE		Scan to Check Document Version		REV	DATE	AMENDMENT / REVISION DESCRIPTION		APPROVAL		DRAWING FILE LOCATION / NAME: H:\SIGN\TTP\DRAWINGS\PL\OTTEMP\T5-4.DWG	
				01	23-03-18	AS Forms & material classification revised		P. Oliver		MATERIALS: ALUMINIUM SIGN BLACK SYMBOL AND BORDER ON AS1906.1 CL.400 YELLOW REFLECTORISED GROUND	
ALL DIMENSIONS ARE IN MILLIMETRES UNLESS OTHERWISE SPECIFIED										SIGN TO BE MANUFACTURED IN ACCORDANCE WITH RMS QA SPECIFICATION 3400	
				DESIGNED		VERIFIED		NSW GOVERNMENT Transport Roads & Maritime Services		TEMPORARY SIGN T5-4 HAZARD WARNING MARKER	
				SIGNED: M. Davies NAME: M. Davies DATE: 31-07-19		SIGNED: P. Oliver NAME: P. Oliver TITLE: Manager, Guidance & Delineation DATE: 31-07-19		PREPARED BY GUIDANCE AND DELINEATION UNIT TRAFFIC ENGINEERING SERVICES TECHNICAL AND PROJECT SERVICES		SCALE: 1:10	
				SIGNED: J. Rozos NAME: J. Rozos DATE: 31-07-19						EDMS N ^o . XXXXXXXXXX	
										SHEET 1 OF 1	
										ISSUE 01	

ACCEPTED FOR CONSTRUCTION

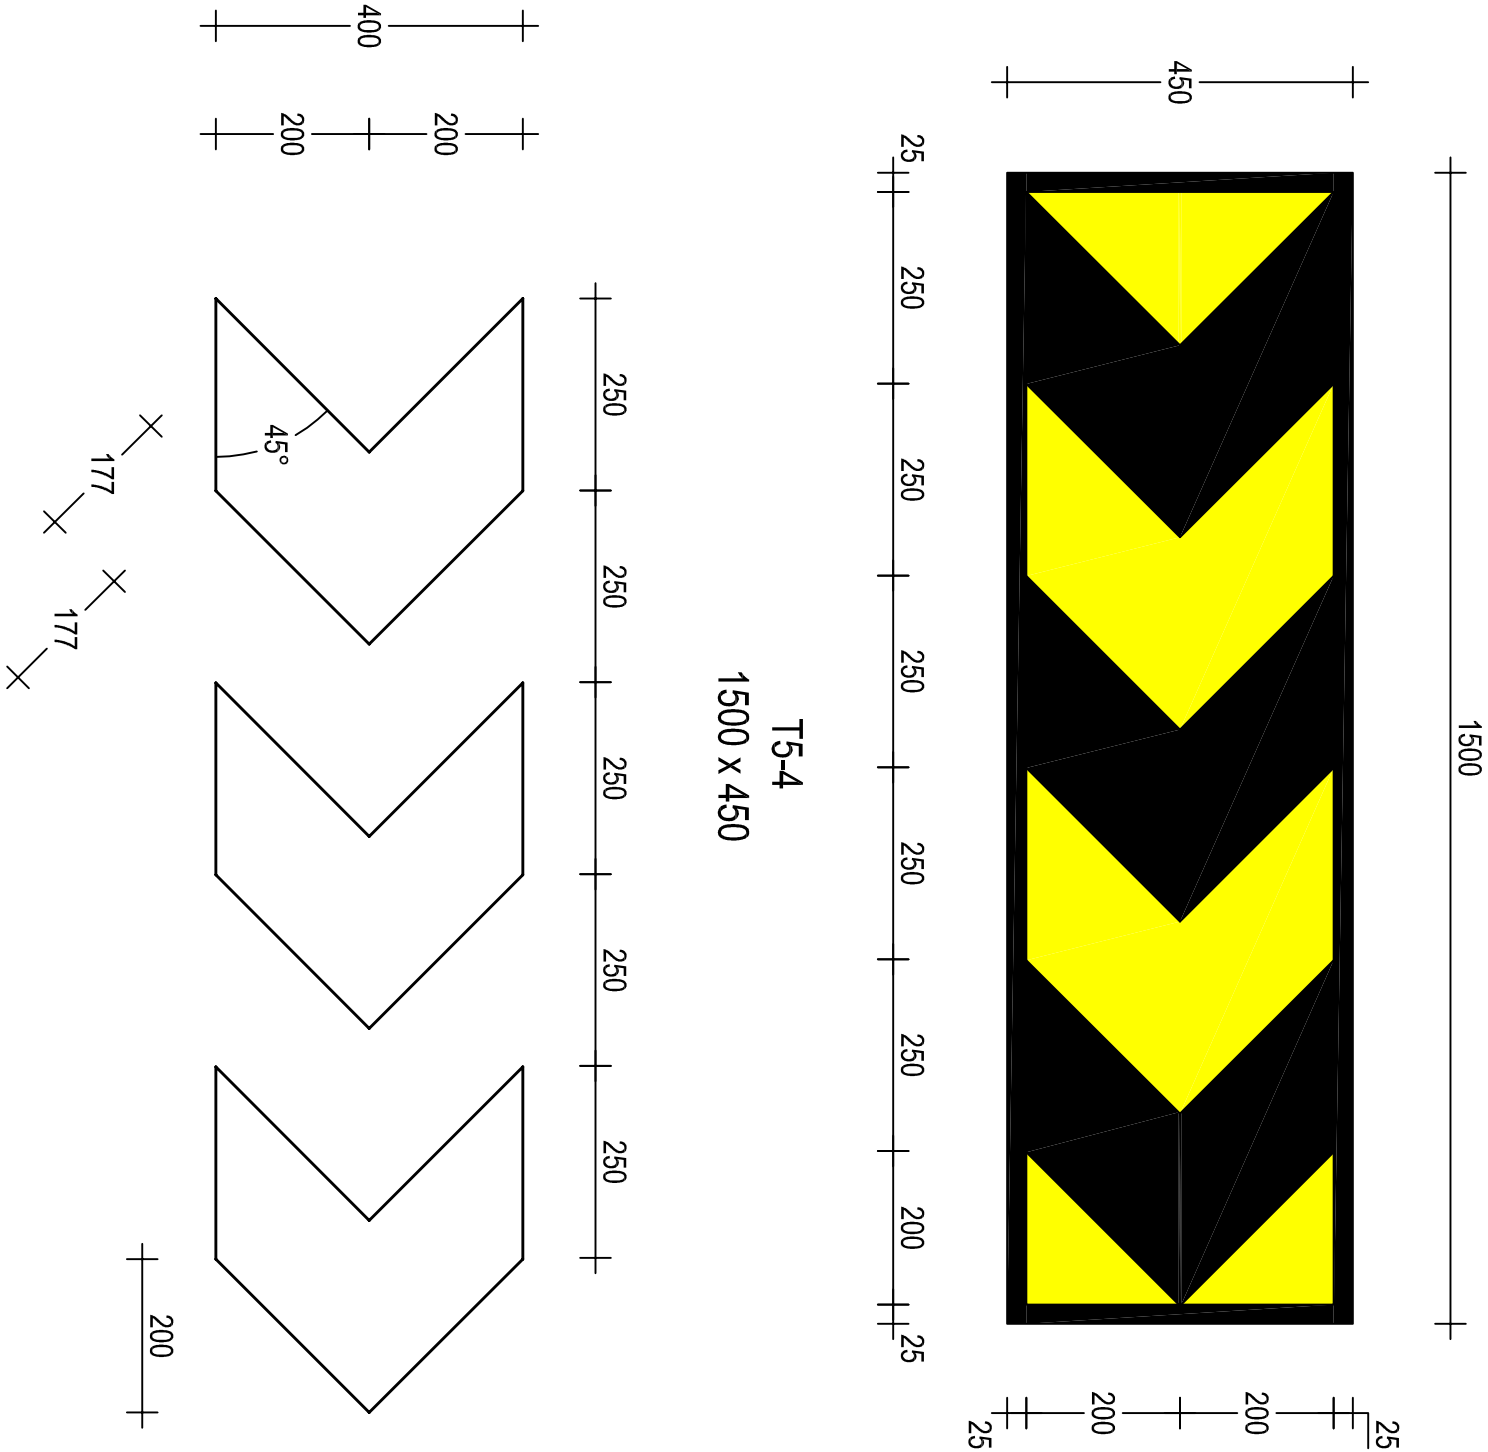

Symbol Detail