


OR CODE Scan to Check Document Version			REV /	DATE	AMENDMENT / REVISION DESCRIPTION	APPROVAL	DRAWING FILE LOCATION / NAME: H:\SIGN\TTP\DRAWINGS\PL\OTTEMP\T7-1.DWG	DESIGNED	VERIFIED	 Transport Roads & Maritime Services GOVERNMENT PREPARED BY GUIDANCE AND DELINEATION TRAFFIC ENGINEERING SERVICES TECHNICAL AND PROJECT SERVICES				
			01	23-03-18	AS Forms & material classification revised	P. Oliver	MATERIALS: ALUMINIUM SIGN BLACK LEGEND AND BORDER ON AS1906.1 CL.400 YELLOW REFLECTORISED GROUND	SIGNED NAME M. Davies DATE 12-07-19 REVIEWED NAME J. Rozos DATE 12-07-19	SIGNED NAME P. Oliver TITLE Manager, Guidance & Delineation DATE 12-07-19					
ALL DIMENSIONS ARE IN MILLIMETRES UNLESS OTHERWISE SPECIFIED						SIGN TO BE MANUFACTURED IN ACCORDANCE WITH RMS QA SPECIFICATION 3400								
TEMPORARY SIGN											A3			
T7-1														
SLOW BAT														
SHEET 1 OF 1														
SCALE: 1:10				EDMS N ^o . XXXXXXXXXX		SHEET N ^o . 1		ISSUE 01						

ACCEPTED FOR CONSTRUCTION

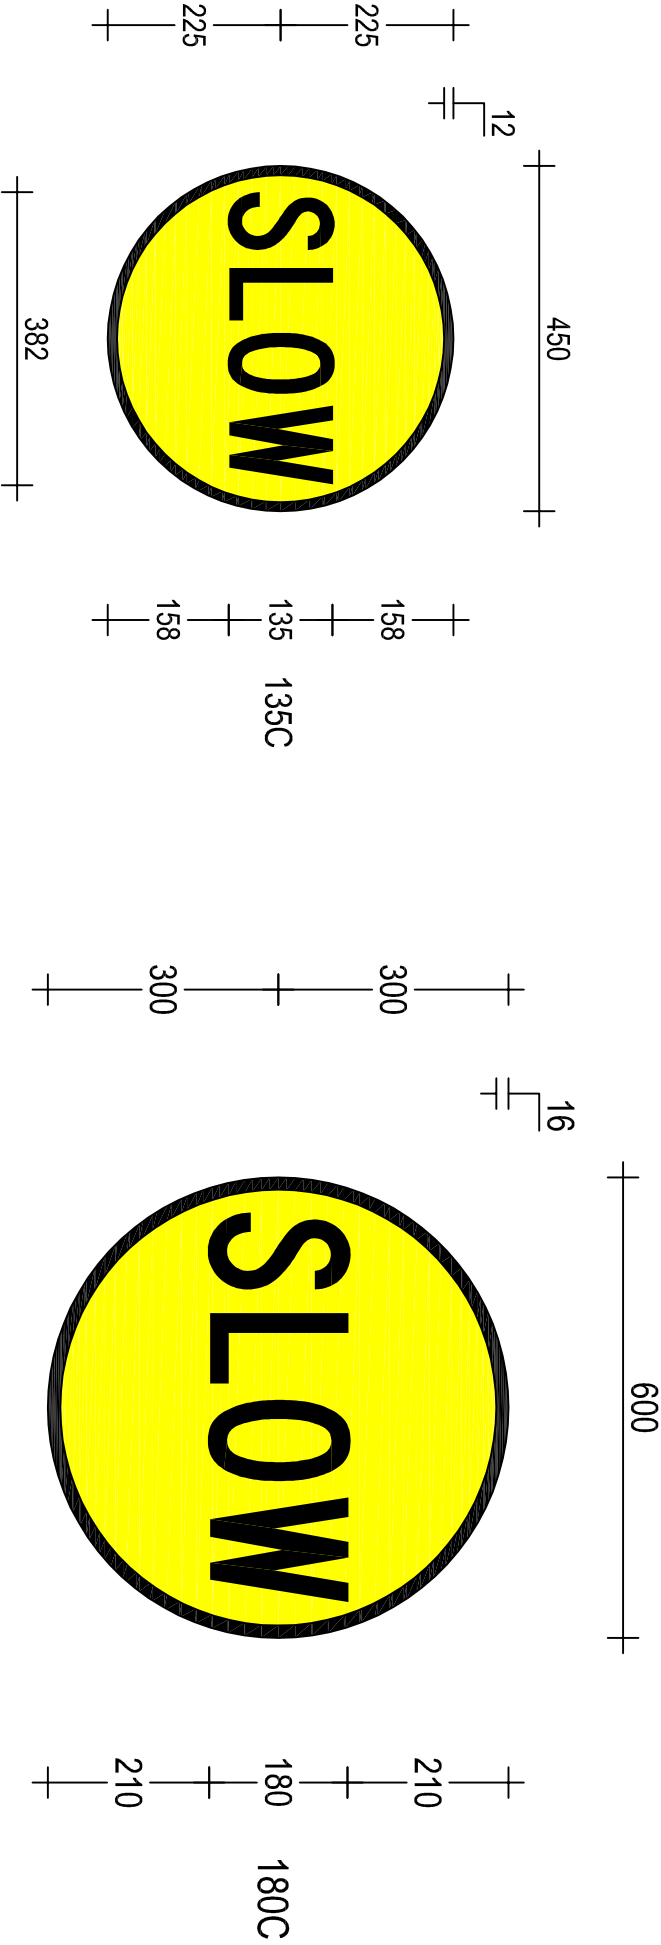

Note: This sign is used in conjunction with Sign No.R6-8 where a double-sided Stop/Slow bat is required