
 
 
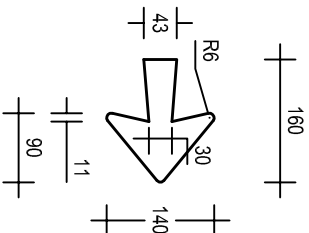


0 5 10 15 20 25 30 35 40 45 50mm ON A3 SIZE ORIGINAL

OR CODE Scan to check Document Version		REV / DATE	AMENDMENT / REVISION DESCRIPTION	APPROVAL	DRAWING FILE LOCATION / NAME: R:\SIGNS\TITD\DRAWINGS\PL\TITD\MTB\T8-2JWG	DESIGNED SIGNED:  NAME: M. Davies DATE: 31-07-19 REVIEWED SIGNED:  NAME: J. Rodos DATE: 31-07-19	VERIFIED SIGNED:  NAME: P. Oliver DATE: 31-07-19 TITLE: Manager, Guidance & Delineation	 Transport Roads & Maritime Services PREPARED BY GUIDANCE AND DELINEATION UNIT TRAFFIC ENGINEERING SERVICES TECHNICAL AND PROJECT SERVICES		TEMPORARY SIGN T8-2(R) PEDESTRIANS (Right arrow) SHEET 1 OF 1		A3	
ALL DIMENSIONS ARE IN MILLIMETRES UNLESS OTHERWISE SPECIFIED					SIGN TO BE MANUFACTURED IN ACCORDANCE WITH RMS QA SPECIFICATION 3400			SCALE: 1:10		EDMS No. XXXXXXXXX	SHEET No. 1	ISSUE 01	© Roads and Maritime Services

ACCEPTED FOR CONSTRUCTION

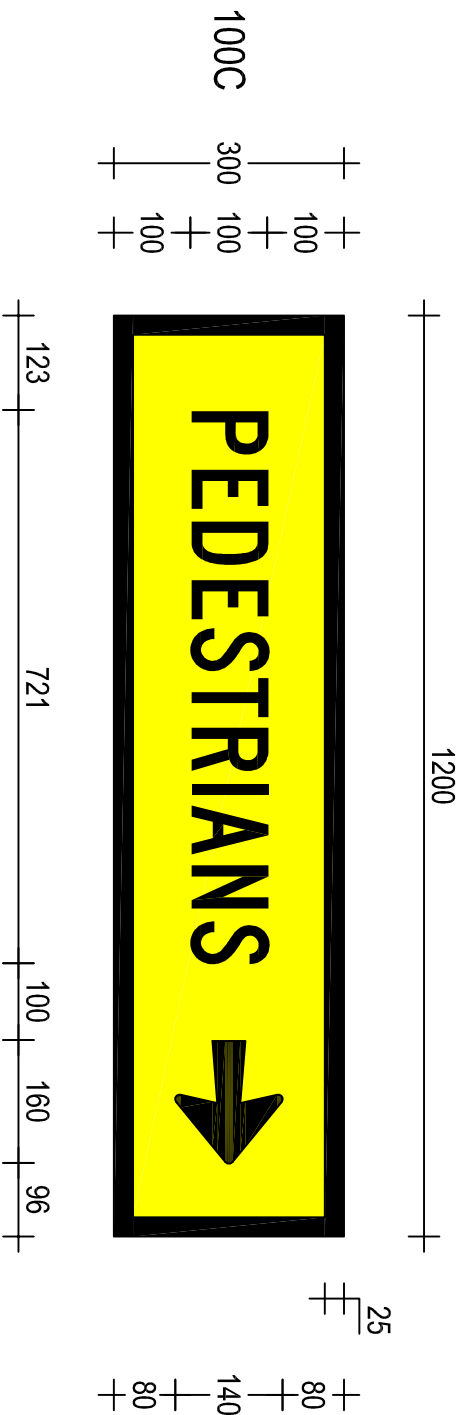

Arrow Detail