


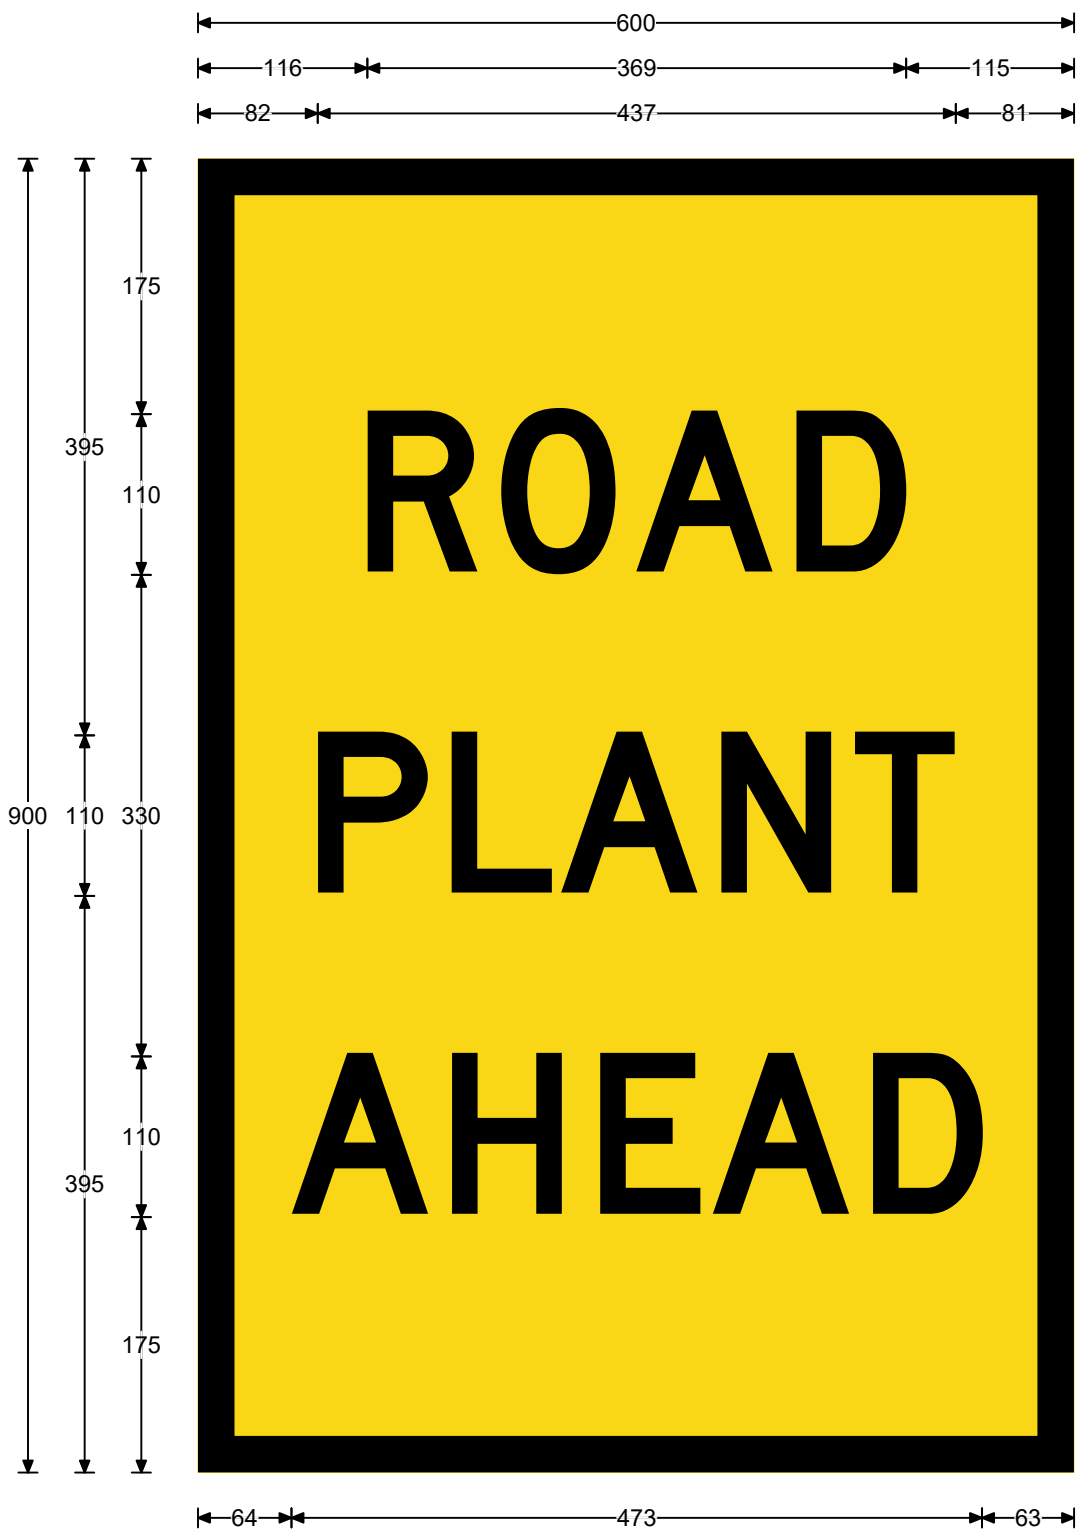

<u>Legend</u>	<u>Font Type</u>	<u>Font Size</u>
ROAD	FHWA Series D2000EX	110
PLANT	FHWA Series D2000EX	110
AHEAD	FHWA Series D2000EX	110

Specifications:
 Aluminium Sign
 Black lgd & Border
 Cl.400 Yellow refl grd(AS1906.1)

Size:	900 x 600	Date:	22/4/20
Area:	0.54 sq.m	Scale:	1:5.2
Border:	0 x 25	Drawn:	DaviesM
Cnr Rad:	0	Checked:	
Patch CR:	NA	File:	tm1-3-1_d
 Prepared using TraSiCAD Product of QMR		Path:	H:\Signs\TTT\DRAWINGS\IMMS Signs
			tm1-3-1_d