

 
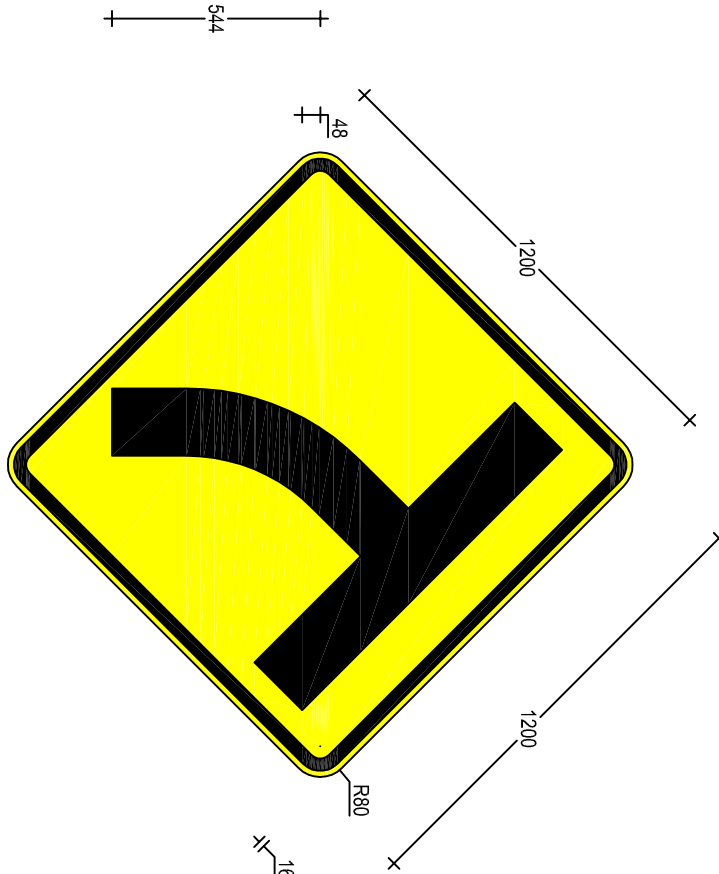
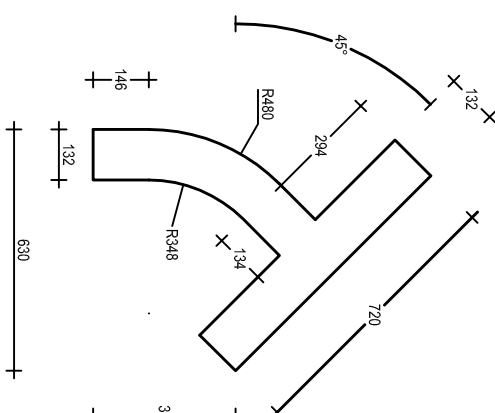
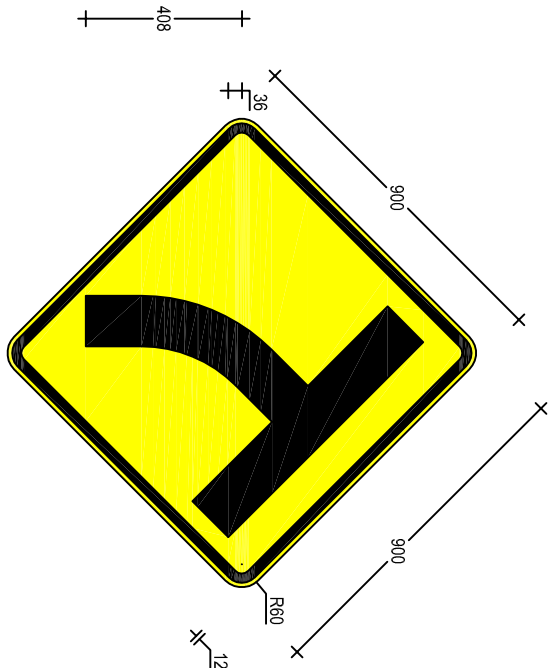
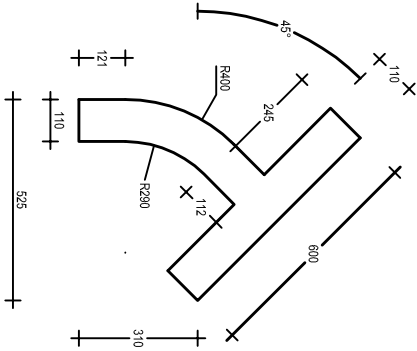
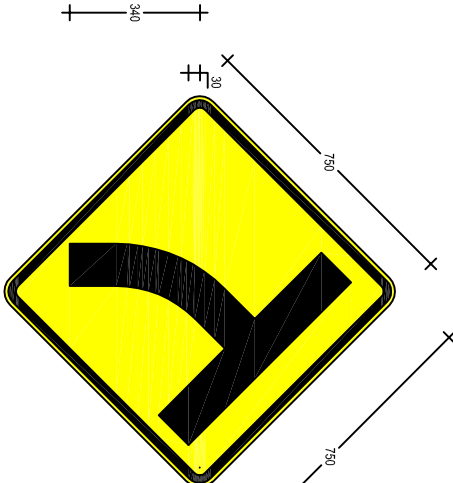
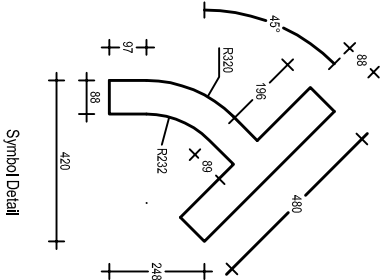


OR CODE Road to Order Document Version			REV 01	DATE 23-03-18	AMENDMENT / REVISION DESCRIPTION AS Forms & material classification revised		APPROVAL P.Oliver	DRAWING FILE LOCATION / NAME: H:\SIGN\TTP\DRAWINGS\PL\OTW\ARNW2-14.dwg						
					DESIGNED SIGNED  NAME M. Davies DATE 31-07-19 REVIEWED  SIGNED NAME J. Rozdos DATE 31-07-19					VERIFIED SIGNED  NAME P. Oliver TITLE Manager Guidance & Delineation DATE 31-07-19				
 Transport Roads & Maritime Services										PREPARED BY GUIDANCE AND DELINEATION UNIT TRAFFIC ENGINEERING SERVICES TECHNICAL AND PROJECT SERVICES				
WARNING SIGN W2-14(R) T INTERSECTION CURVED APPROACH (Right Symbolic)										SHEET 1 OF 1				
SCALE: 1:20										EDMS No. XXXXXXXX SHEET No. 1 ISSUE 01				
© Roads and Maritime Services														

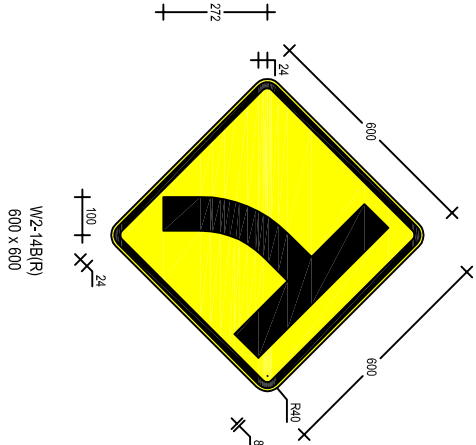

W2-14B(R)
600 x 600

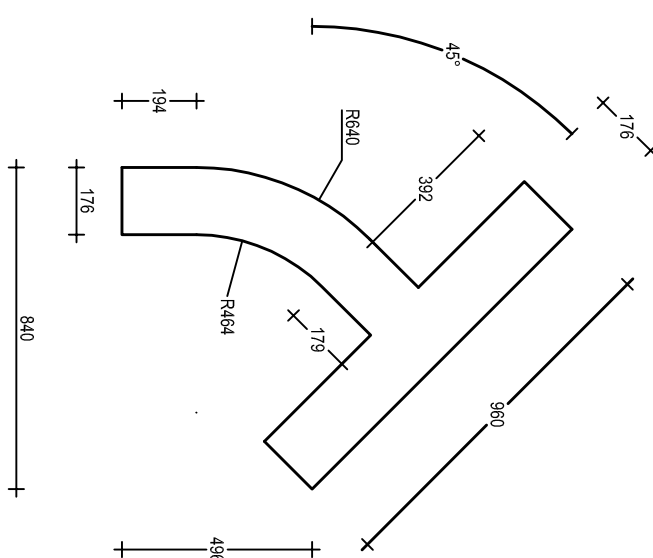

Symbol Detail

ACCEPTED FOR CONSTRUCTION