

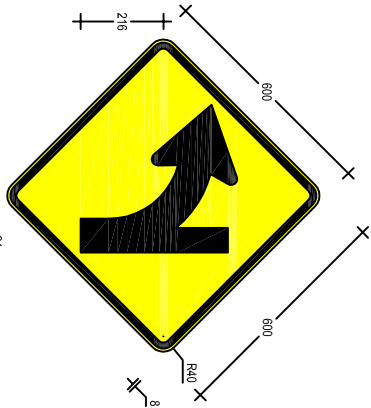


OR CODE Sign & Check Document Version				REV/ 01	DATE 22-08-18	AMENDMENT / REVISION DESCRIPTION AS Forms & material classification revised		APPROVAL P.Oliver	DRAWING FILE LOCATION / NAME: H:\SIGN\ITTDRAWINGS\PROJECT\WARRW2-16.LDWG												
MATERIALS: ALUMINIUM SIGN BLACK SYMBOL AND BORDER ON AS1906.1 CL.400 YELLOW REFLECTORISED GROUND										DESIGNED				VERIFIED							
										SIGNED				SIGNED							
										NAME M.Davies				NAME P.Oliver							
										DATE 31-07-19				DATE 31-07-19							
SIGN TO BE MANUFACTURED IN ACCORDANCE WITH RMS QA SPECIFICATION 3400										REVIEWED				TITLE Manager Guidance & Delineation							
										SIGNED				SIGNED							
										NAME J.Rozos				DATE 31-07-19							
ALL DIMENSIONS ARE IN MILLIMETRES UNLESS OTHERWISE SPECIFIED										NAME				PREPARED BY							
										DATE 31-07-19				GUIDANCE AND DELINEATION UNIT							
														TRAFFIC ENGINEERING SERVICES							
														TECHNICAL AND PROJECT SERVICES							
WARNING SIGN W2-16(L) SIDE ROAD ON STRAIGHT ALIGNMENT (Left Symbolic)										SHEET 1 OF 1				A3							
										SCALE: 1:20				EDMS No. XXXXXXXXXX				SHEET No. 1			



ACCEPTED FOR CONSTRUCTION

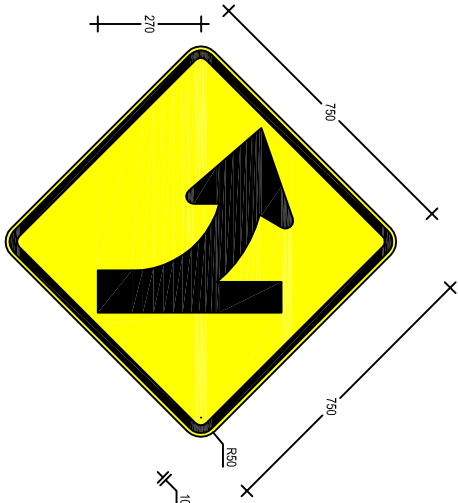



W2-16A(L)
600 x 600

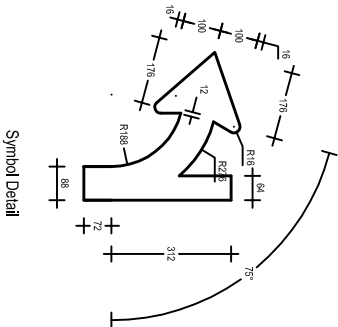


W2-16B(L)
750 x 750

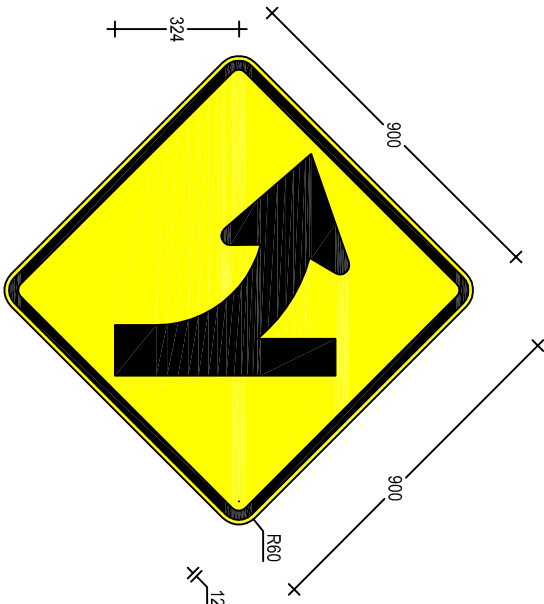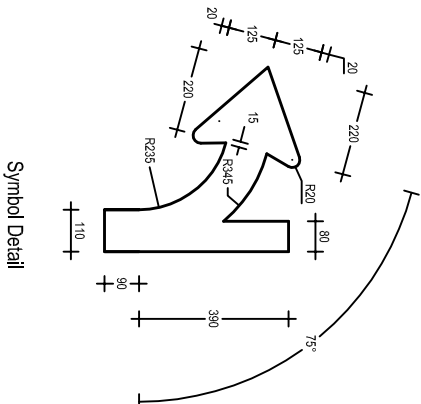

W2-16C(L)
900 x 900

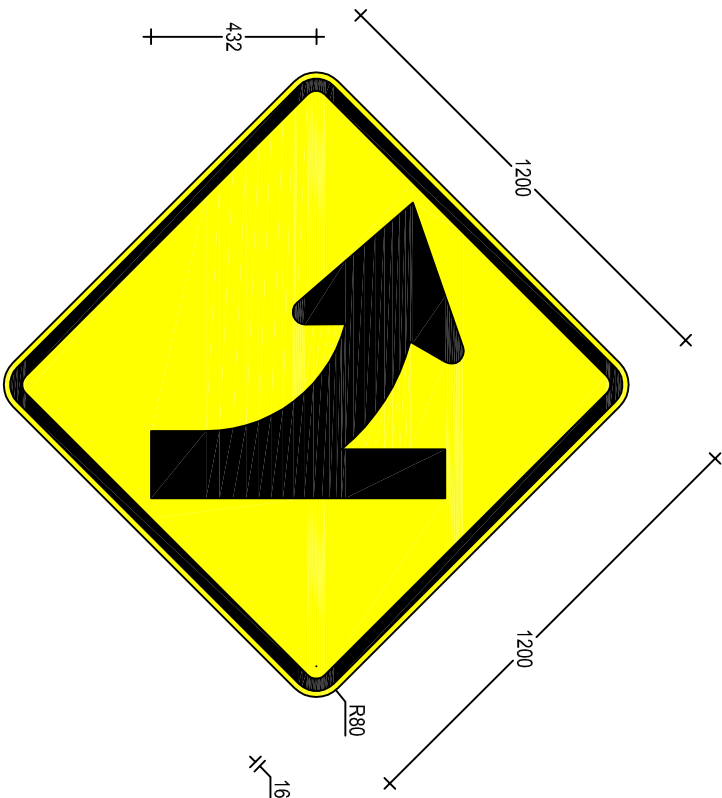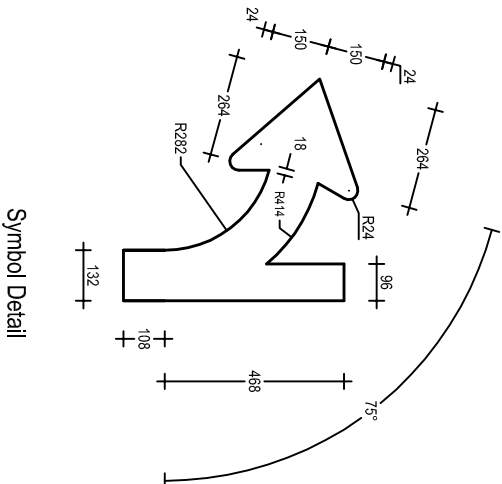

W2-16D(L)
1200 x 1200

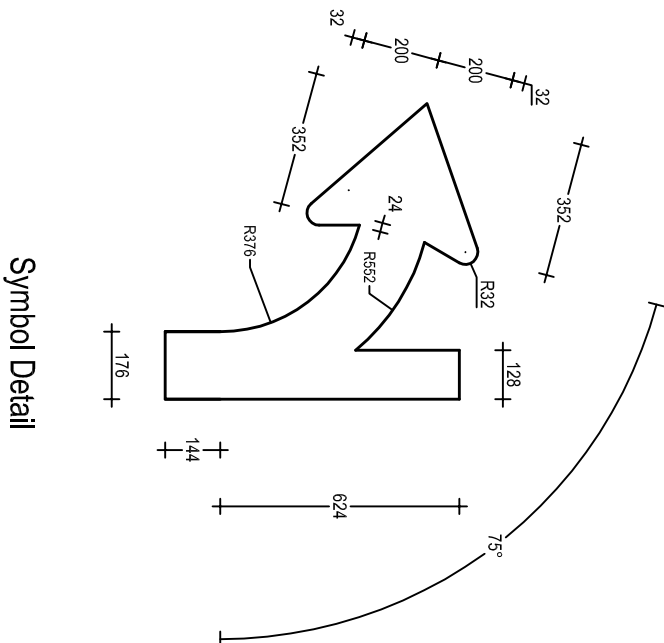

Symbol Detail