
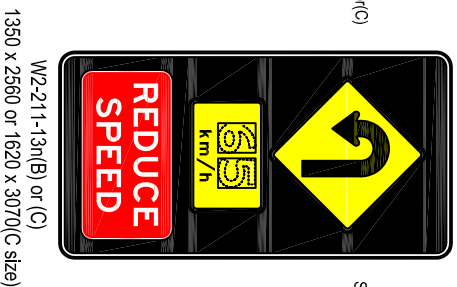
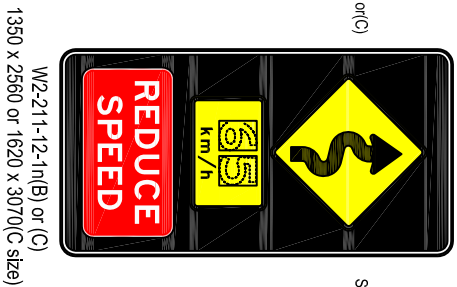
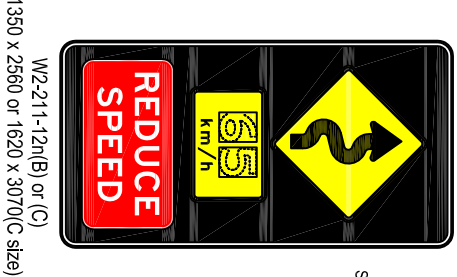
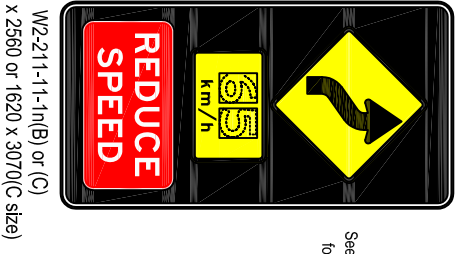
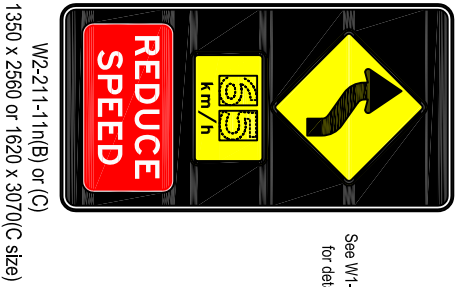
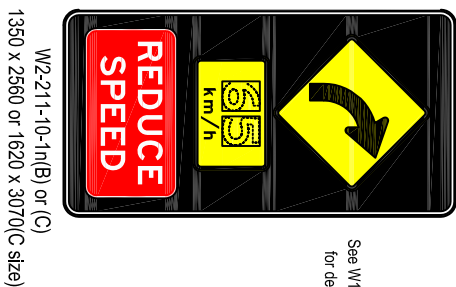
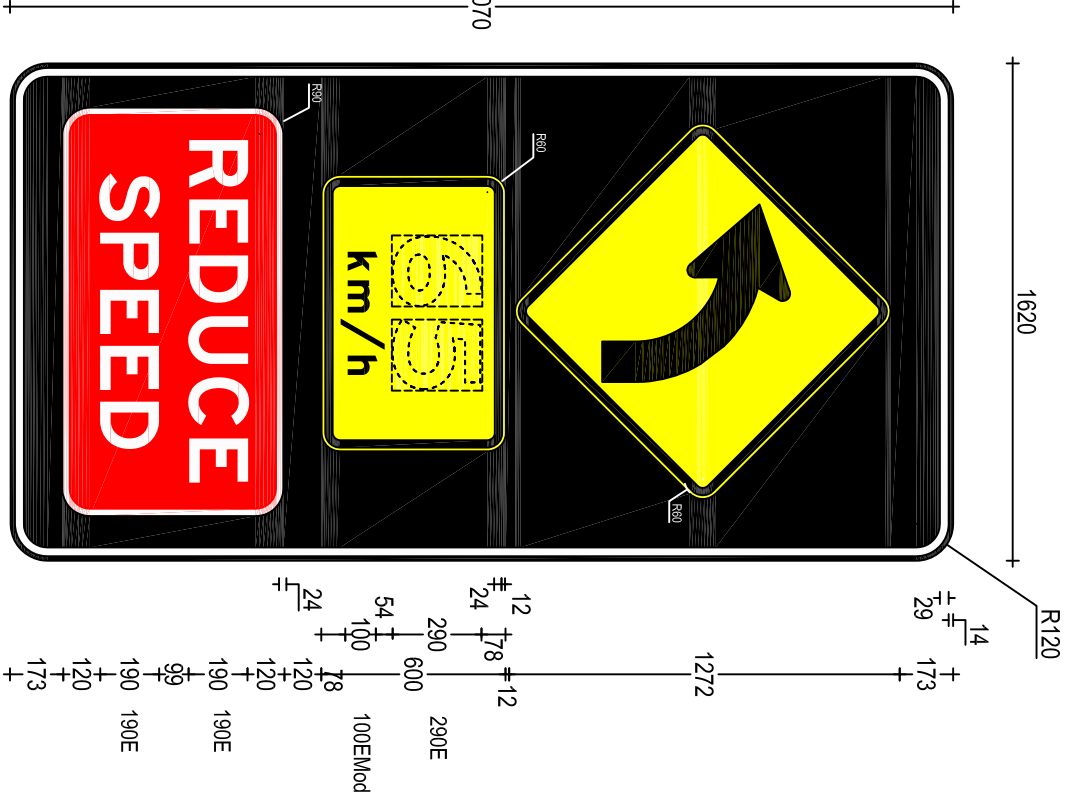
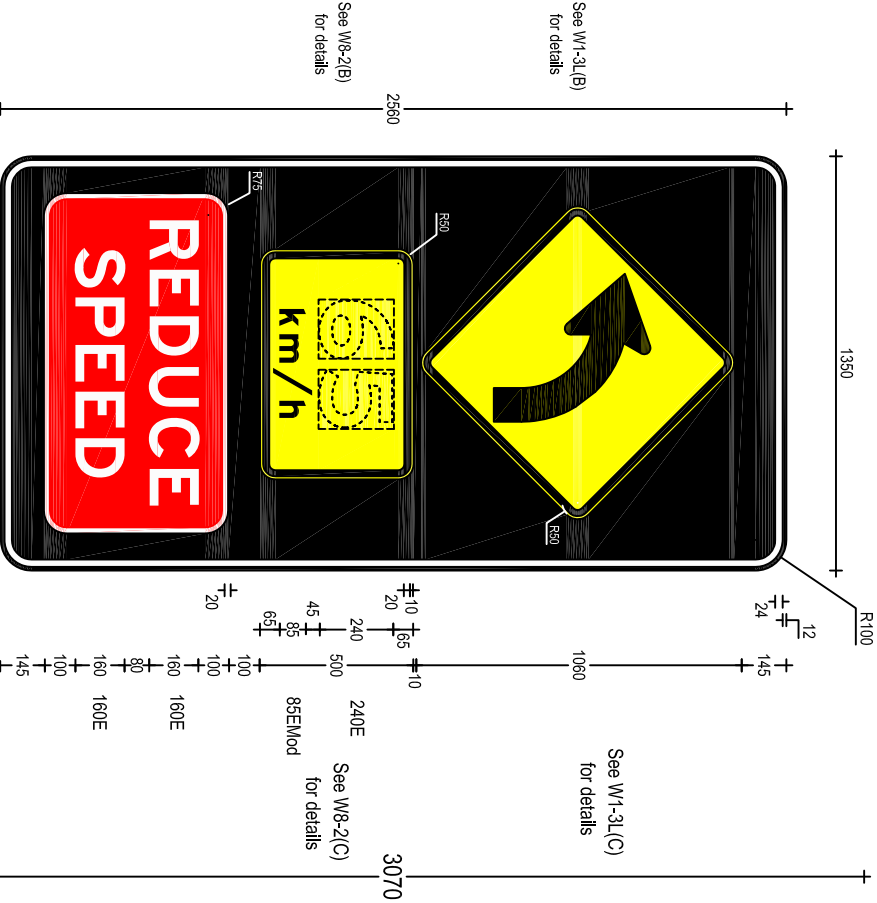
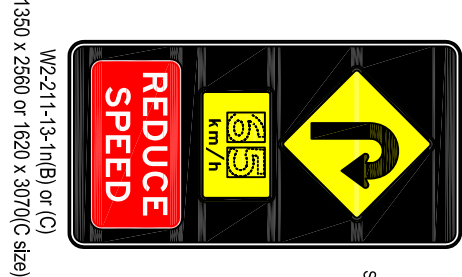
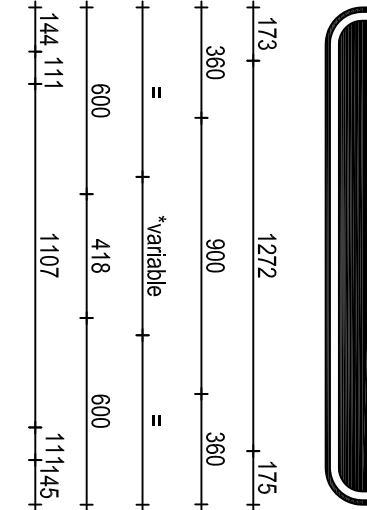


OR CODE	Scan to Check Document Version	REV	DATE	AMENDMENT / REVISION DESCRIPTION	APPROVAL	DRAWING FILE LOCATION / NAME: H:\SIGN\TTP\DRAWINGS\PROJECT\WARRW\211-10nDwg	DESIGNED	VERIFIED	PREPARED BY	WARNING SIGN	A3
		01	23-03-18	AS Forms & material classification revised	P. Oliver	MATERIALS: ALUMINIUM SIGN CL.400 WHITE BDR ON BLACK GRD WARNING SYMBOL & PLATE: BLACK LGD/SYMBOL & BDR ON CL.400 YELLOW REFL GRD REDUCE SPEED: CL.400 WHITE REFL LGD/CL.400 REFL RED GRD	SIGNED: M. Davies DATE: 31-07-19 REVIEWED SIGNED: J. Rozdos NAME: J. Rozdos DATE: 31-07-19	SIGNED: P. Oliver NAME: Manager, Guidance & Definition DATE: 31-07-19	NSW GOVERNMENT Transport Roads & Maritime Services	W2-211-11n REDUCE SPEED REVERSE CURVE (LEFT) + ADVISORY SPEED km/h SCALE: 1:25	ISSUE EDMS No. XXXXXXXXXX SHEET No. 1 01
ALL DIMENSIONS ARE IN MILLIMETRES UNLESS OTHERWISE SPECIFIED											
SIGN TO BE MANUFACTURED IN ACCORDANCE WITH RMS QA SPECIFICATION 3400											

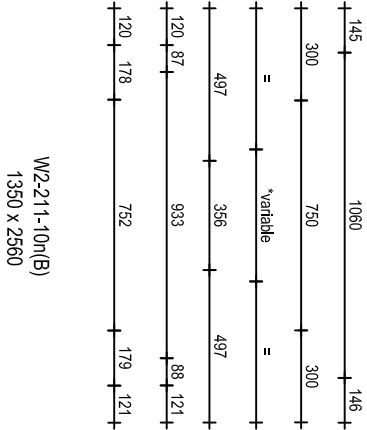

ACCEPTED FOR CONSTRUCTION