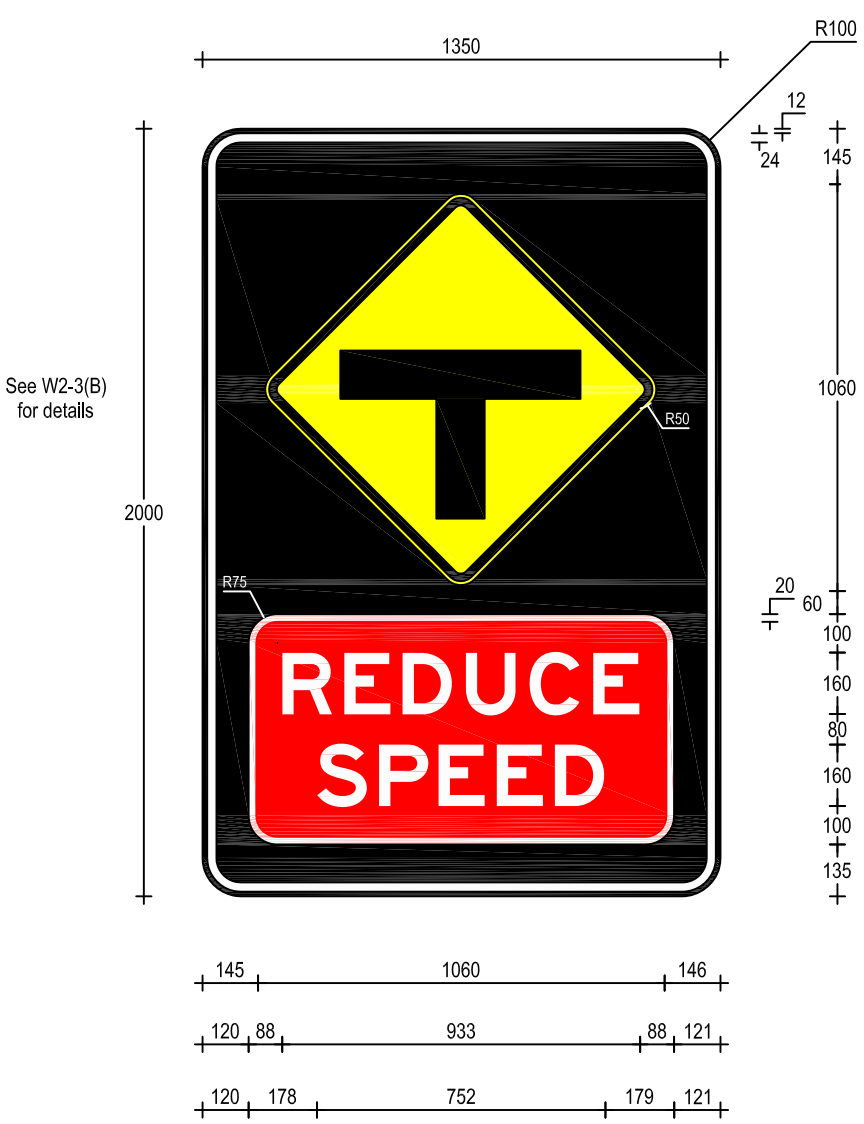

W2-211-3n(B) (Option 1)
1350 x 2000

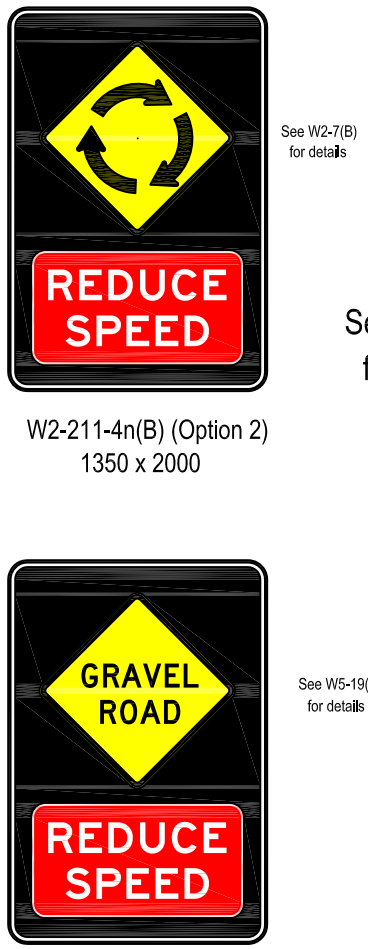

W2-211-4n(B) (Option 2)
1350 x 2000

W2-211-5n(B) (Option 3)
1350 x 2000

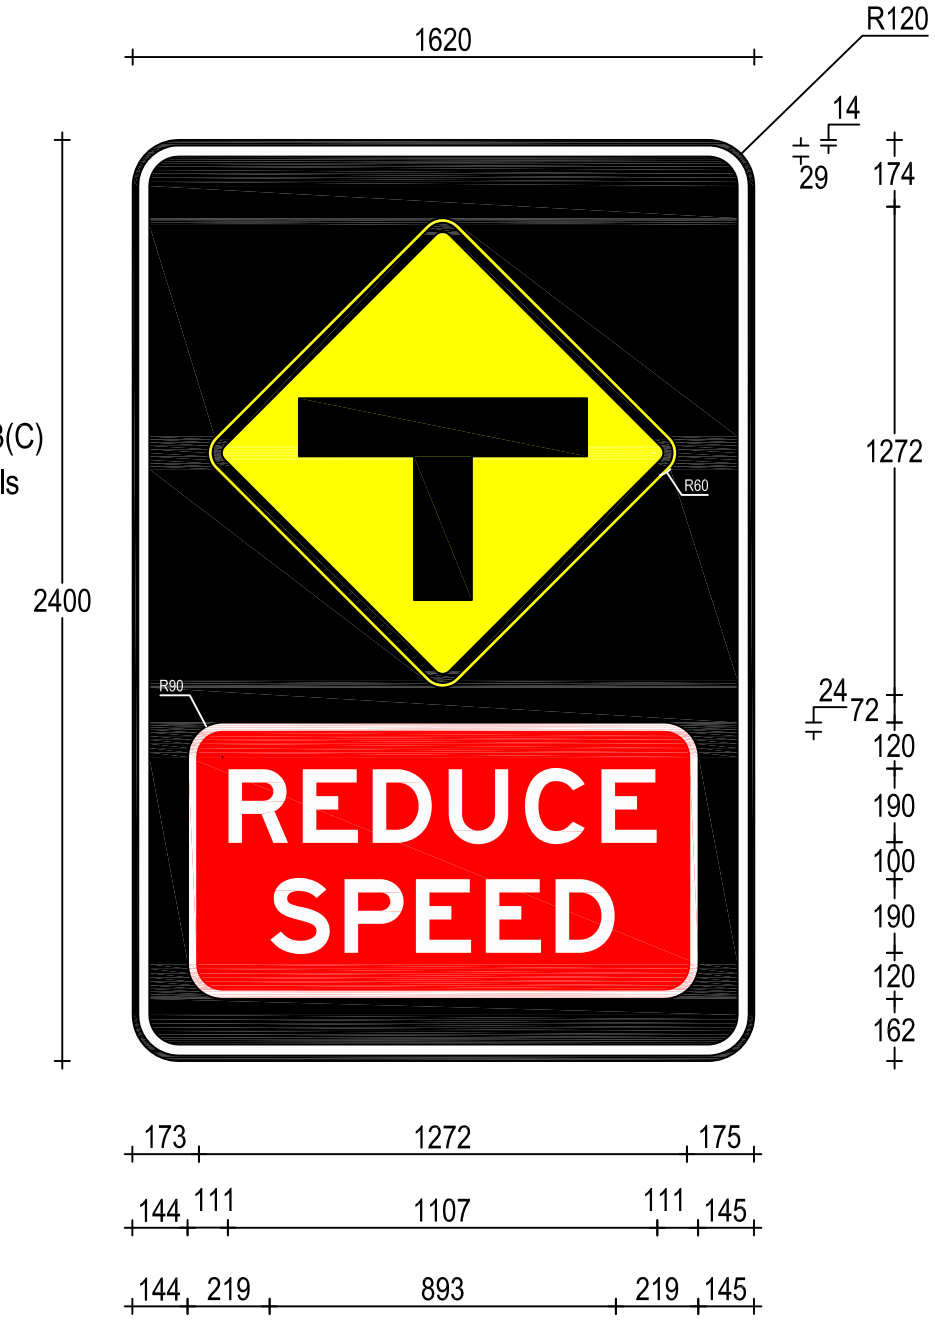

W2-211-3n(C) (Option 1)
1620 x 2400

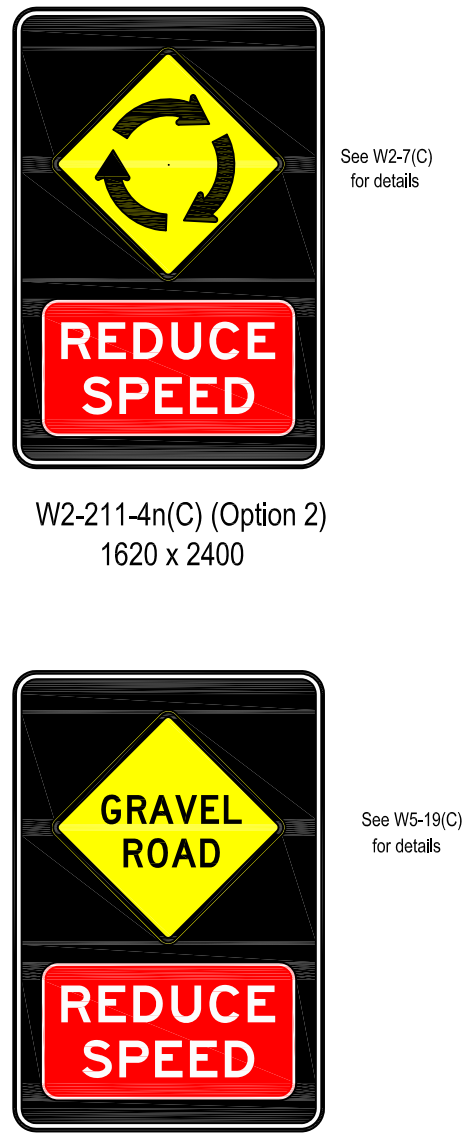

W2-211-4n(C) (Option 2)
1620 x 2400

W2-211-5n(C) (Option 3)
1620 x 2400

ACCEPTED FOR CONSTRUCTION

THIS DRAWING MAY BE PREPARED IN COLOUR AND MAY BE INCOMPLETE IF COPIED
50mm ON A3 SIZE ORIGINAL

QR CODE Scan to Check Document Version	REV	DATE	AMENDMENT / REVISION DESCRIPTION	APPROVAL
	01	23-08-18	AS Fonts & material classification revised	P.Oliver

DRAWING FILE LOCATION / NAME: H:\SIGNS\TTT\DRAWINGS\PLOT\WARN\W2-211-3N.DWG

MATERIALS: ALUMINIUM SIGN
CL.400 WHITE BDR ON BLACK GRD
WARNING SYMBOL: BLACK LEGEND /SYMBOL & BORDER
ON CL.400 YELLOW REFL GRD
REDUCE SPEED: CL400 WHITE REFL LGD /CL400 REFL RED GRD

ALL DIMENSIONS ARE IN MILLIMETRES UNLESS OTHERWISE SPECIFIED

SIGN TO BE MANUFACTURED IN ACCORDANCE WITH RMS QA SPECIFICATION 3400

DESIGNED
SIGNED
NAME M.Davies
DATE 31-07-19

REVIEWED
SIGNED
NAME J.Rozos
DATE 31-07-19

VERIFIED
SIGNED
NAME P.Oliver
TITLE Manager Guidance & Delineation
DATE 31-07-19

NSW GOVERNMENT Transport Roads & Maritime Services

PREPARED BY
GUIDANCE AND DELINEATION UNIT
TRAFFIC ENGINEERING SERVICES
TECHNICAL AND PROJECT SERVICES

WARNING SIGN

A3

W2-211-3N & W2-211-4N & W2-211-5N

REDUCE SPEED with T-JUNCTION or RABOUT or GRAVEL ROAD

SHEET 1 OF 1

SCALE: 1:25	EDMS No. XXXXXXXXX	SHEET No. 1	ISSUE 01

© Roads and Maritime Services