
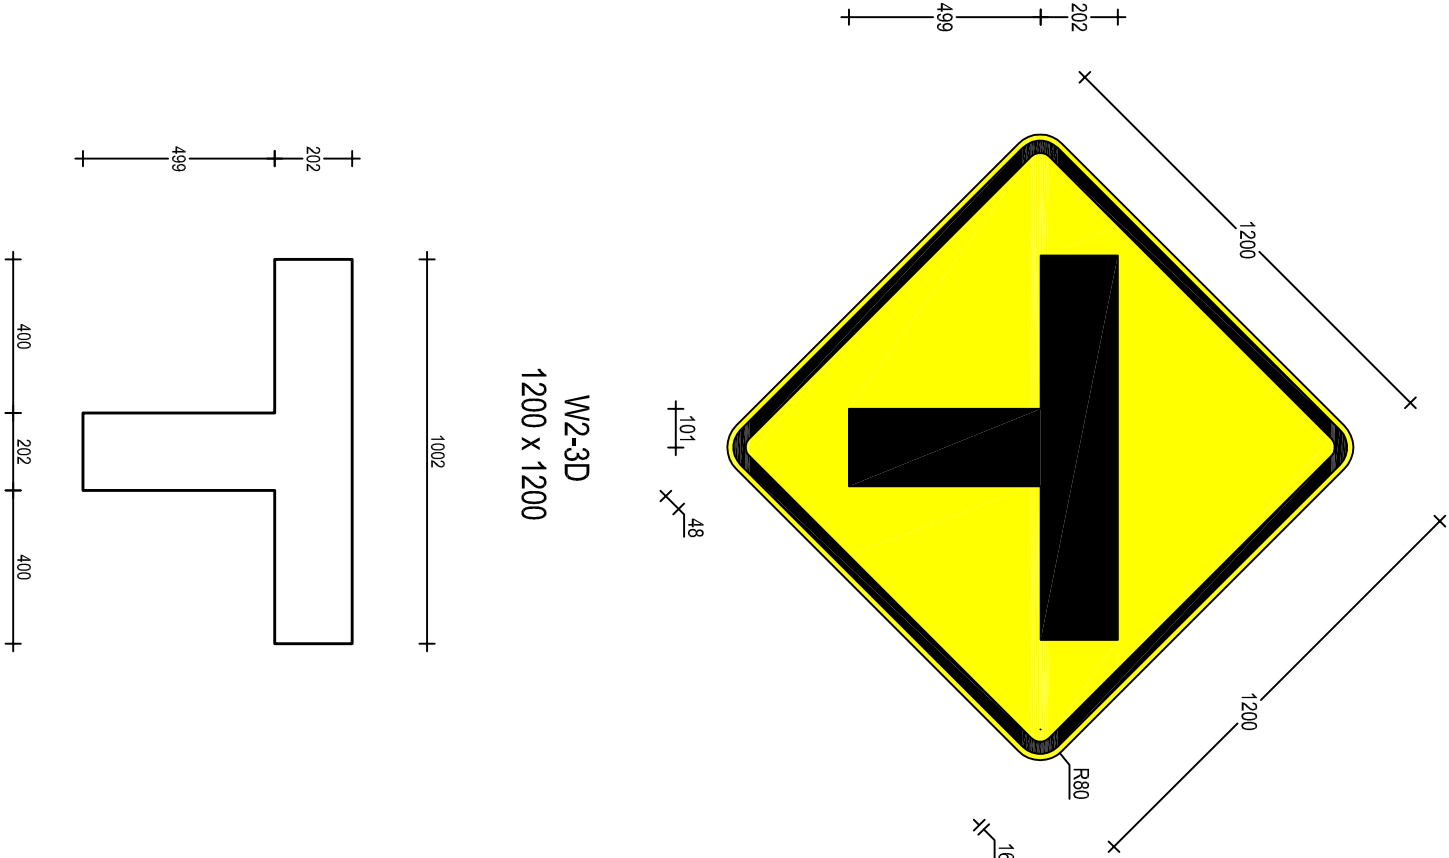
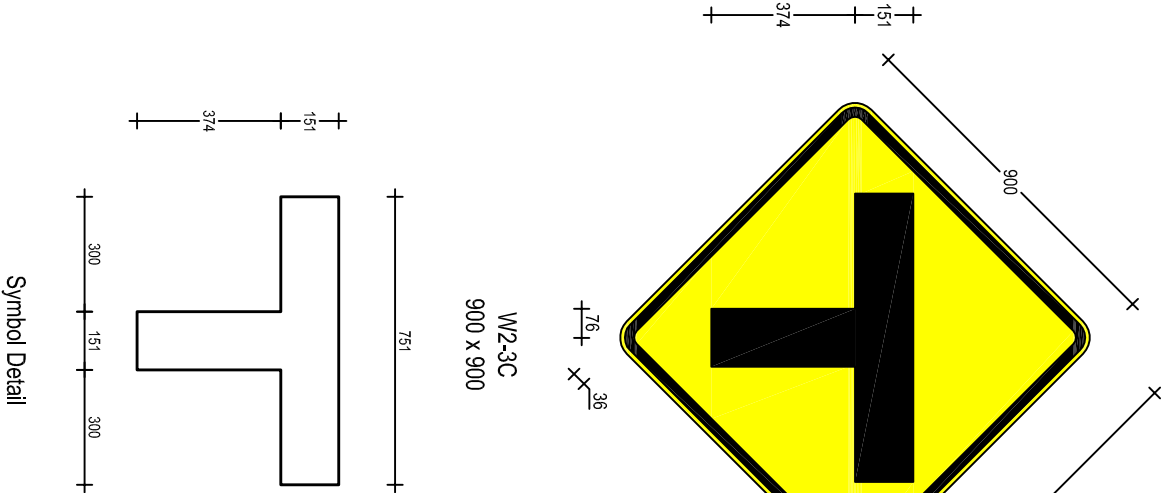
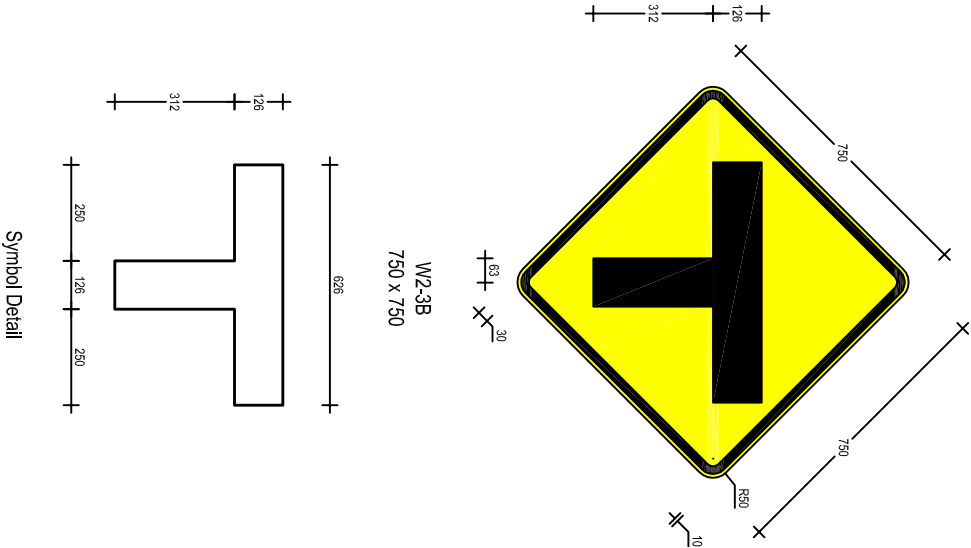


OR CODE	REVISION	REV	DATE	AMENDMENT / REVISION DESCRIPTION	APPROVAL	DRAWING FILE LOCATION / NAME: H:\SIGN\ITTDRAWINGS\PL\OTWANN\W2-3.DWG
	01	23-03-18		AS Forms & material classification revised	P. Oliver	
DRAWING FILE LOCATION / NAME: H:\SIGN\ITTDRAWINGS\PL\OTWANN\W2-3.DWG						
MATERIALS: ALUMINIUM SIGN BLACK SYMBOL AND BORDER ON AS1906.1 CL.400 YELLOW REFLECTORISED GROUND						
ALL DIMENSIONS ARE IN MILLIMETRES UNLESS OTHERWISE SPECIFIED						
SIGN TO BE MANUFACTURED IN ACCORDANCE WITH RMS QA SPECIFICATION 3400						
DESIGNED						
SIGNED:  NAME: M. Davies DATE: 31-07-19						
REVIEWED						
SIGNED:  NAME: J. Rozos DATE: 31-07-19						
VERIFIED						
SIGNED:  NAME: P. Oliver TITLE: Manager, Guidance & Definition DATE: 31-07-19						
PREPARED BY						
NSW GOVERNMENT Transport Roads & Maritime Services GUIDANCE AND DELINEATION UNIT TRAFFIC ENGINEERING SERVICES TECHNICAL AND PROJECT SERVICES						
WARNING SIGN						
W2-3 T-JUNCTION (Symbolic)						
SCALE: 1:20						
SHEET 1 OF 1						
EDMS N ^o . XXXXXXXXXX						
SHEET N ^o . 1						
ISSUE 01						
A3						

ACCEPTED FOR CONSTRUCTION

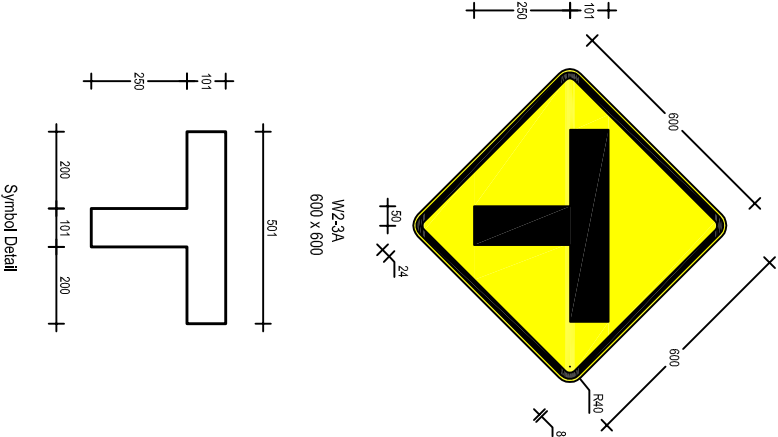

Symbol Detail