
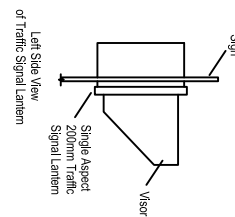
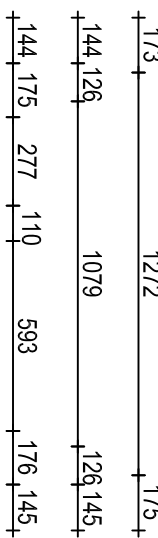
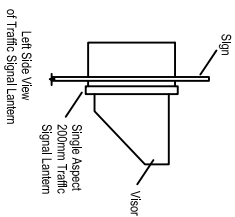
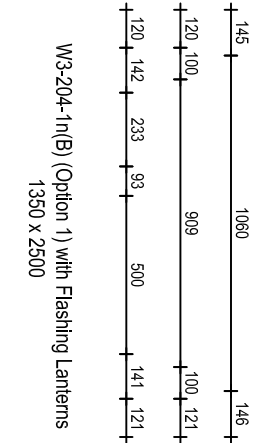
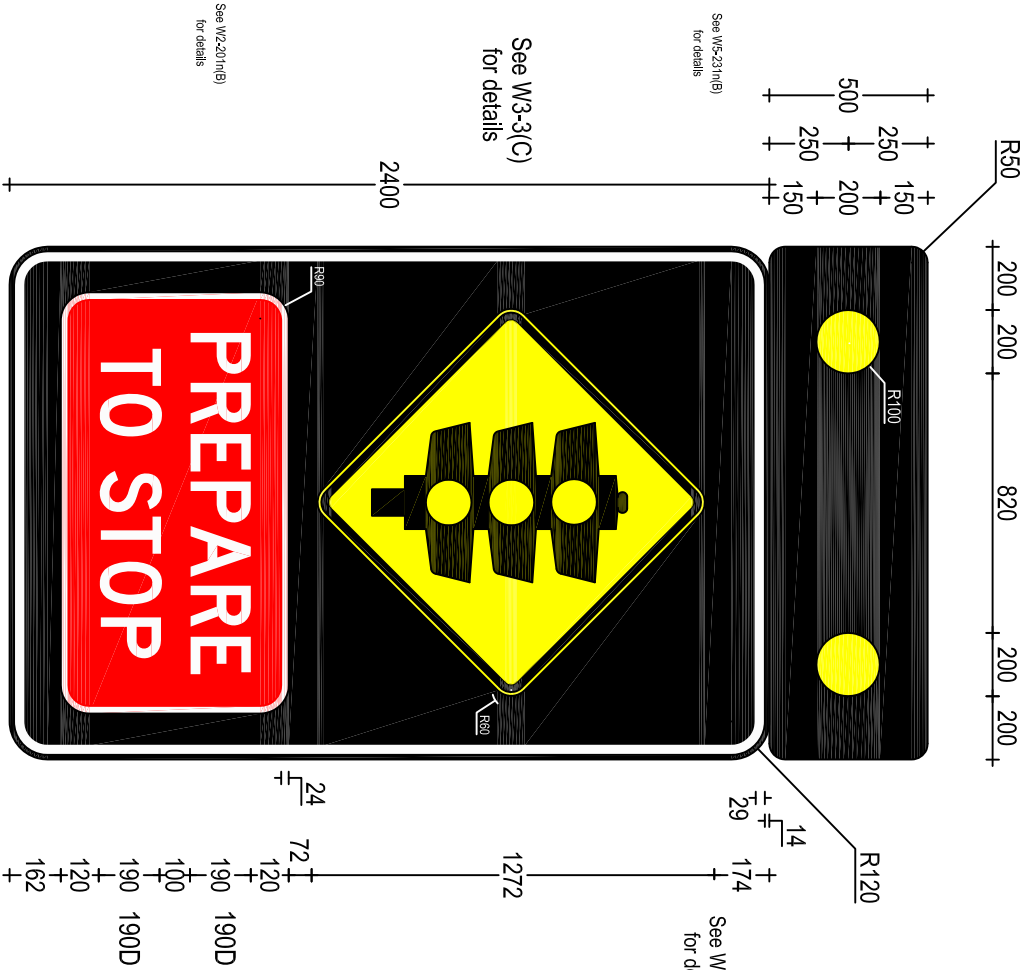


OR CODE Scan to Check Document Version	REV 01	DATE 22-05-18	AMENDMENT / REVISION DESCRIPTION AS Forms & material classification revised	APPROVAL P.Oliver	DRAWING FILE LOCATION / NAME H:\SIGNS\TITRADINGMS\PLOT\WARWIV-204-m2MG
DESIGNED					
SIGNED 					
NAME M.Davies					
DATE 12-07-19					
REVIEWED 					
SIGNED J. Rozos					
NAME					
DATE 12-07-19					
VERIFIED					
SIGNED 					
NAME P. Oliver					
TITLE Manager, Guidance & Delineation					
DATE 12-07-19					
 Transport Roads & Maritime Services GOVERNMENT					
PREPARED BY GUIDANCE AND DELINEATION TRAFFIC ENGINEERING SERVICES TECHNICAL AND PROJECT SERVICES					
WARNING SIGN					
W3-204-3N					
SHEET 1 OF 1					
PREPARE TO STOP					
QUEUED TRAFFIC(S) (Symbolic)					
SCALE: 1:20					
EDMS No. XXXXXXXXXX					
SHEET No. 1					
ISSUE 01					

ACCEPTED FOR CONSTRUCTION

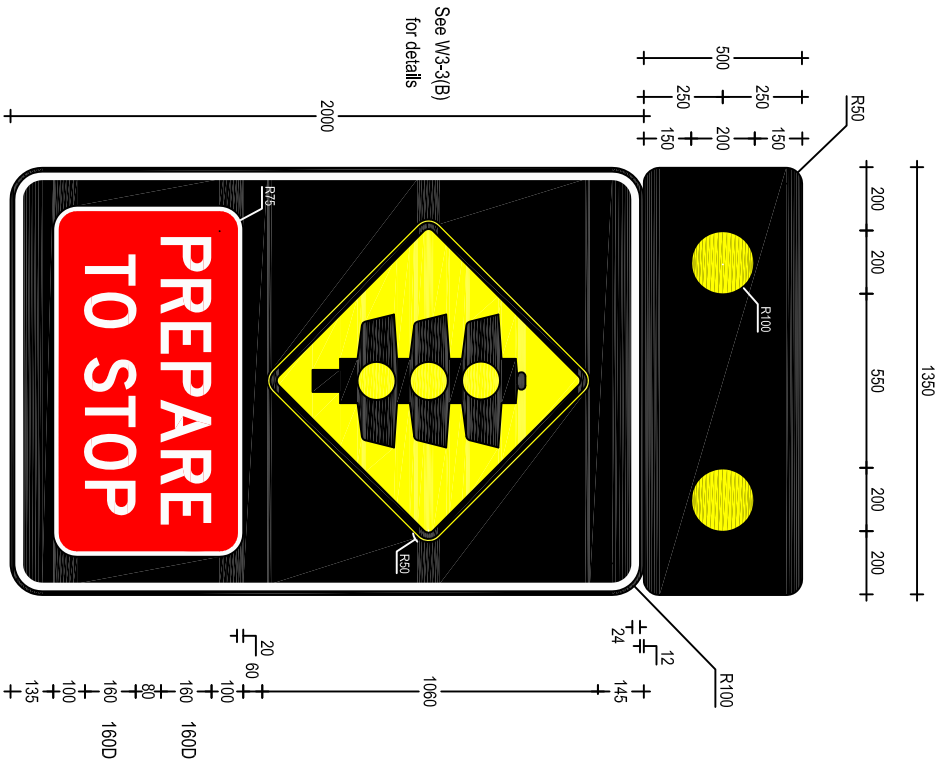

Note:- Lanterns to Flash alternately when amber/red is showing on traffic signals

W3-204-1n(C) (Option 1) with Flashing Lanterns
1620 x 2900

Note:- Lanterns to Flash alternately when amber/red is showing on traffic signals