


0510253035404550mm ON A3 SIZE ORIGINAL



OR CODE	Scan to Check Document Version	REV	DATE	AMENDMENT / REVISION DESCRIPTION	APPROVAL	DRAWING FILE LOCATION / NAME: H:\SIGNS\TTT\DRAWINGS\PI\OTWARR\W4-10.DWG	DESIGNED	VERIFIED	PREPARED BY	WARNING SIGN
		01	23-08-18	AS Forms & material classification revised	P. Oliver	MATERIALS: ALUMINIUM SIGN BLACK SYMBOL AND BORDER ON AS1906.1 CL.400 YELLOW REFLECTORISED GROUND	SIGNED:  NAME: M. Davies DATE: 31-07-19 REVIEWED:  NAME: J. Rozdos DATE: 31-07-19	SIGNED:  NAME: P. Oliver TITLE: Manager, Guidance & Delineation DATE: 31-07-19	TRANS NSW GOVERNMENT Roads & Maritime Services	W4-10 TWO LANES ON RIGHT (Symbolic)
ALL DIMENSIONS ARE IN MILLIMETRES UNLESS OTHERWISE SPECIFIED						SIGN TO BE MANUFACTURED IN ACCORDANCE WITH RMS QA SPECIFICATION 3400	SCALE: 1:15			
					SHEET 1 OF 1		EDMS No.	XXXXXXXXXX	SHEET No.	1
					ISS		0			

ACCEPTED FOR CONSTRUCTION


Symbol Detail

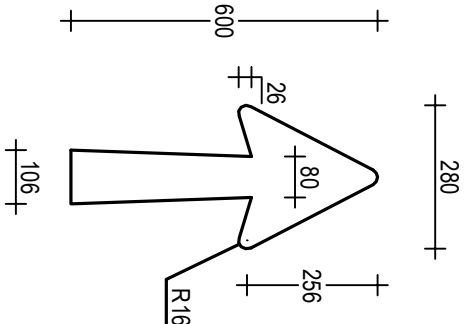

W4-10n(D)
1200x 1200

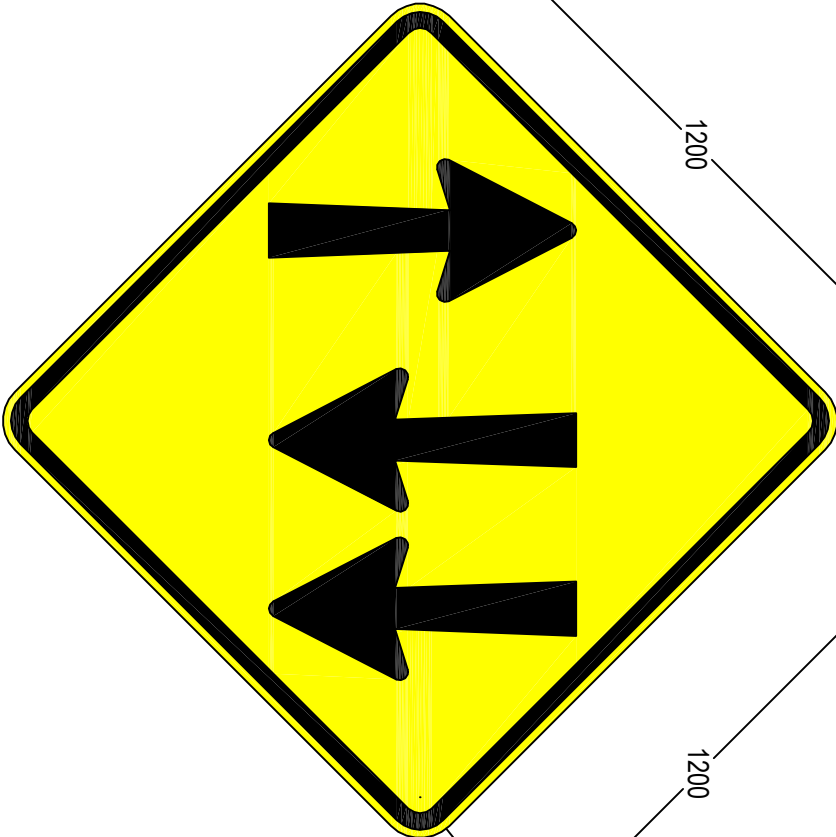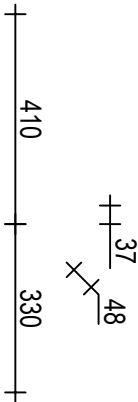


304
296

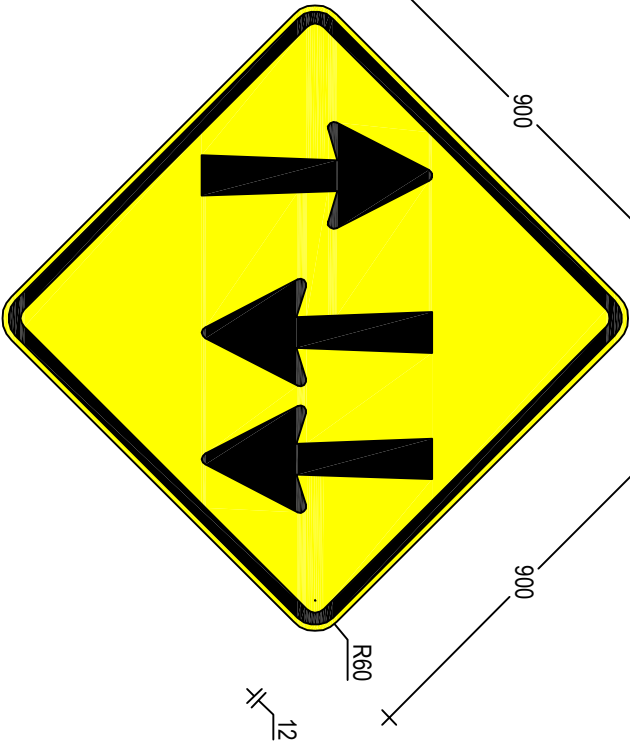


36
28

307
247

W4-10C
900 x 900

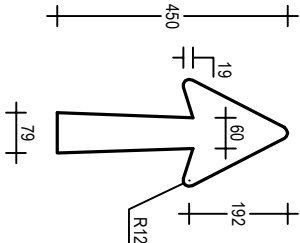


Symbol Detail

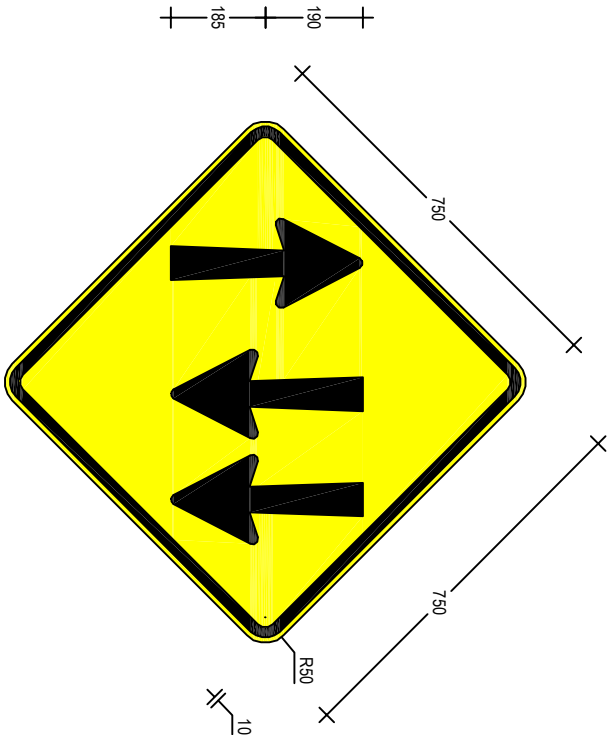

30
23
256
206

W4-10B
750 x 750

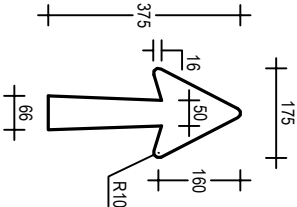

Symbol Detail