


50mm ON A3 SIZE ORIGINAL

OR CODE	Scan to Check Document Version	REV	DATE	AMENDMENT / REVISION DESCRIPTION	APPROVAL	DRAWING FILE LOCATION / NAME: H:\SIGNS\TTT\DRAWINGS\PL\CT\WARRW4-205N.DWG
		01	23-08-18	AS Fonts & material classification revised	P. Oliver	
ALL DIMENSIONS ARE IN MILLIMETRES UNLESS OTHERWISE SPECIFIED						
SIGN TO BE MANUFACTURED IN ACCORDANCE WITH RMS QA SPECIFICATION 3400						

DESIGNED	
SIGNED	
NAME	M. Davies
DATE	31-07-19
REVIEWED	
SIGNED	J. Rozdos
NAME	J. Rozdos
DATE	31-07-19

VERIFIED	
SIGNED	
NAME	P. Oliver
TITLE	Manager, Guidance & Delineation
DATE	31-07-19

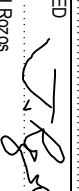

NSW
GOVERNMENT



Transport
Roads & Maritime
Services

PREPARED BY
GUIDANCE AND DELINEATION UNIT
TRAFFIC ENGINEERING SERVICES
TECHNICAL AND PROJECT SERVICES

WARNING SIGN

W4-205n

S-LANE (Symbolic)

SCALE: 1:15



EDMS No. XXXXXXXXXX

SHEET No. 1

ISS 0

SHEET 1 OF 1

ACCEPTED FOR CONSTRUCTION

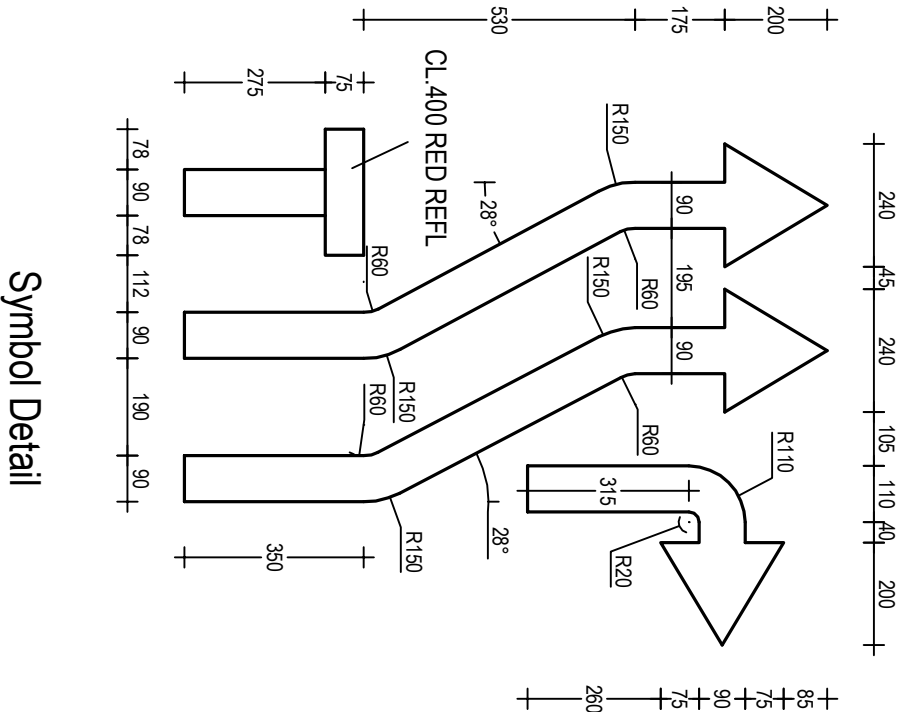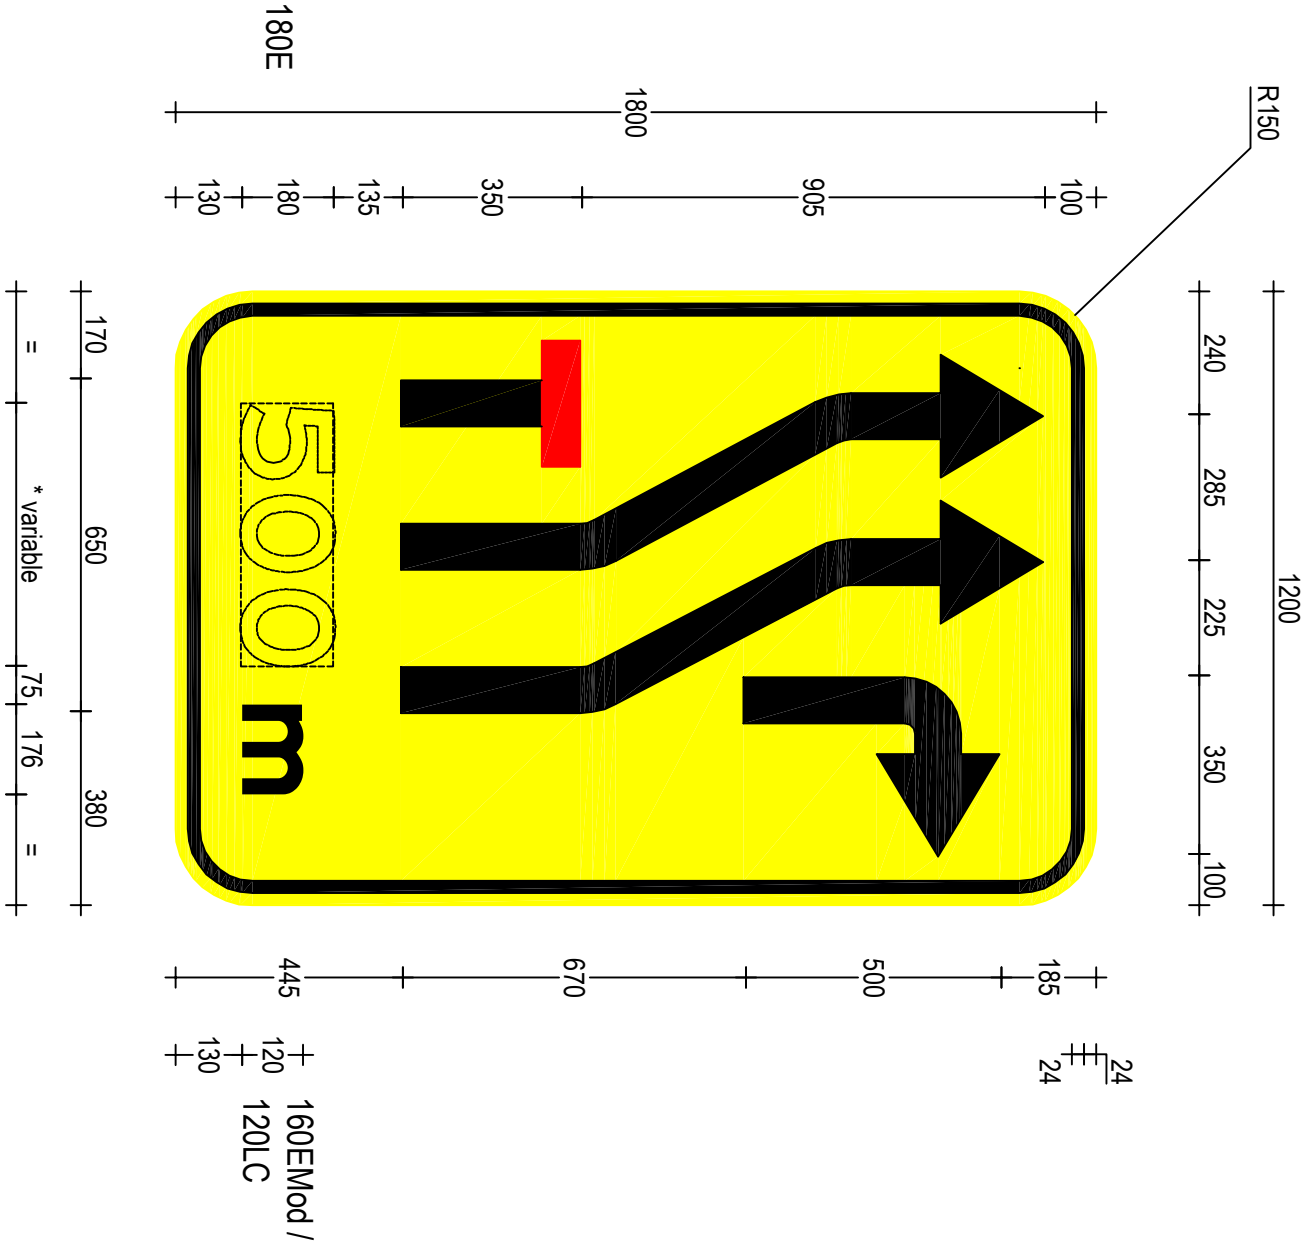

Symbol Detail