
 


05101520253035404550mm ON A3 SIZE ORIGINAL

OR CODE	Scan to Check Document Version	REV	DATE	AMENDMENT / REVISION DESCRIPTION	APPROVAL	DRAWING FILE LOCATION / NAME: H:\SIGNS\TTT\DRAWINGS\PI\OTWARR\W5-234\DWG
		01	23-08-18	AS Fonts & material classification revised	P Oliver	
ALL DIMENSIONS ARE IN MILLIMETRES UNLESS OTHERWISE SPECIFIED						
SIGN TO BE MANUFACTURED IN ACCORDANCE WITH RMS QA SPECIFICATION 3400						
MATERIALS: ALUMINIUM SIGN BLACK LEGEND AND BORDER ON AS1906.1 CL 400 YELLOW REFLECTORISED GROUND						
DESIGNED		SIGNED 				
NAME: M. Davies		SIGNED 				
DATE: 31-07-19		NAME: P Oliver				
REVIEWED		TITLE: Manager Guidance & Delineation				
SIGNED 		DATE: 31-07-19				
NAME: J. Rozos		DATE: 31-07-19				
 Transport Roads & Maritime Services PREPARED BY GUIDANCE AND DELINEATION UNIT TRAFFIC ENGINEERING SERVICES TECHNICAL AND PROJECT SERVICES						
WARNING SIGN W5-234N WATCH FOR HEAVY VEHICLES						A
SHEET 1 OF 1						
SCALE: 1:10				EDMS No XXXXXXXXXX	SHEET No. 1	ISS 0
© Roads and Maritime Service						

ACCEPTED FOR CONSTRUCTION

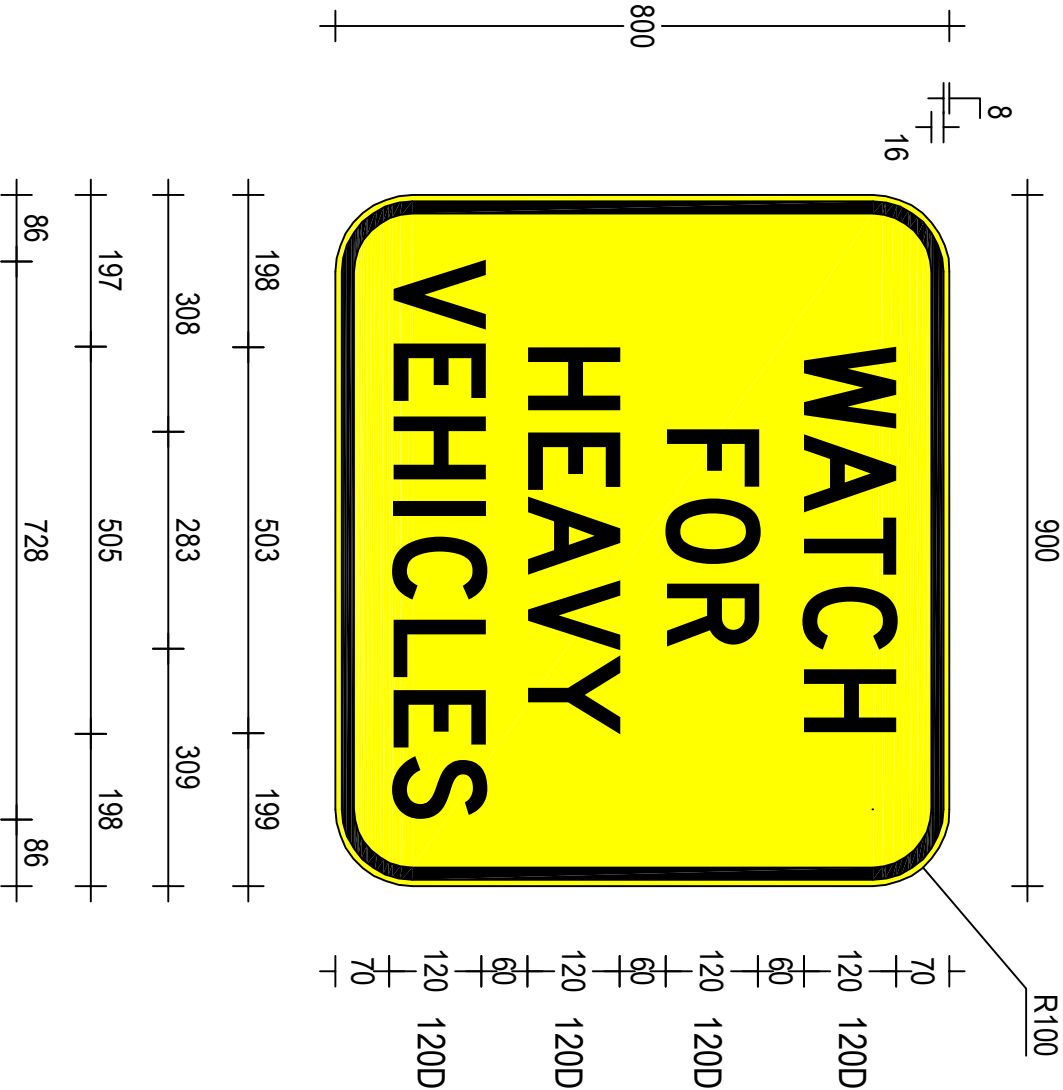

W5-234n
900 x 800