


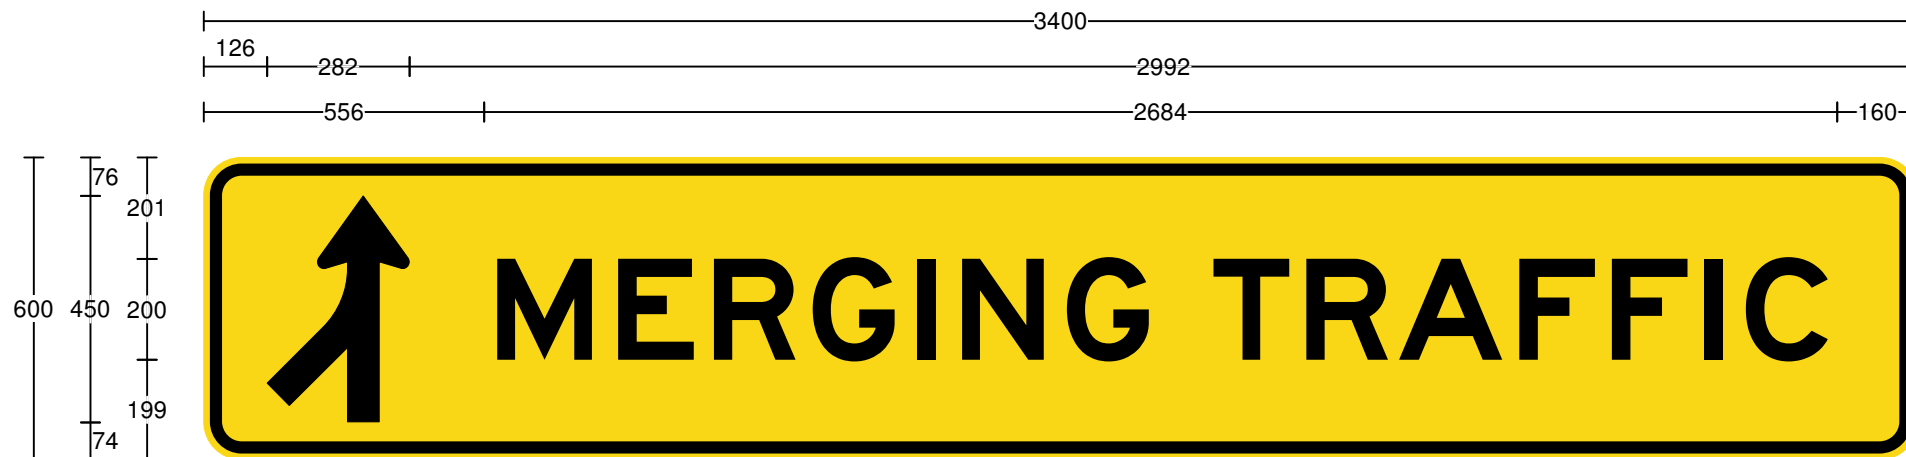

Legend

MERGING TRAFFIC

Font Type

FHWA Series E2000EX

Font Size

200

Specifications:
BACKLIT SIGN
Black lgd
Yellow grd

Size:	600 x 3400	Date:	27/9/19
Area:	2.04 sq.m	Scale:	1:15
Border:	12 x 24	Drawn:	RozosJ
Cnr Rad:	75	Checked:	
Patch CR:	NA	File:	W5-34-1n(L)
 Transport Roads & Maritime Services		Path:	H:\Signs\Standard_Signs & Symbols\Tunnel Signs\New Tunnel Signs
Prepared using TraSiCAD Product of QMR		Guidance & Delineation Team Traffic Engineering Services Technical & Project Services 99 Phillip St Parramatta NSW 2150	W5-34-1n(L)