
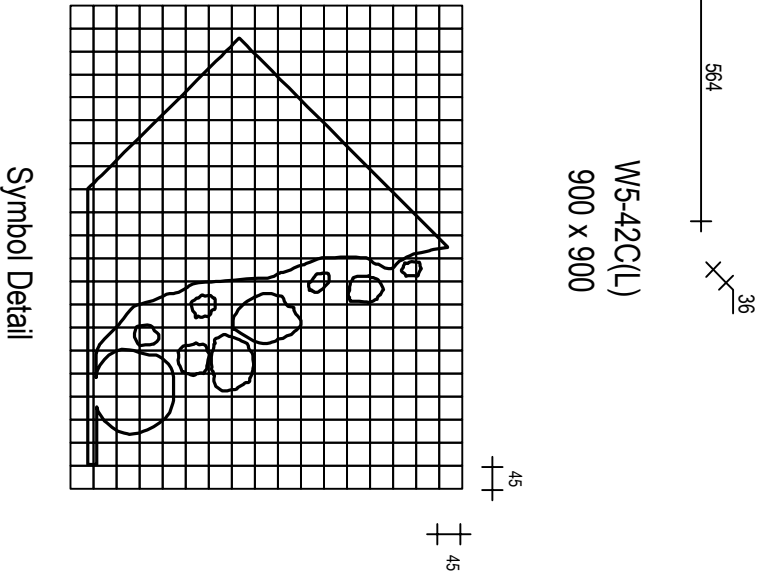
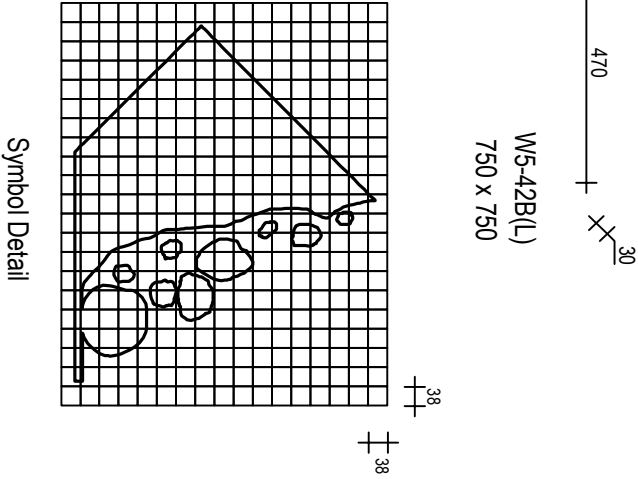
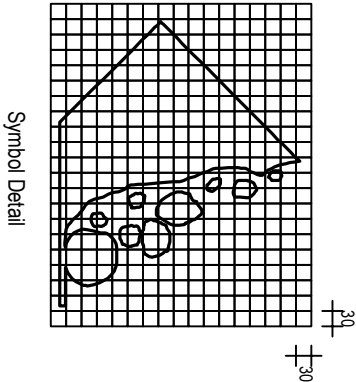


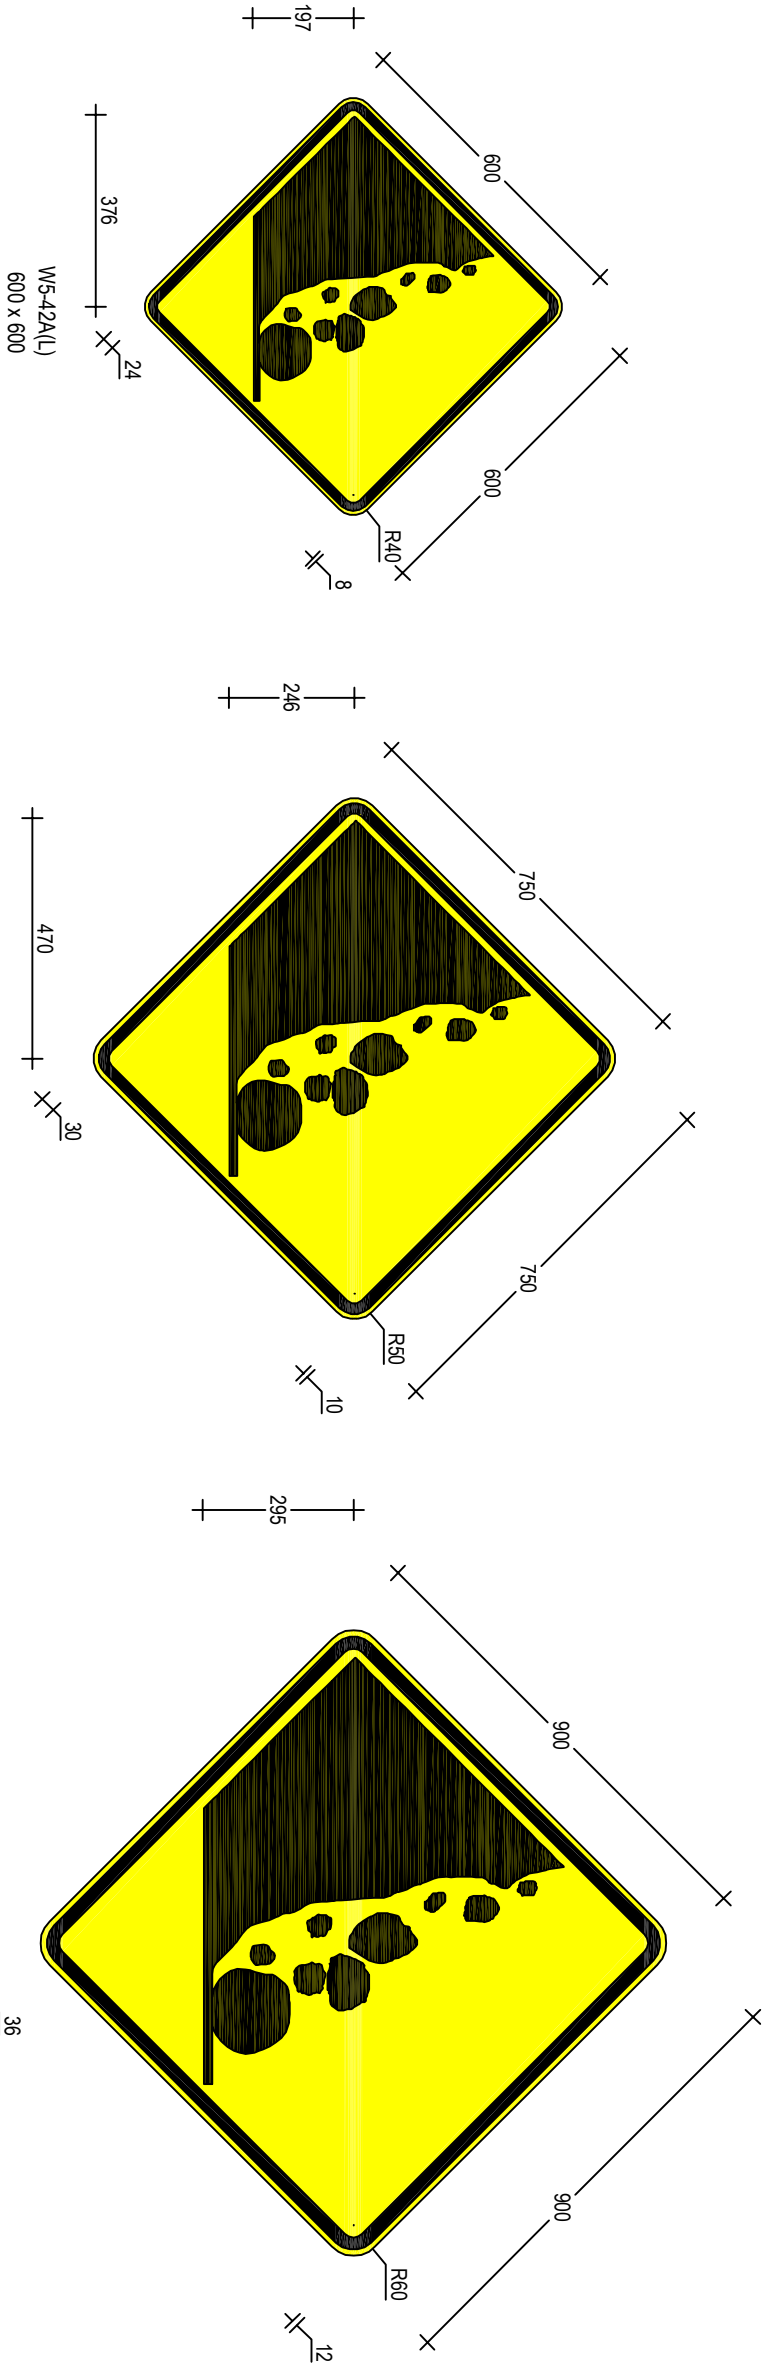

ACCEPTED FOR CONSTRUCTION