

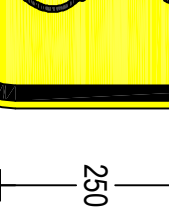


OR CODE	Scan to Check Document Version	REV	DATE	AMENDMENT / REVISION DESCRIPTION	APPROVAL	DRAWING FILE LOCATION / NAME: H:\SIGN\STTT\DRAWINGS\PI\OT\WARRW6-213N.DWG
		01	23-08-18	AS Fonts & material classification revised	P Oliver	
ALL DIMENSIONS ARE IN MILLIMETRES UNLESS OTHERWISE SPECIFIED						
SIGN TO BE MANUFACTURED IN ACCORDANCE WITH RMS QA SPECIFICATION 3400						
DESIGNED						
SIGNED: 						
NAME: M. Davies						
DATE: 31-07-19						
REVIEWED						
SIGNED: 						
NAME: J. Rozos						
DATE: 31-07-19						
VERIFIED						
SIGNED: 						
NAME: P. Oliver						
TITLE: Manager, Guidance & Delineation						
DATE: 31-07-19						
PREPARED BY						
GUIDANCE AND DELINEATION UNIT						
TRAFFIC ENGINEERING SERVICES						
TECHNICAL AND PROJECT SERVICES						
WARNING SIGN						
W6-213N						
BEWARE CYCLISTS (Symbolic)						
SCALE: 1:10						
EDMS No. XXXXXXXXXX						
SHEET No. 1						
ISS 0						
SHEET 1 OF 1						
A						

ACCEPTED FOR CONSTRUCTION

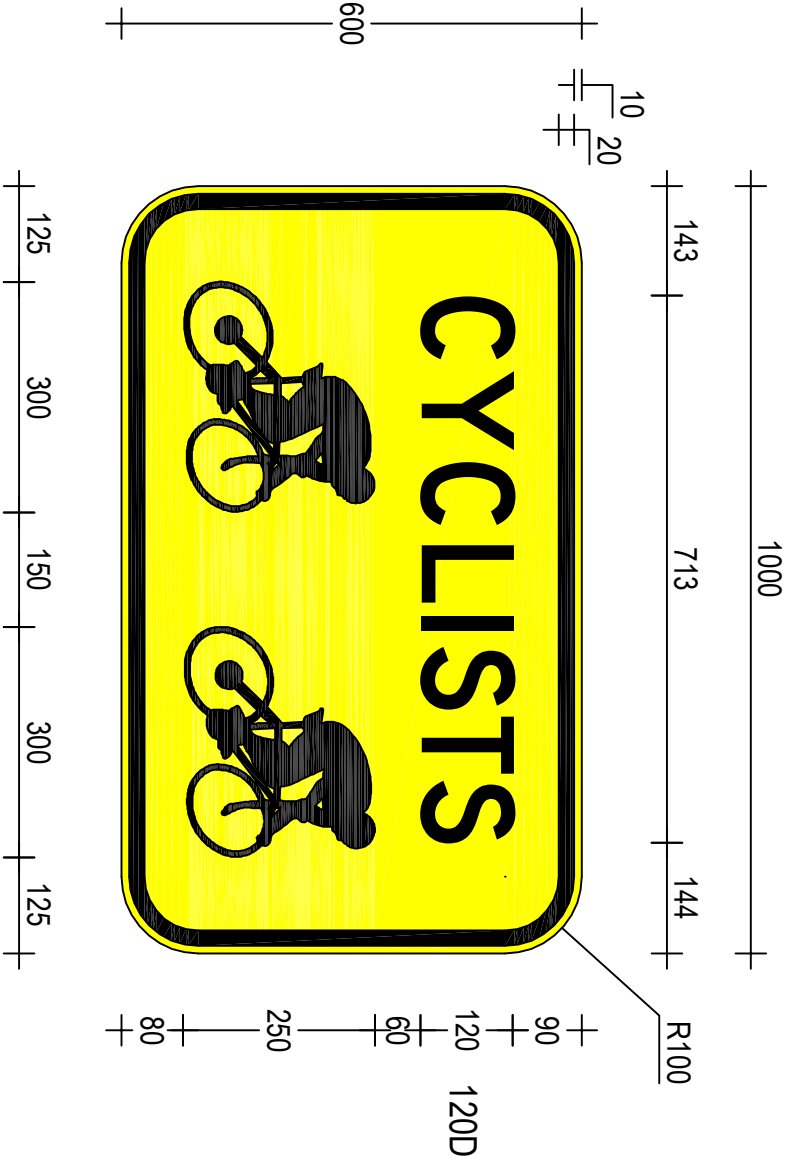

W6-213N
1000 x 600

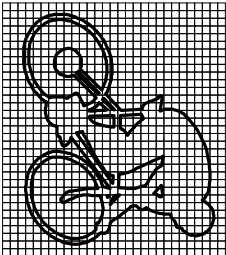

Symbol Detail