
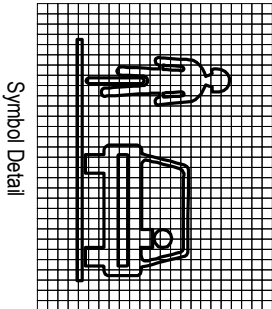



0 5 10 15 20 25 30 35 40 45 50mm ON A3 SIZE ORIGINAL

OR CODE	Scan to Check Document Version	REV	DATE	AMENDMENT / REVISION DESCRIPTION	APPROVAL	DRAWING FILE LOCATION / NAME: H:\SIGNS\TTT\DRAWINGS\PI\OTWARRW6-214NDWG	DESIGNED	VERIFIED	 Transport Roads & Maritime Services PREPARED BY GUIDANCE AND DELINEATION UNIT TRAFFIC ENGINEERING SERVICES TECHNICAL AND PROJECT SERVICES	WARNING SIGN W6-214N SHARE THE ROAD(Symbolic)	A			
		01	23-08-18	AS Fonts & material classification revised	P. Oliver		SIGNED: M. Davies NAME: 31-07-19 DATE: 31-07-19 SIGNED: J. Rozdos NAME: 31-07-19 DATE: 31-07-19	SIGNED: P. Oliver NAME: Manager, Guidance & Delineation TITLE: 31-07-19 DATE: 31-07-19		SCALE: 1:15	EDMS No. XXXXXXXXXX	SHEET No. 1	ISS 0	
ALL DIMENSIONS ARE IN MILLIMETRES UNLESS OTHERWISE SPECIFIED						SIGN TO BE MANUFACTURED IN ACCORDANCE WITH RMS QA SPECIFICATION 3400						SHEET 1 OF 1		


ACCEPTED FOR CONSTRUCTION

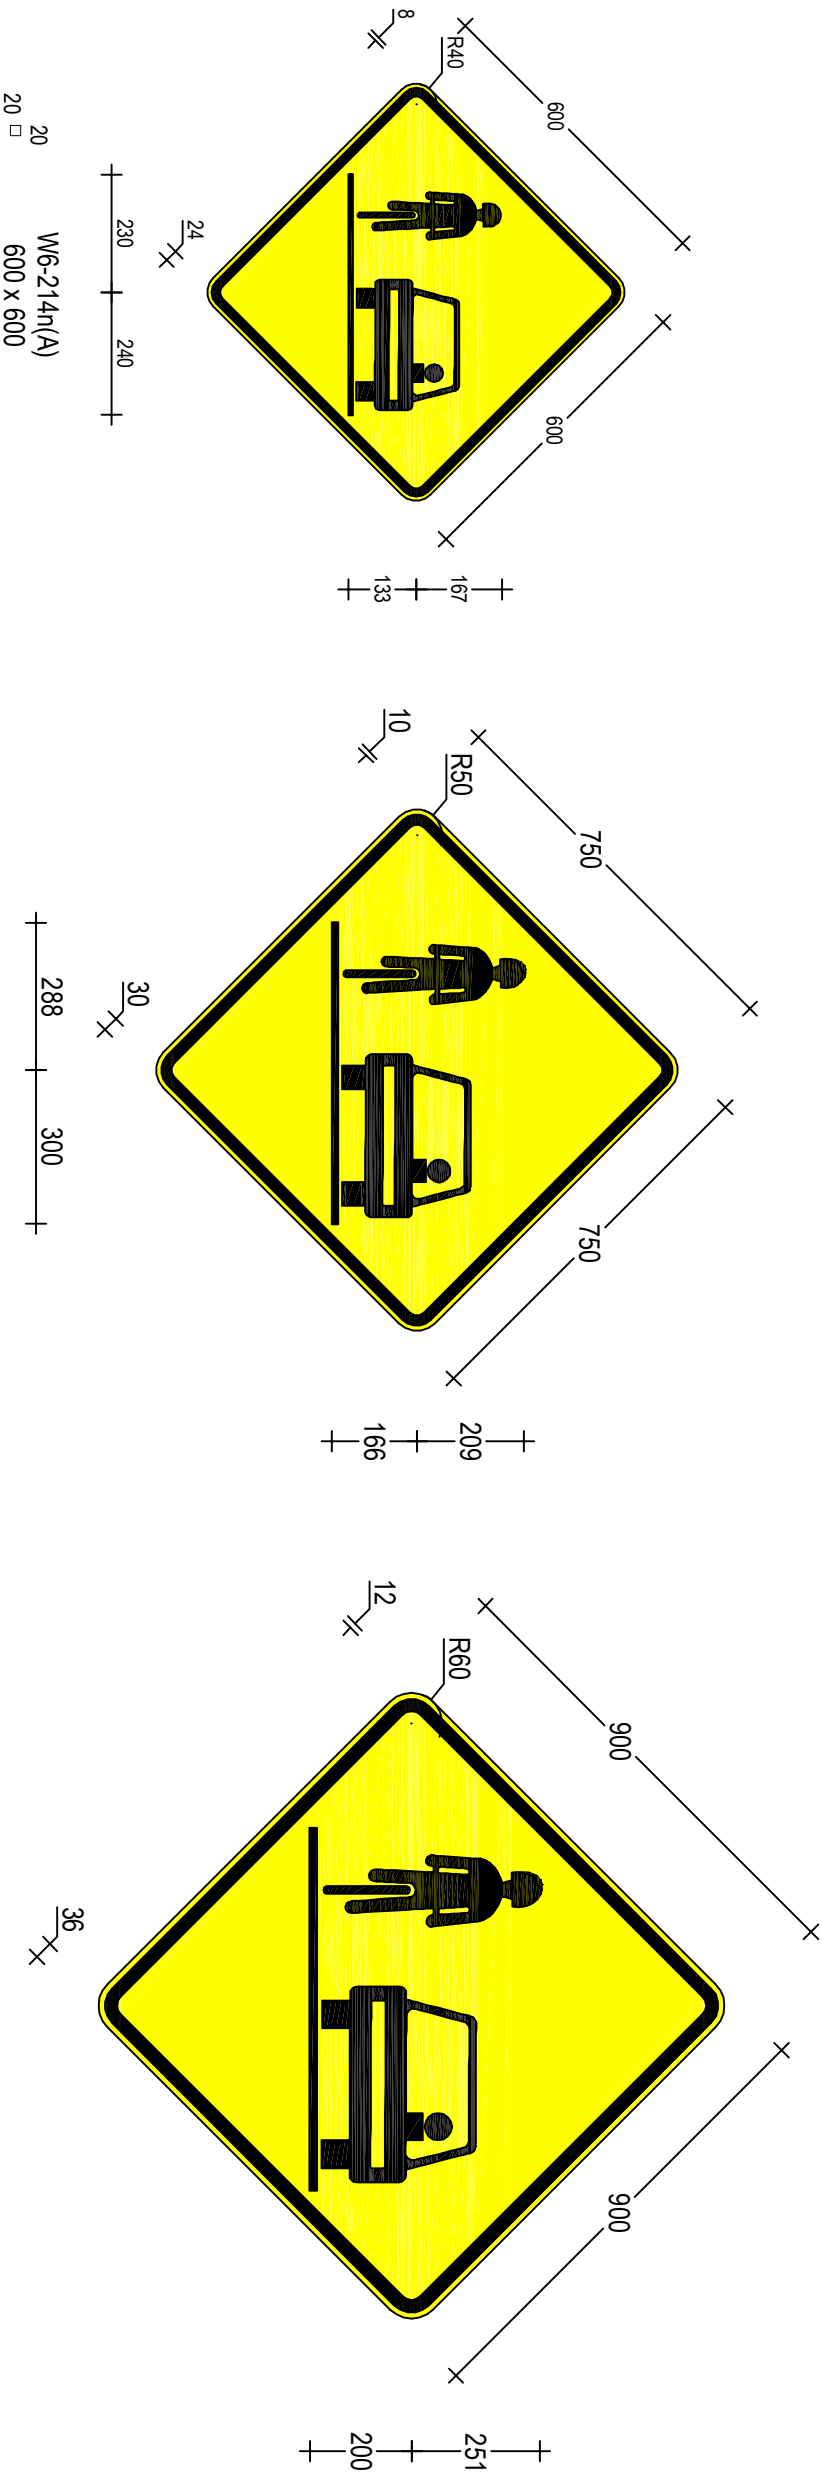

Symbol Detail

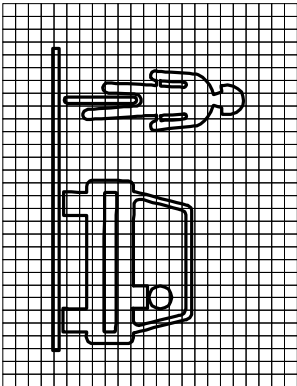

Symbol Detail

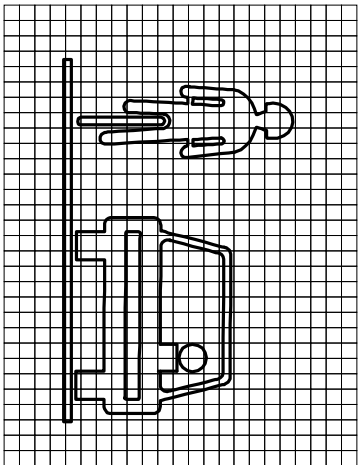

Symbol Detail