
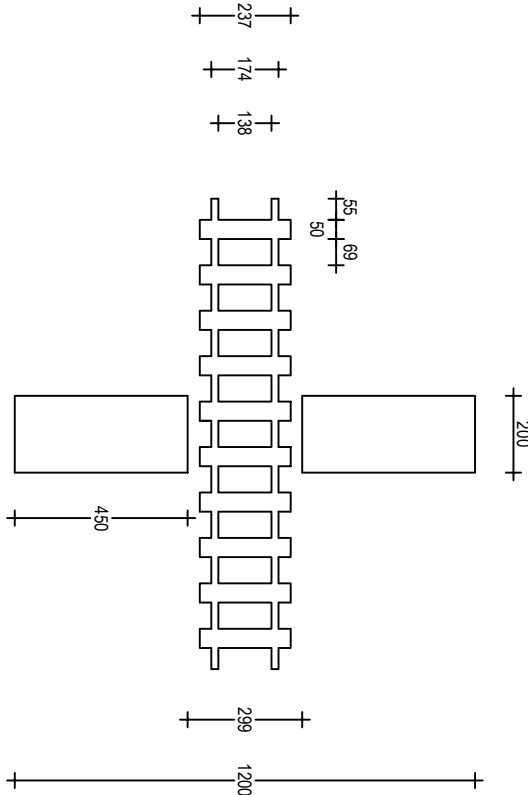
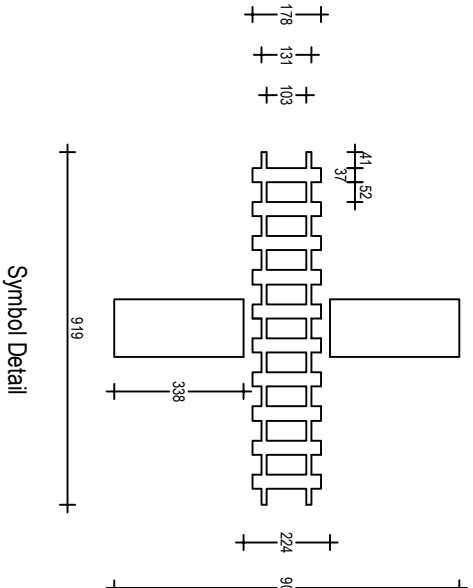
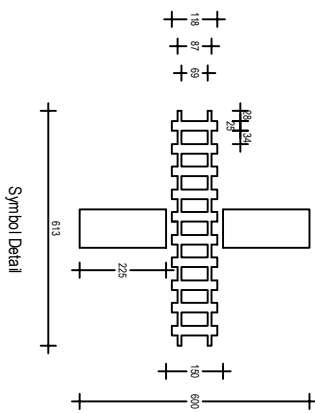
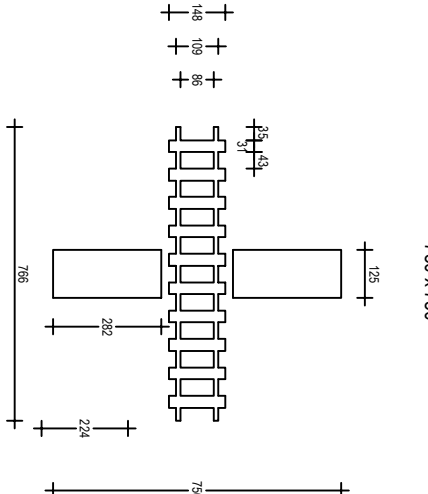
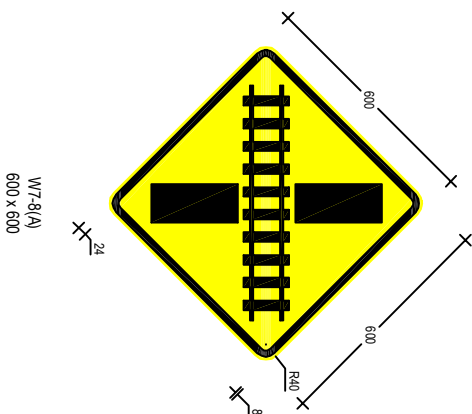
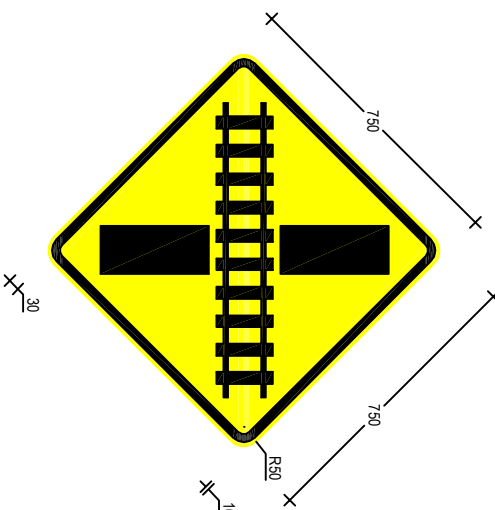
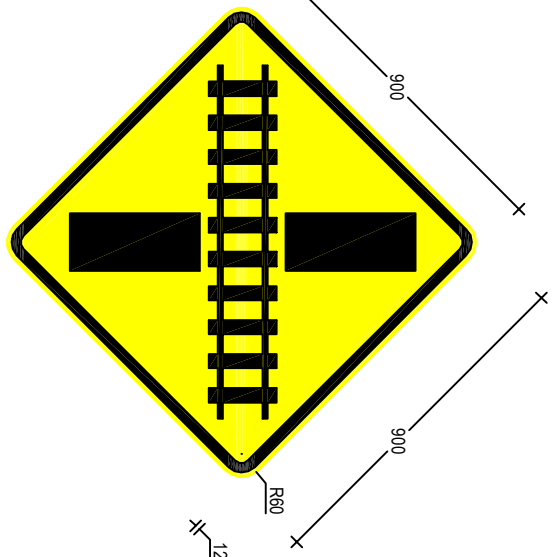


0	5	10	15	20	25	30	35	40	45
ALL DIMENSIONS ARE IN MILLIMETRES UNLESS OTHERWISE SPECIFIED									
OR CODE		Scan to Check Document Version		REV	DATE	AMENDMENT / REVISION DESCRIPTION			APPROVAL
		01		23-08-18		AS Form & material classification revised			P. Oliver
DRAWING FILE LOCATION / NAME: H:\SIGNS\TTT\DRAWINGS\PI\OTWARR\W7-8.DWG									
MATERIALS: ALUMINIUM SIGN BLACK SYMBOL AND BORDER ON AS1906.1 CL.400 YELLOW REFLECTORISED GROUND									
DESIGNED		SIGNED		NAME		M. Davies			
DATE		31-07-19		NAME		P. Oliver			
REVIEWED		SIGNED		NAME		J. Rozdos			
DATE		31-07-19		TITLE		Manager, Guidance & Delineation			
VERIFIED		SIGNED		NAME		P. Oliver			
DATE		31-07-19		TITLE		Manager, Guidance & Delineation			
PREPARED BY		GUIDANCE AND DELINEATION UNIT		TRAFFIC ENGINEERING SERVICES		TECHNICAL AND PROJECT SERVICES			
WARNING SIGN		W7-8		RAILWAY LEVEL CROSSING		(Symbolic Right Angle)		SHEET 1 OF 1	
SCALE: 1:20		EDMS No.		XXXXXXXXXX		SHEET No.		1	
								0	

ACCEPTED FOR CONSTRUCTION

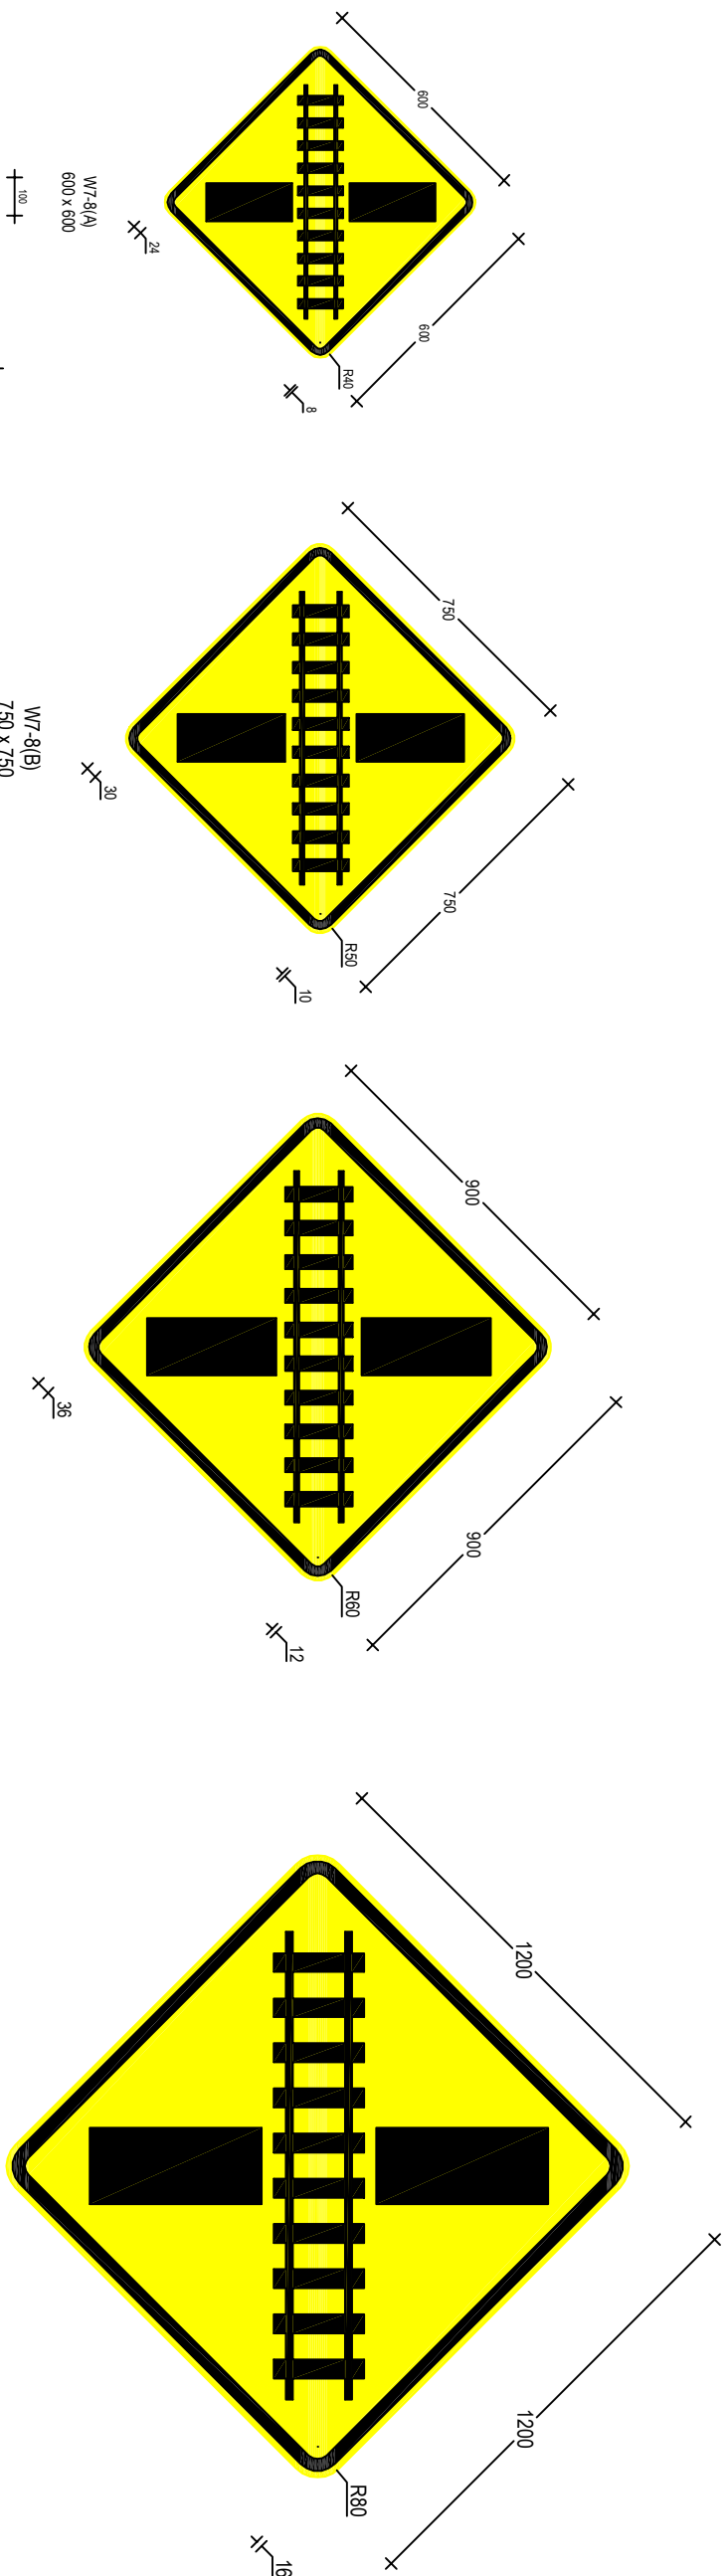

Symbol Detail