




51020253035404550mm ON A3 SIZE ORIGINAL

OR CODE		Scan to Check Document Version		REV	DATE	AMENDMENT / REVISION DESCRIPTION		APPROVAL		DRAWING FILE LOCATION / NAME: H:\SIGNS\TTP\DRAWINGS\SP\CTWARRW7-9.DWG	
				01	23-08-18	AS Fonts & material classification revised		P Oliver		MATERIALS: ALUMINIUM SIGN BLACK LEGEND AND BORDER ON AS1906.1 CL.400 YELLOW REFLECTORISED GROUND	
ALL DIMENSIONS ARE IN MILLIMETRES UNLESS OTHERWISE SPECIFIED											
SIGN TO BE MANUFACTURED IN ACCORDANCE WITH RMS QA SPECIFICATION 3400											
DESIGNED						VERIFIED					
SIGNED:  NAME: M. Davies DATE: 31-07-19						SIGNED:  NAME: P. Oliver TITLE: Manager, Guidance & Delineation DATE: 31-07-19					
REVIEWED:  NAME: J. Rozdos DATE: 31-07-19						PREPARED BY:  Transport Roads & Maritime Services GUIDANCE AND DELINEATION UNIT TRAFFIC ENGINEERING SERVICES TECHNICAL AND PROJECT SERVICES					
WARNING SIGN W7-9(L) RAIL TRACK CROSSING (Symbolic Left)						SCALE: 1:20					
EDMS No. XXXXXXXXXX						SHEET No. 1					
ISS 0						SHEET 1 OF 1					



ACCEPTED FOR CONSTRUCTION

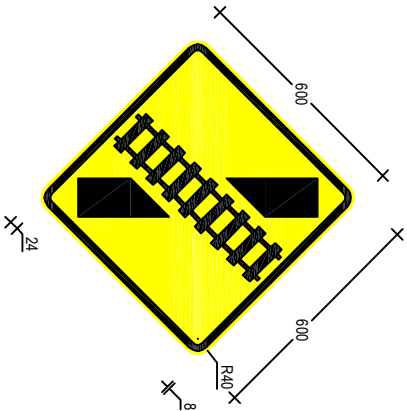



W7-9L(A)
600 x 600

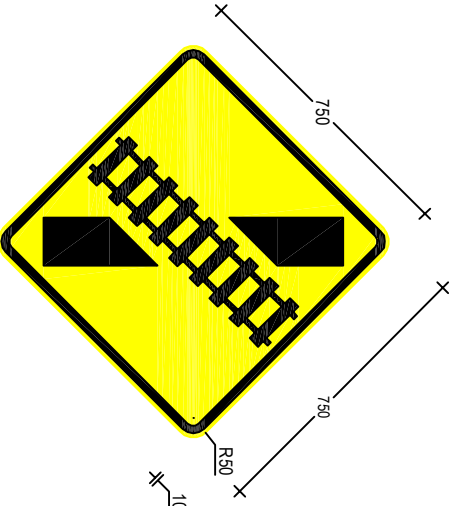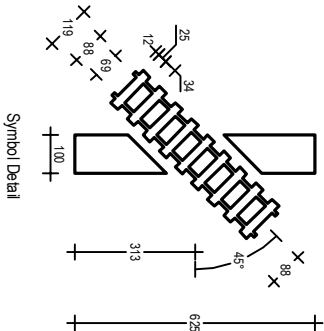


W7-9L(B)
750 x 750

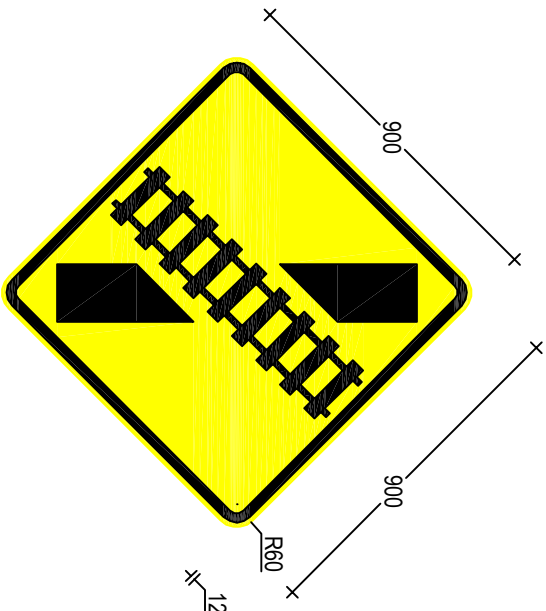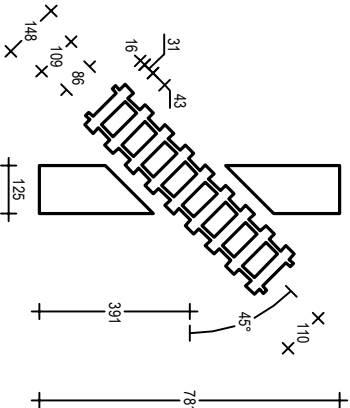

W7-9L(C)
900 x 900

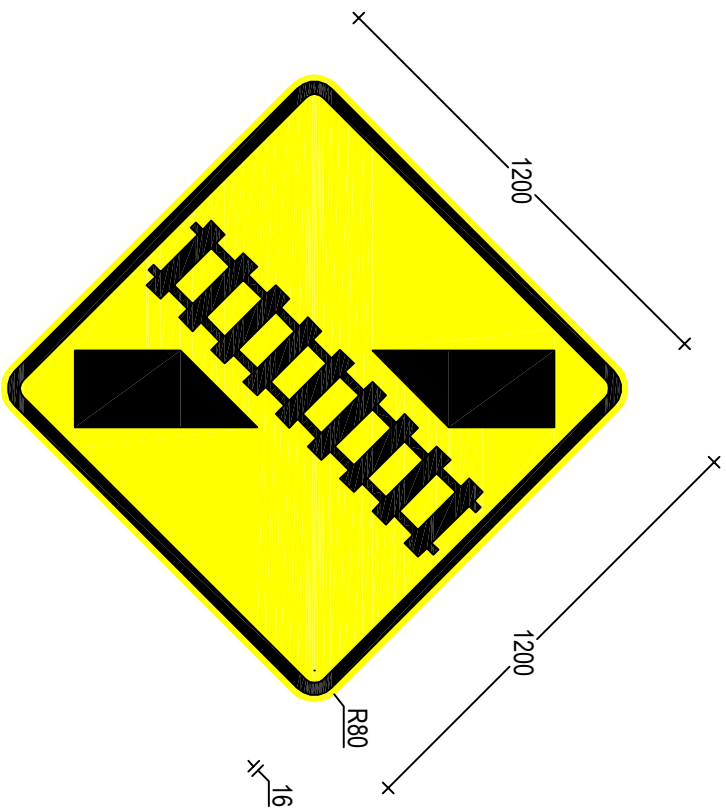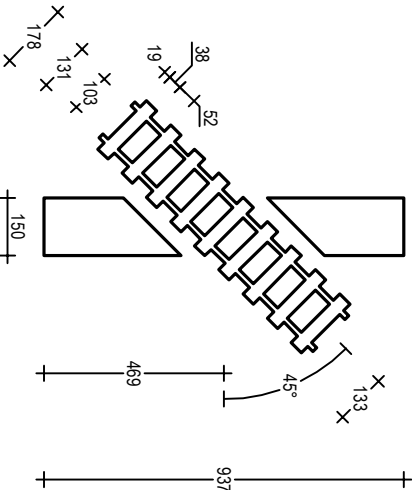

W7-9Ln(D)
1200 x 1200

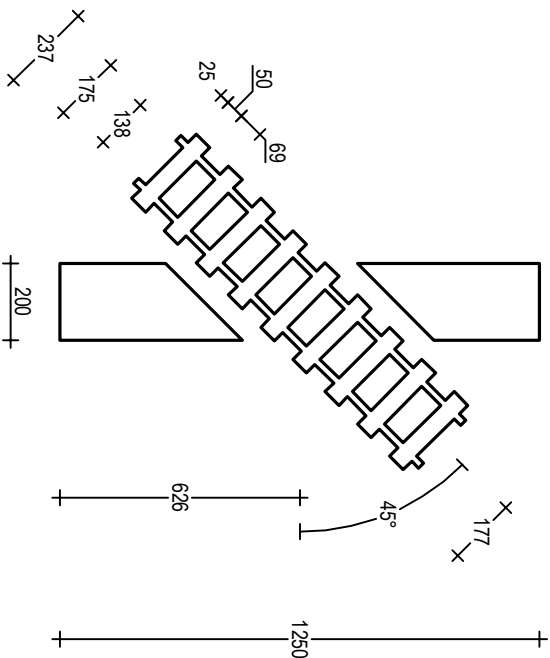

Symbol Detail