

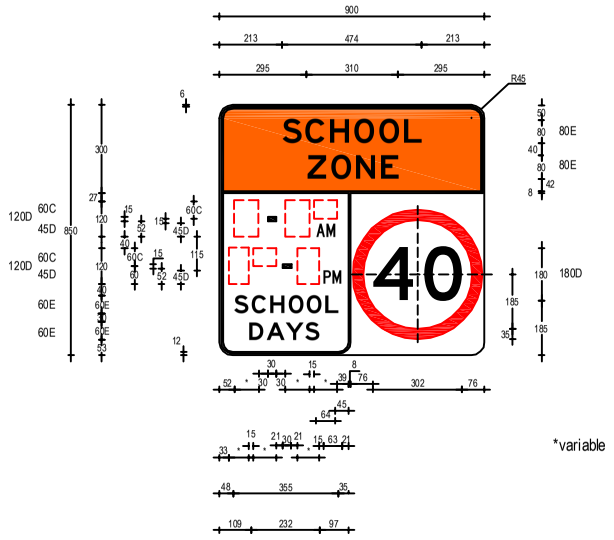


R4-235n(A)
900 x 850

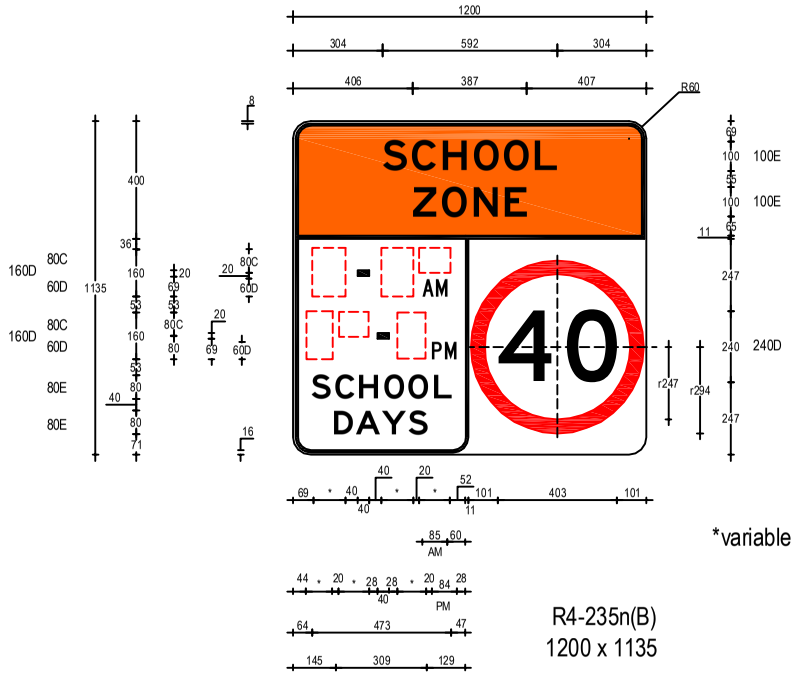


R4-235n(B)
1200 x 1135

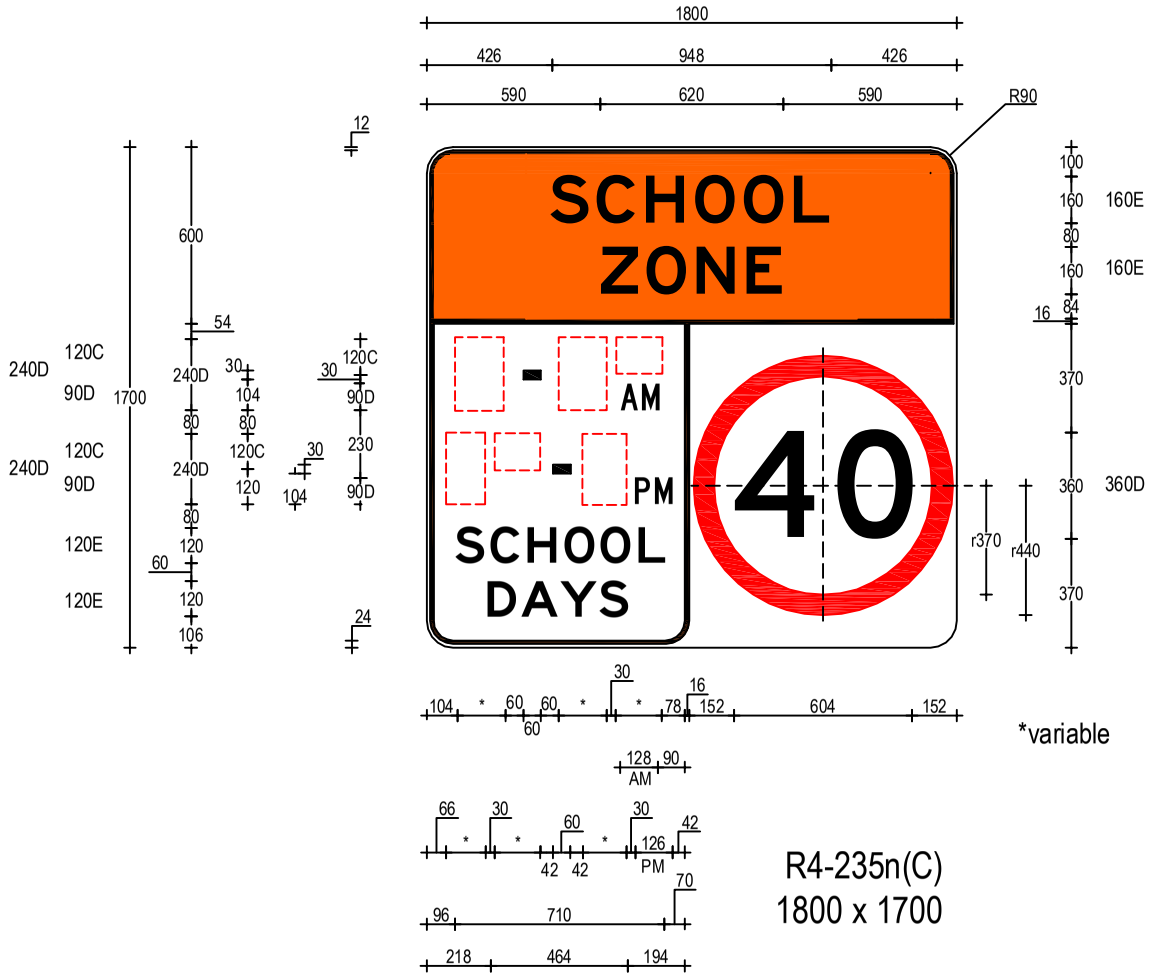

R4-235n(C)
1800 x 1700

Note:- For standard times (8-9.30am & 2.30-4pm) use R4-230n

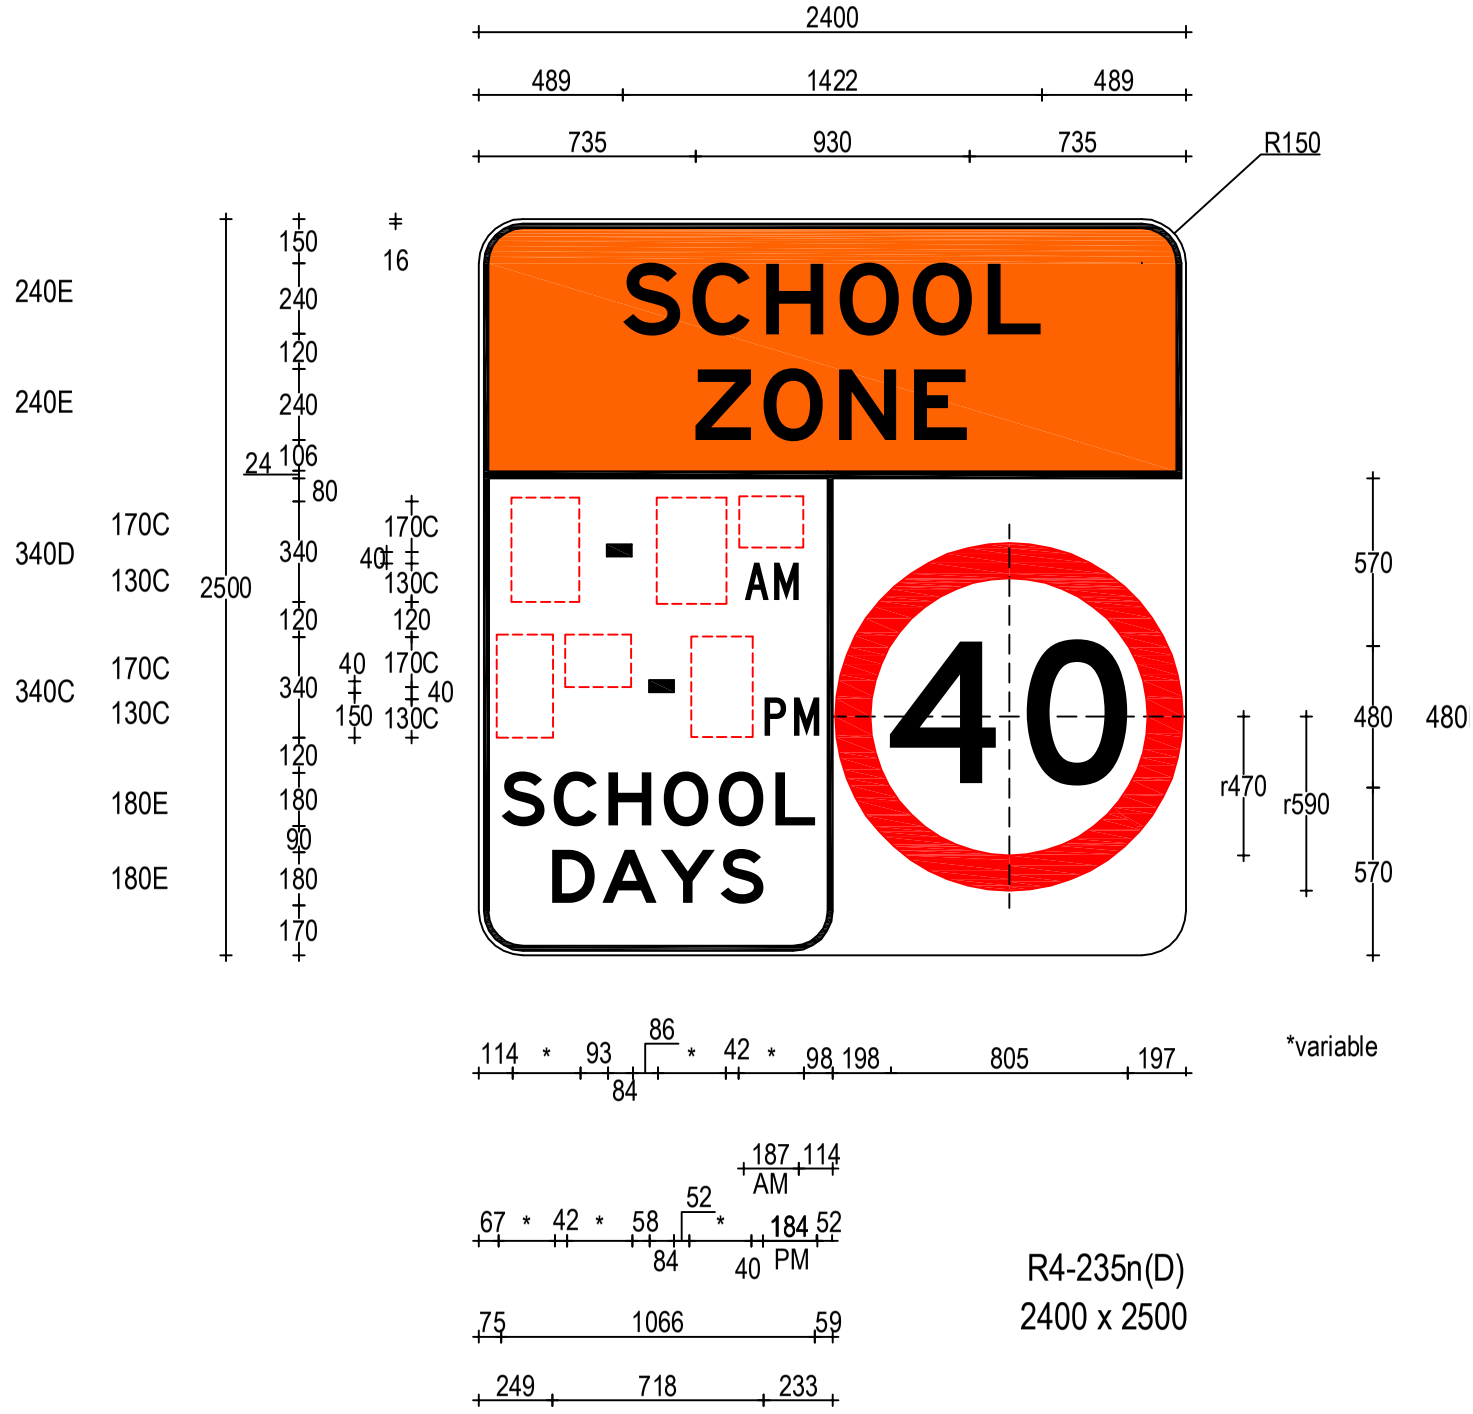

R4-235n(D)
2400 x 2500

ACCEPTED FOR CONSTRUCTION

THIS DRAWING MAY BE PREPARED IN COLOUR AND MAY BE INCOMPLETE IF COPIED
50mm ON A3 SIZE ORIGINAL

QR CODE	Scan to Check Document Version	REV	DATE	AMENDMENT / REVISION DESCRIPTION	APPROVAL
		01	23-08-18	AS Fonts & material classification revised	P.Oliver

DRAWING FILE LOCATION / NAME: H:\SIGNS\TTT\DRAWINGS\PLOT\REGULAT\R4-235n.DWG

MATERIALS: ALUMINIUM SIGN
BLACK LEGEND AND BORDER
TOP PANEL: CL.400 FLUORESCENT ORANGE REFL GROUND
BOTTOM PANELS:- CL.400 RED REFL TIMES & ANNULUS
ON CL.400 WHITE REFLECTORISED GROUND

ALL DIMENSIONS ARE IN MILLIMETRES UNLESS OTHERWISE SPECIFIED

SIGN TO BE MANUFACTURED IN ACCORDANCE WITH RMS QA SPECIFICATION 3400

DESIGNED
SIGNED
NAME M.Davies
DATE 31-07-19

REVIEWED
SIGNED
NAME J.Rozos
DATE 31-07-19

VERIFIED
SIGNED
NAME P.Oliver
TITLE Manager Guidance & Delineation
DATE 31-07-19

Transport Roads & Maritime Services
NSW GOVERNMENT

PREPARED BY
GUIDANCE AND DELINEATION UNIT
TRAFFIC ENGINEERING SERVICES
TECHNICAL AND PROJECT SERVICES

REGULATORY SIGN
R4-235N
SCHOOL ZONE (Times) SCHOOL DAYS

A

SHEET 1 OF 1

SCALE: 1:20 | EDMS No. XXXXXXXXX | SHEET No. 1 | ISS 0

© Roads and Maritime Servic