


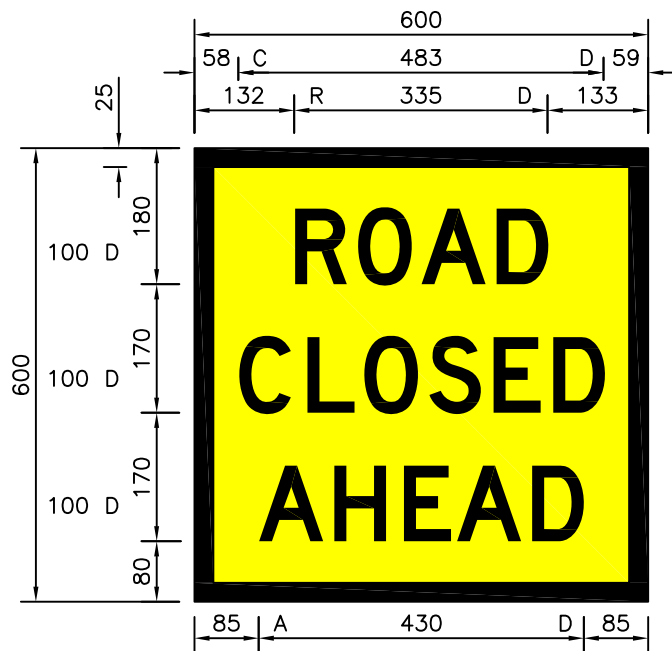

NOTE:

To be used in multi-message sign frames only.



Black

Yellow class 1

Note: Letters & Numerals AS1744:2015.

 Government of South Australia Department of Planning, Transport and Infrastructure	TEMPORARY WARNING SIGN 'Road Closed Ahead'	
Road and Marine Services Traffic Services, Traffic Solutions Unit	Authorisation: 	TM1-43A
Drawn: A. Simister	Scale: 1:10	Date: 9 January, 2020