


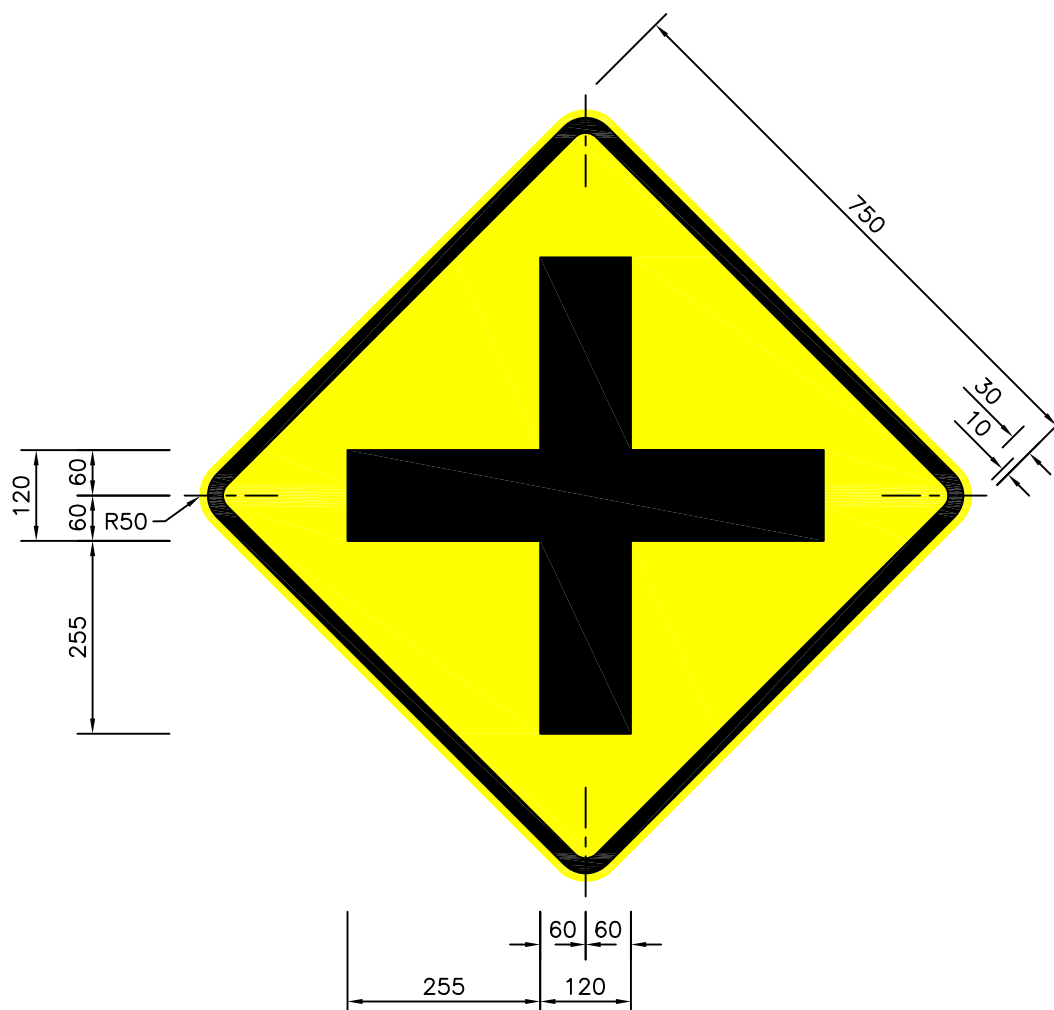

NOTE:

This sign shall only be used for unsealed cross road intersections without a give way or stop sign.

(Refer DPTI Operational Instruction 2.37)



Black

Yellow (retroreflective)

Scale: 1:10

ALL DIMENSIONS ARE IN MILLIMETRES

Total Sign Area: 0.56 sqm

Sign Type: Warning

Location: Various

Drawn: A. Simister
Edition: A Rev: 0
Date: 18 March, 2015

Authorisation:

Date:

TES 18903