



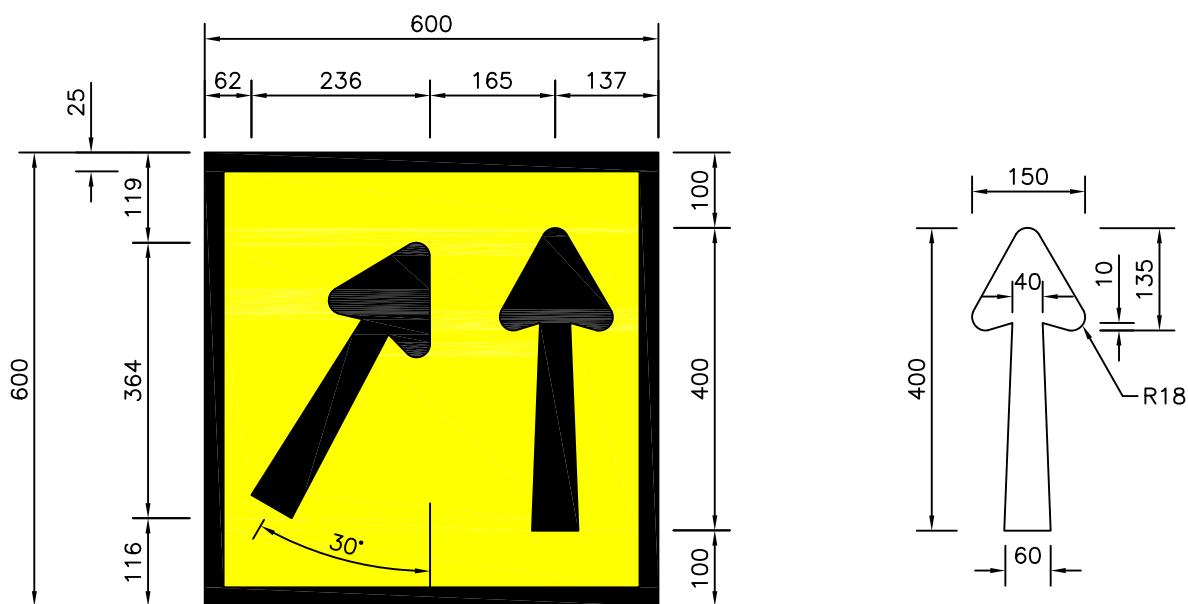

NOTE:
To be used in multi-message
sign frames only.

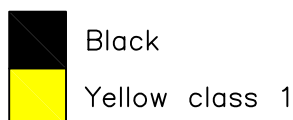

Note: Letters & Numerals AS1744:2015.

 Government of South Australia Department of Planning, Transport and Infrastructure	TEMPORARY WARNING SIGN 'Merge Right - Left Lane'		
Road and Marine Services Traffic Services, Traffic Solutions Unit	Authorisation: 	TM10-SA116A	
	Date: 9 January, 2020		

Drawn: A. Simister

Scale: 1:10