



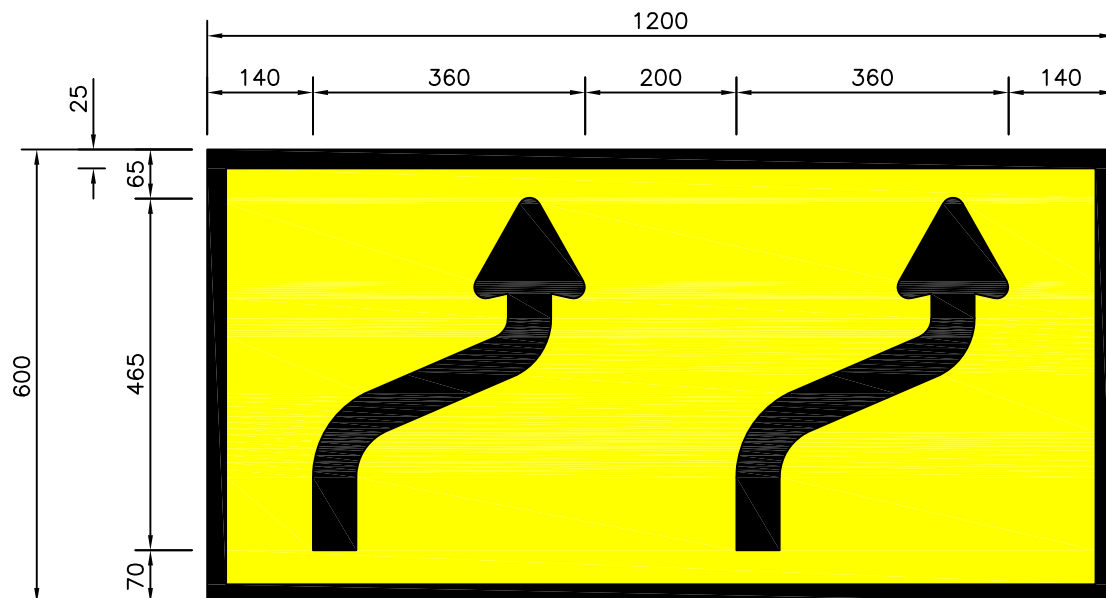

NOTE:

To be used in multi-message sign frames only.

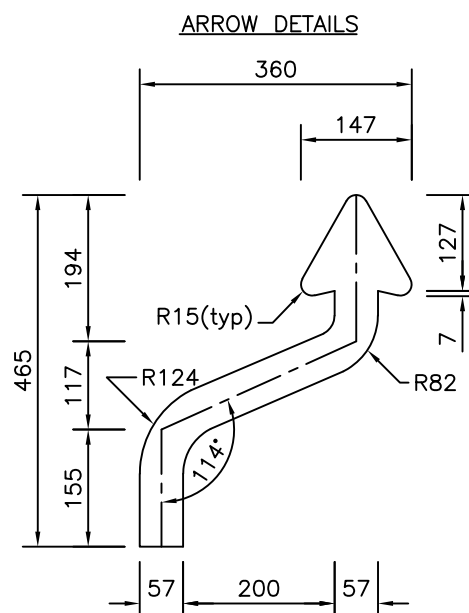

Black

Yellow class 1

Note: Letters & Numerals AS1744:2015.



Government of South Australia
Department of Planning,
Transport and Infrastructure

Road and Marine Services
Traffic Services, Traffic Solutions Unit

Drawn: A. Simister

Scale: 1:10

Authorisation:

Date: 9 January, 2019

TEMPORARY WARNING SIGN
'Lanes Status'

TM10-SA14C