


SIGN SIZE, mm
W3-SA4A 600X600
W3-SA4B(Illust.) 750X750

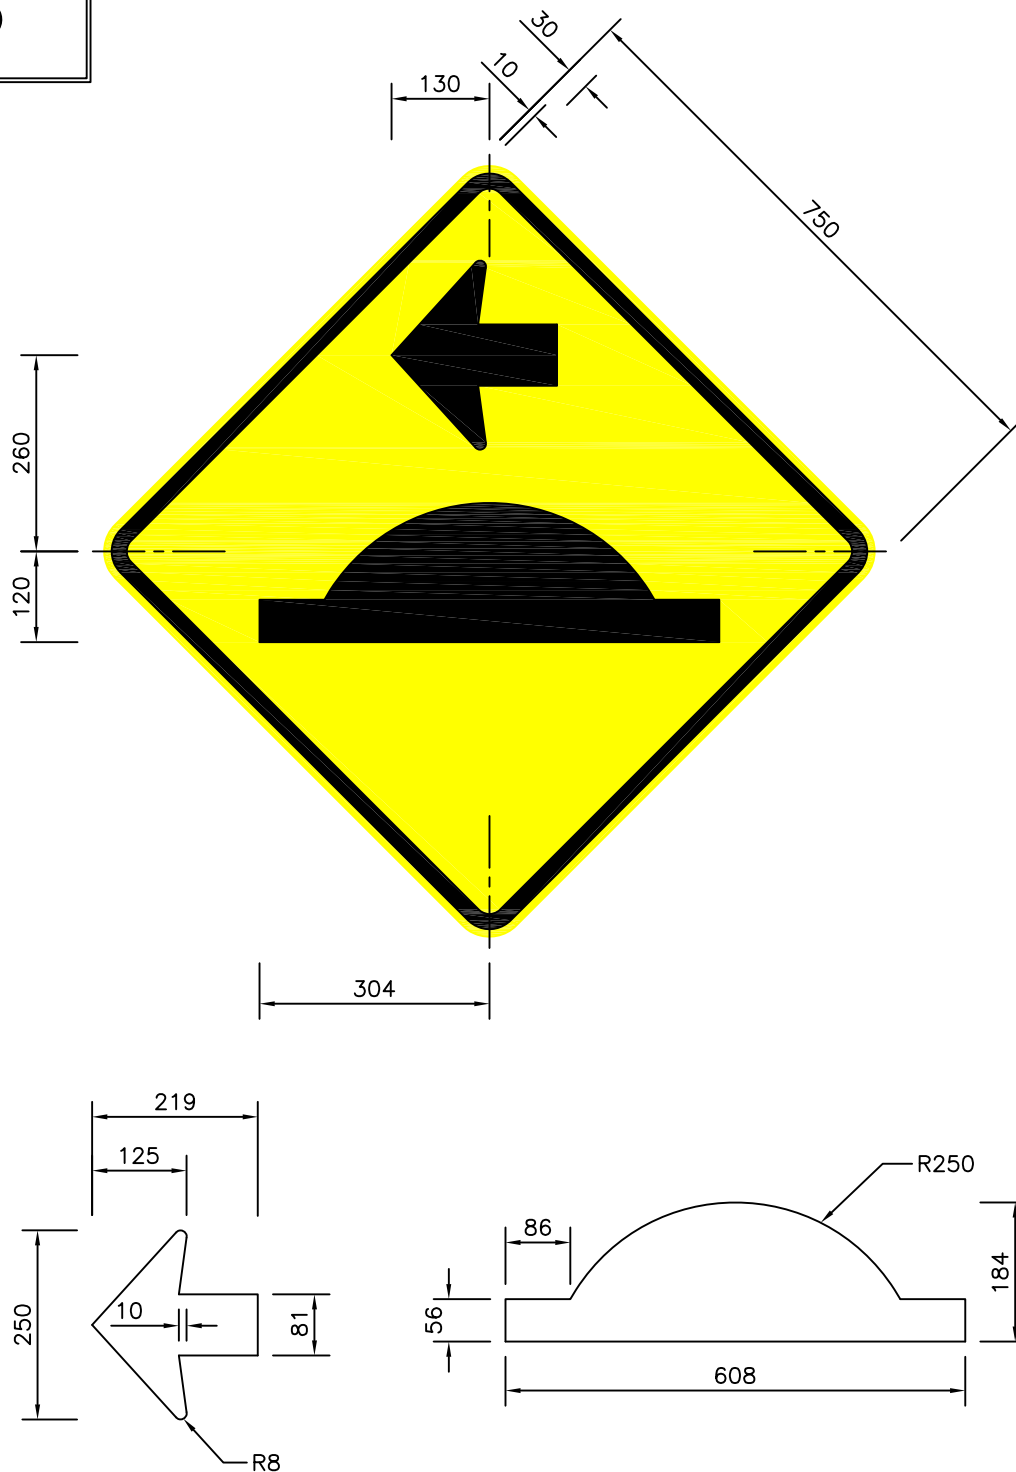

Note: Letters & Numerals AS1744:2015.

 Government of South Australia Department of Planning, Transport and Infrastructure	WARNING SIGN 'Road Hump(s) on Side Road'		
Safety & Service Division Traffic Operations		Authorisation: 	W3-SA4(LorR)
Drawn: A. Simister	Scale: 1:10	Date: 17 July, 2017	