
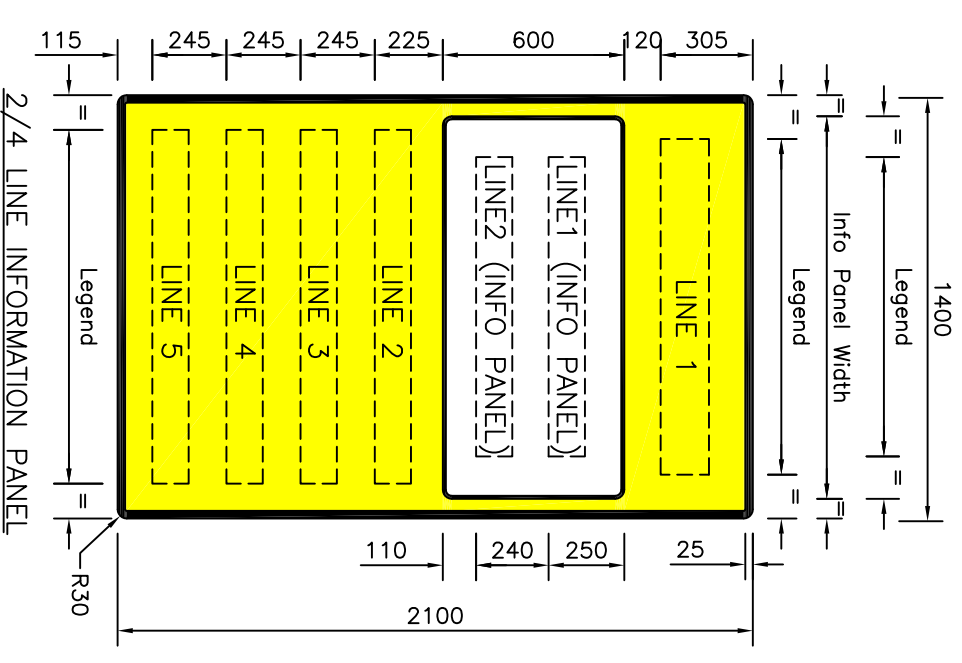
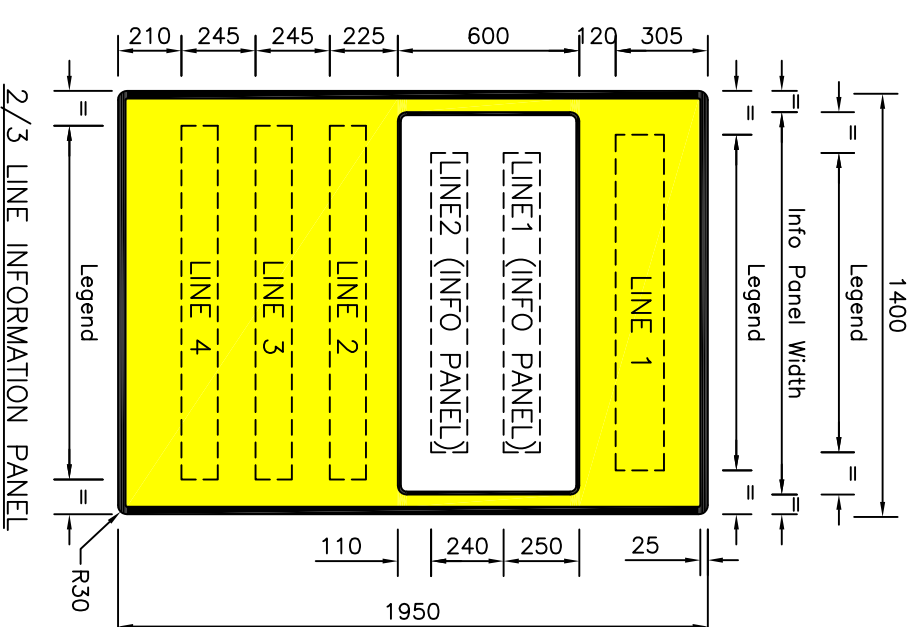


**Safety & Service Division
Traffic Operations, Traffic Solutions Unit
Specific Road Signs - Specifications, South Australia**

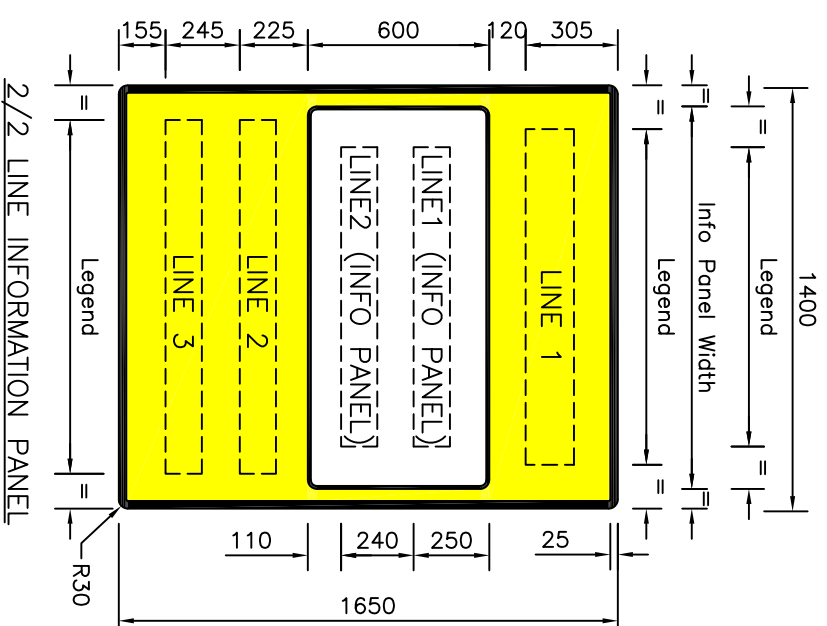

NOTES:

MAIN PANEL:

Line 1: 160mm U.C. Series 'C' or 'D' to fit.

Line 2-5: 120mm U.C. Series 'C' to fit.

Numerals: 120mm Series 'C' to fit.

SPECIFIC TEXT:

"USE ALTERNATIVE ROUTE TO AVOID DELAY", 100

U.C. Series 'C'

"DELAYS CAN BE EXPECTED" 120 U.C. Series 'C'

INFORMATION PANEL:




Letters: 140mm U.C. Series 'C' or 'D' to fit.

Border: 10mm wide border.

Panel corner radius = 30mm.

POST:

1400mm sign width can be installed on one post, >1400mm (where necessary) use two posts.

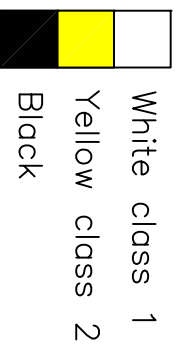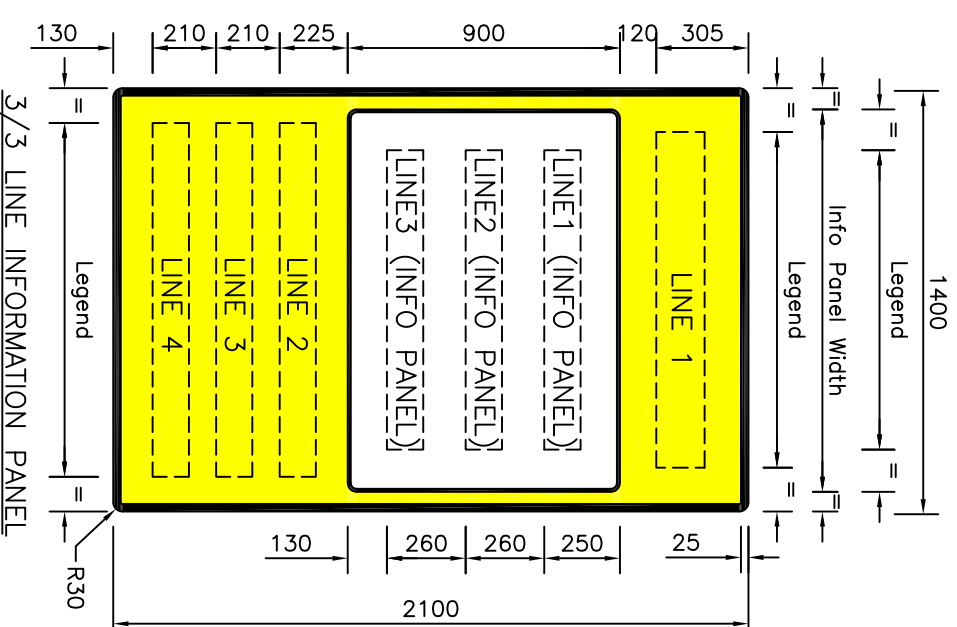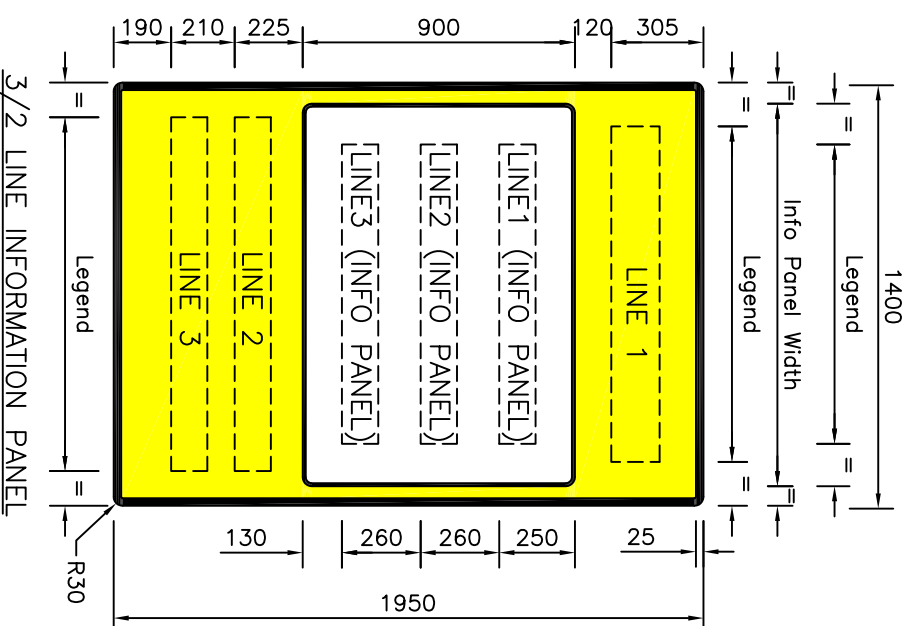

Scale: 1:25

ALL DIMENSIONS ARE IN MILLIMETRES

Total Sign Area: Varies

Sign Type: Temporary Warning

Location: Various

Drawn: A. Simister
Edition: A Rev: 3
Date: 3 August, 2017

Authorisation:
Date:

- NOTE -

Series 2000 Font

TES 13004-1