


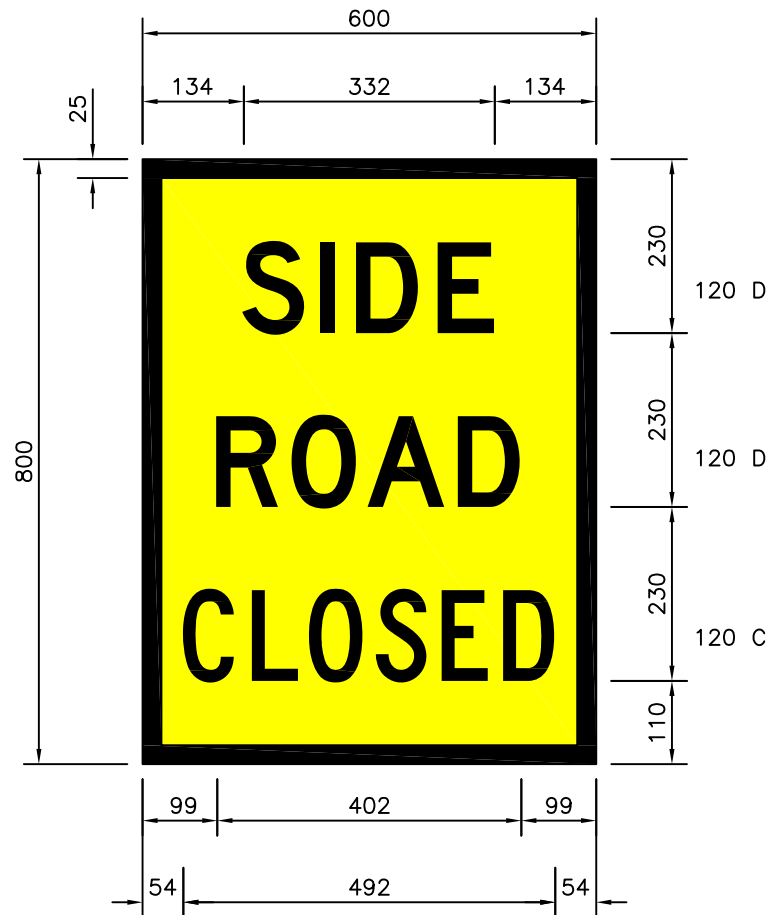

Note: For larger Standard size refer to AS 1743.
 *AA size shall only be used on local residential roads in 40km/h or 50km/h traffic areas.

 Yellow (retro-reflective)

 Black

Note: Letters & Numerals AS1744:2015.

 Government of South Australia Department of Planning, Transport and Infrastructure	TEMPORARY WARNING SIGN 'Side Road Closed (3 Lines)'	
Safety & Service Division Technical Services Section Drawn: A. Simister	Authorisation:  Date: 4 October, 2017	T1-32AA
	Scale: 1:10	