


Note: Letters & Numerals AS1744:2015.

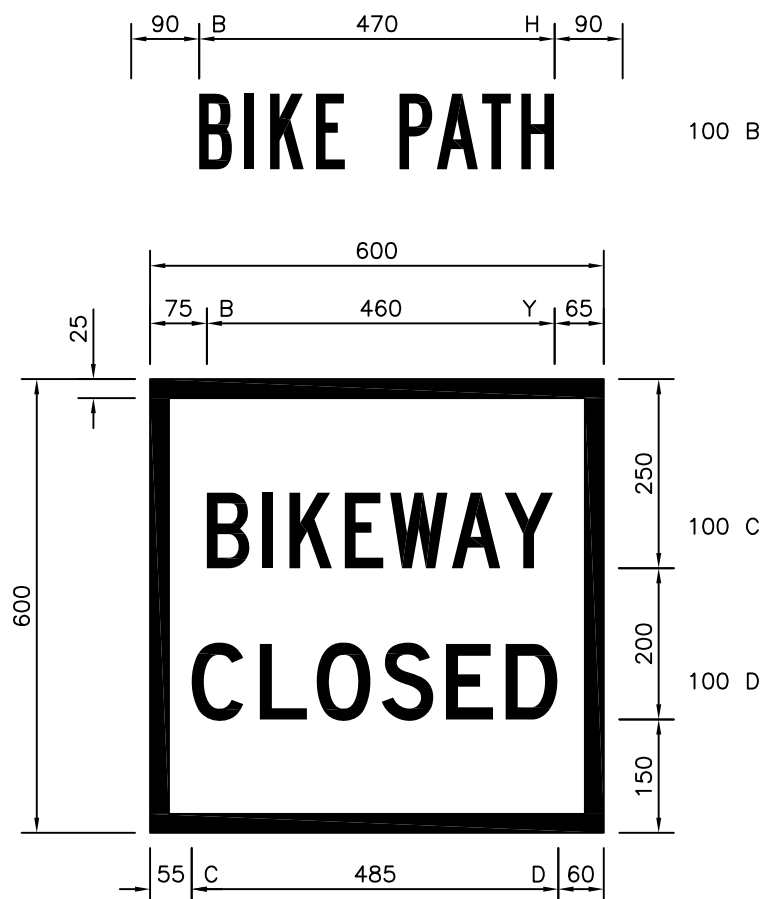

Government of South Australia
Department of Planning,
Transport and Infrastructure

Road and Marine Services
Traffic Services, Traffic Solutions Unit

Drawn: A. Simister

Scale: 1:10

TEMPORARY WARNING SIGN
'Bikeway / Bike Path Closed'

Authorisation:

Date:

TM8-SA110A